PLANTA DE TRANSFORMACIÓN DE LÁCTEOS

Municipio de Marulanda – Caldas · Planos arquitectónicos — versión de lectura

CONTENIDO

Vistas ampliadas (A3, una por página)

Pág.	Plancha	Contenido
2	A-001	Implantación general — Localización del lote, vías y perfiles
3	A-002	Planta piso -1 — Nivel N -2.85
4	A-003	Planta piso 1 — Nivel N ±0.00 / N +0.15 — zona de producción
5	A-003	Planta piso 2 — Nivel N +3.19 — almacén de empaques, oficina
6	A-002	Planta de cubiertas — Nivel N +8.41
7	A-004	Fachada norte
8	A-004	Alzado fachada oeste
9	A-004	Alzado fachada este
10	A-005	Corte A-A'
11	A-005	Corte B-B'
12	A-005	Corte C-C'
13	A-005	Corte D-D'

Planchas completas (formato original 100 × 70.7 cm)

14	A-001	Implantación y notas generales
15	A-002	Planta piso -1 y planta de cubiertas
16	A-003	Plantas piso 1 y piso 2
17	A-004	Fachada norte, alzados oeste y este
18	A-005	Cortes A-A', B-B', C-C' y D-D'

CÓMO LEER LOS COLORES

━	Muros cortados
■	Columnas y muros en corte (relleno)
—	Puertas y ventanas
—	Escaleras y rampas
—	Mobiliario, aparatos y equipos
—	Líneas de fachada
—	Proyecciones y líneas de fondo
-·-·-	Ejes estructurales (A, B, C… / 1, 2, 3…)
—	Cotas (medidas en metros)
Aa	Niveles (N ±0.00)
Aa	Nombre y área de cada espacio
Aa	Referencias de corte y acabados
▭	Tinte de piso / superficies
▨	Terreno, gravilla y tramas

Generado a partir de ARQ_PLANTA LACTEOS.dwg (AutoCAD 2018). Se reasignaron colores y grosores por capa para facilitar la lectura en pantalla e impresión; la geometría, las cotas y los textos no se modificaron.
No incluye logos ni objetos incrustados (OLE) del rótulo, ni el mapa de localización (imagen externa).
Documento de consulta: para obra, licencia o contratación usar los planos originales firmados.

IMPLANTACIÓN GENERAL

Localización del lote, vías y perfiles · Plancha A-001 · Escala original 1:150 · En esta hoja A3 ≈ 1:319

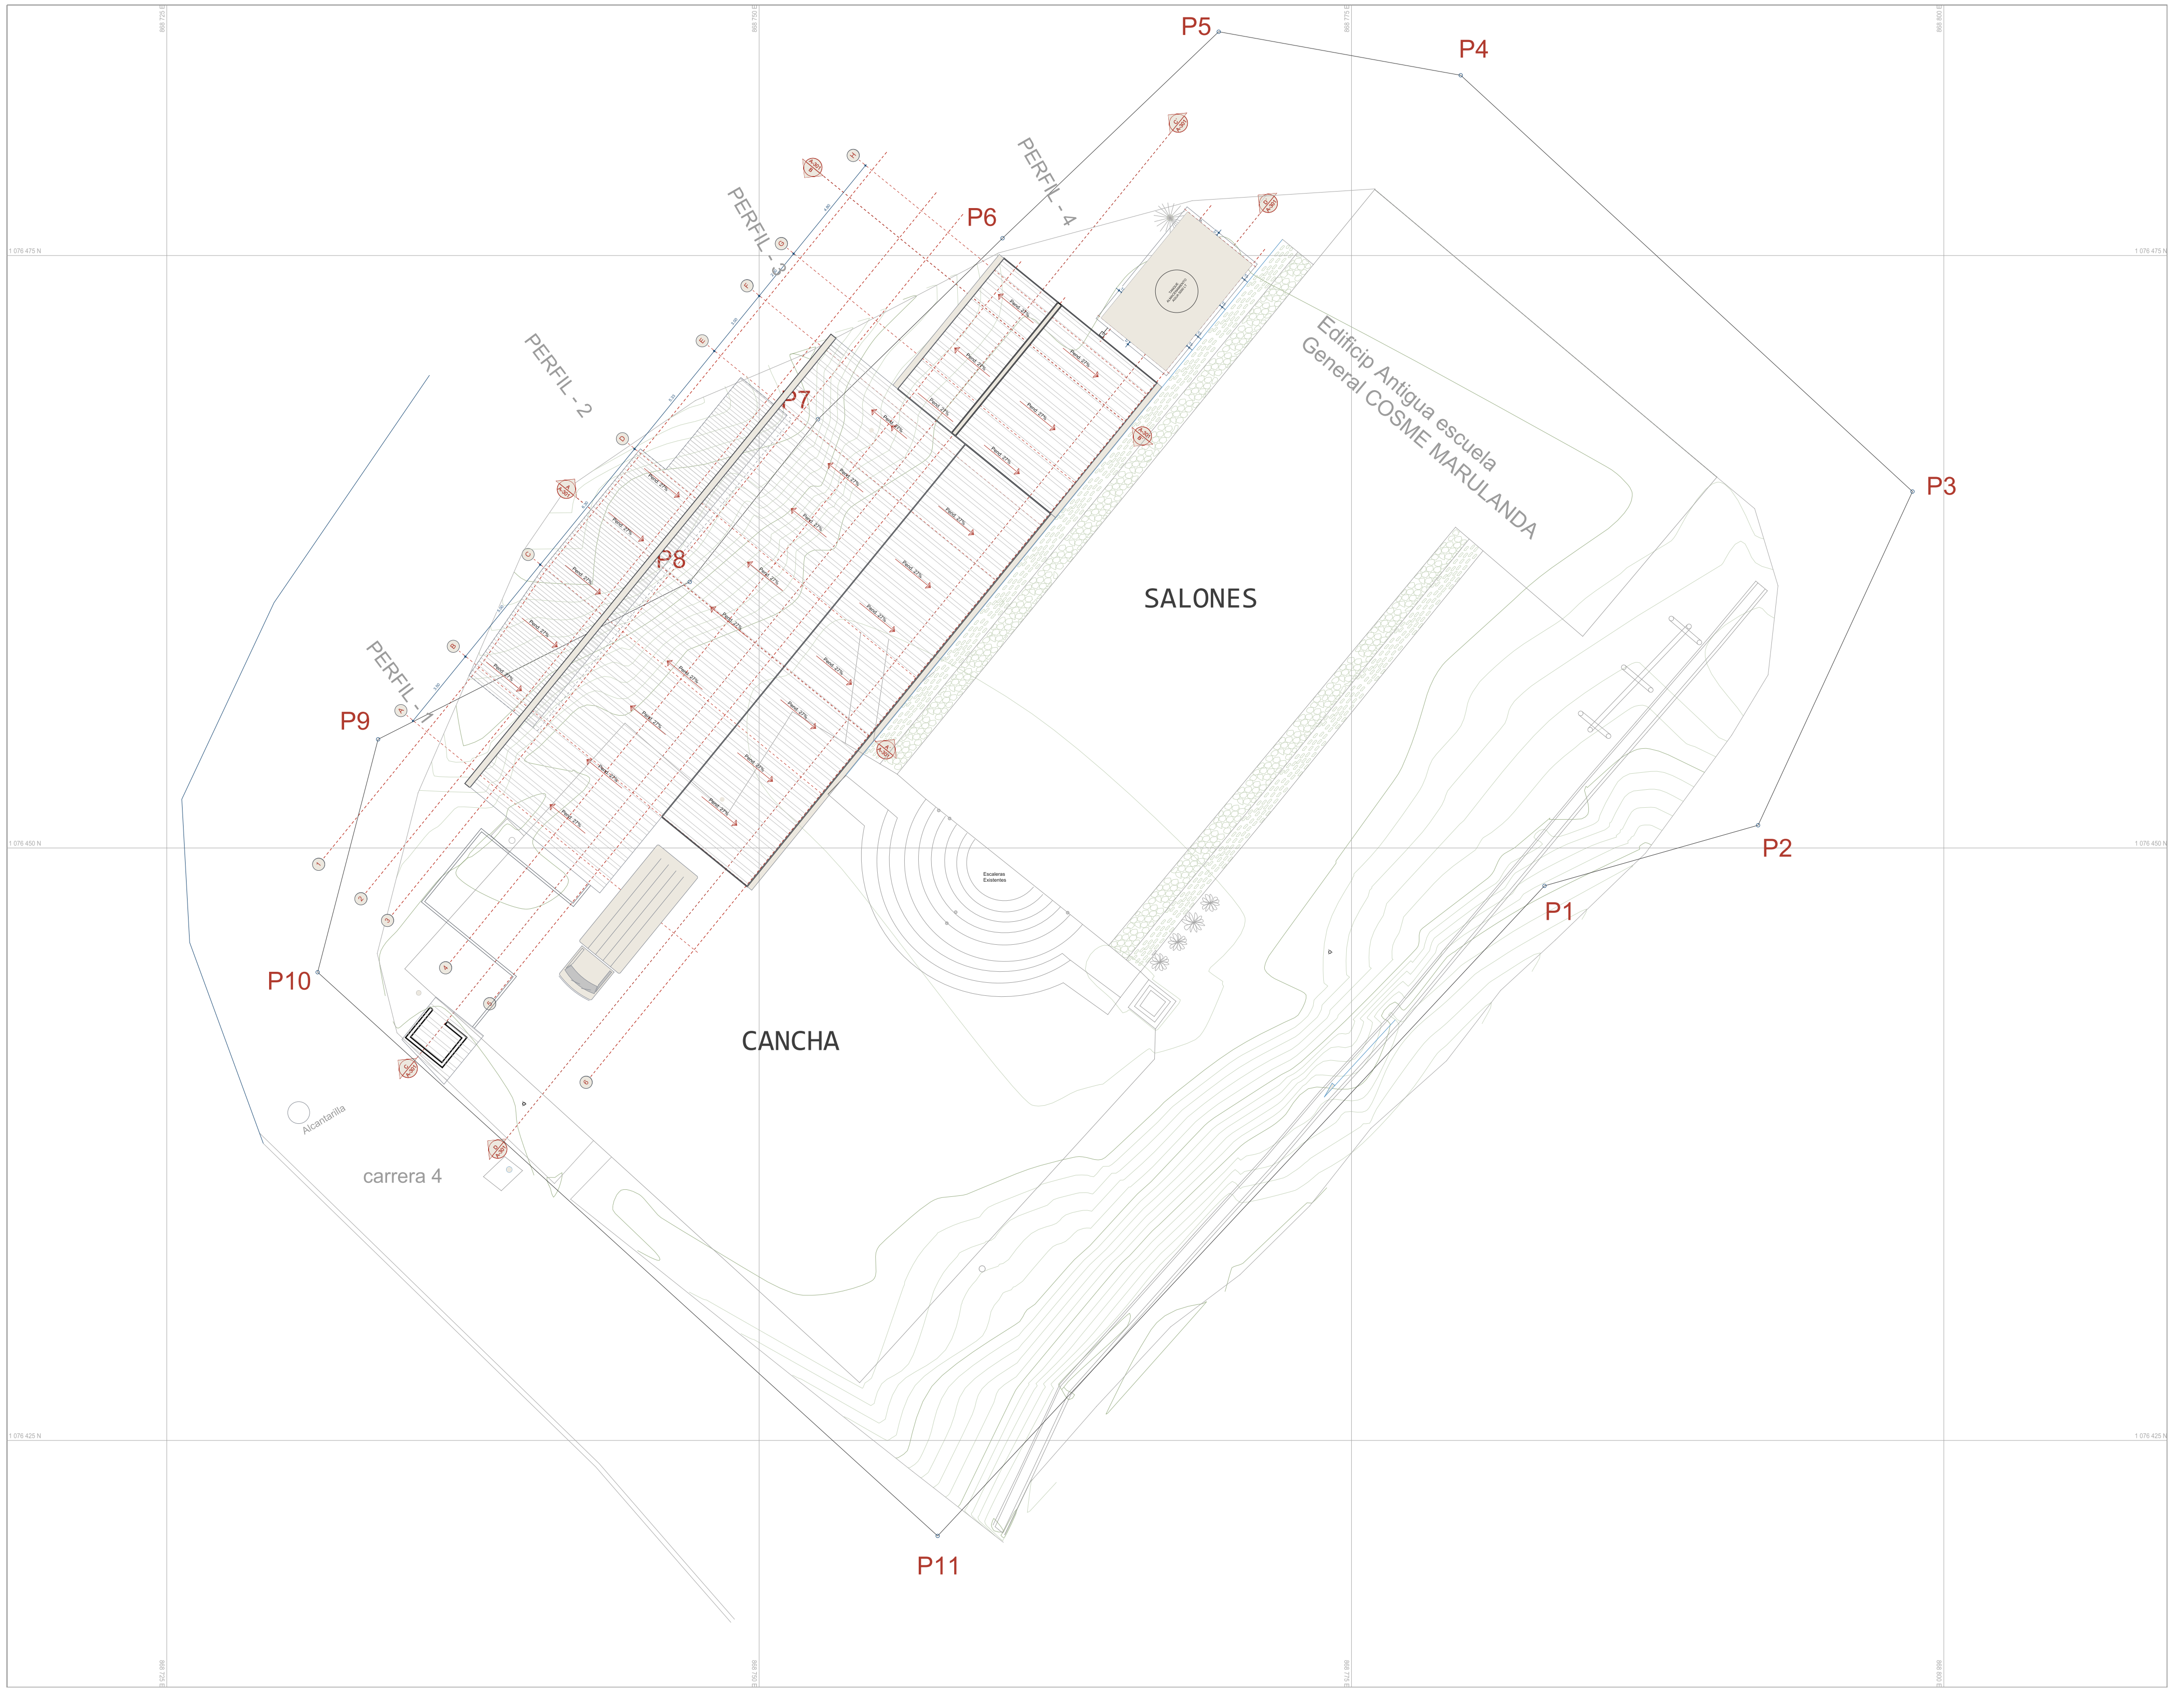
P5
P4
P6
PERFIL - 4
PERFIL - 3
PERFIL - 2
P7
P8
PERFIL - 1
P9
P10
P3
P2
P1
P11
Edificio Antigua escuela General COSME MARULANDA
SALONES
CANCHA
Alcantarilla
carrera 4

0 20 m

Muros · Puertas/ventanas · Equipos/mobiliario · Cotas (m) · -·-·- Ejes · Aa Niveles · Aa Espacios

PLANTA PISO -1

Nivel N -2.85 · Plancha A-002 · Escala original 1:75 · En esta hoja A3 ≈ 1:145

Planta de transformación de lácteos

Municipio de Marulanda – Caldas ·

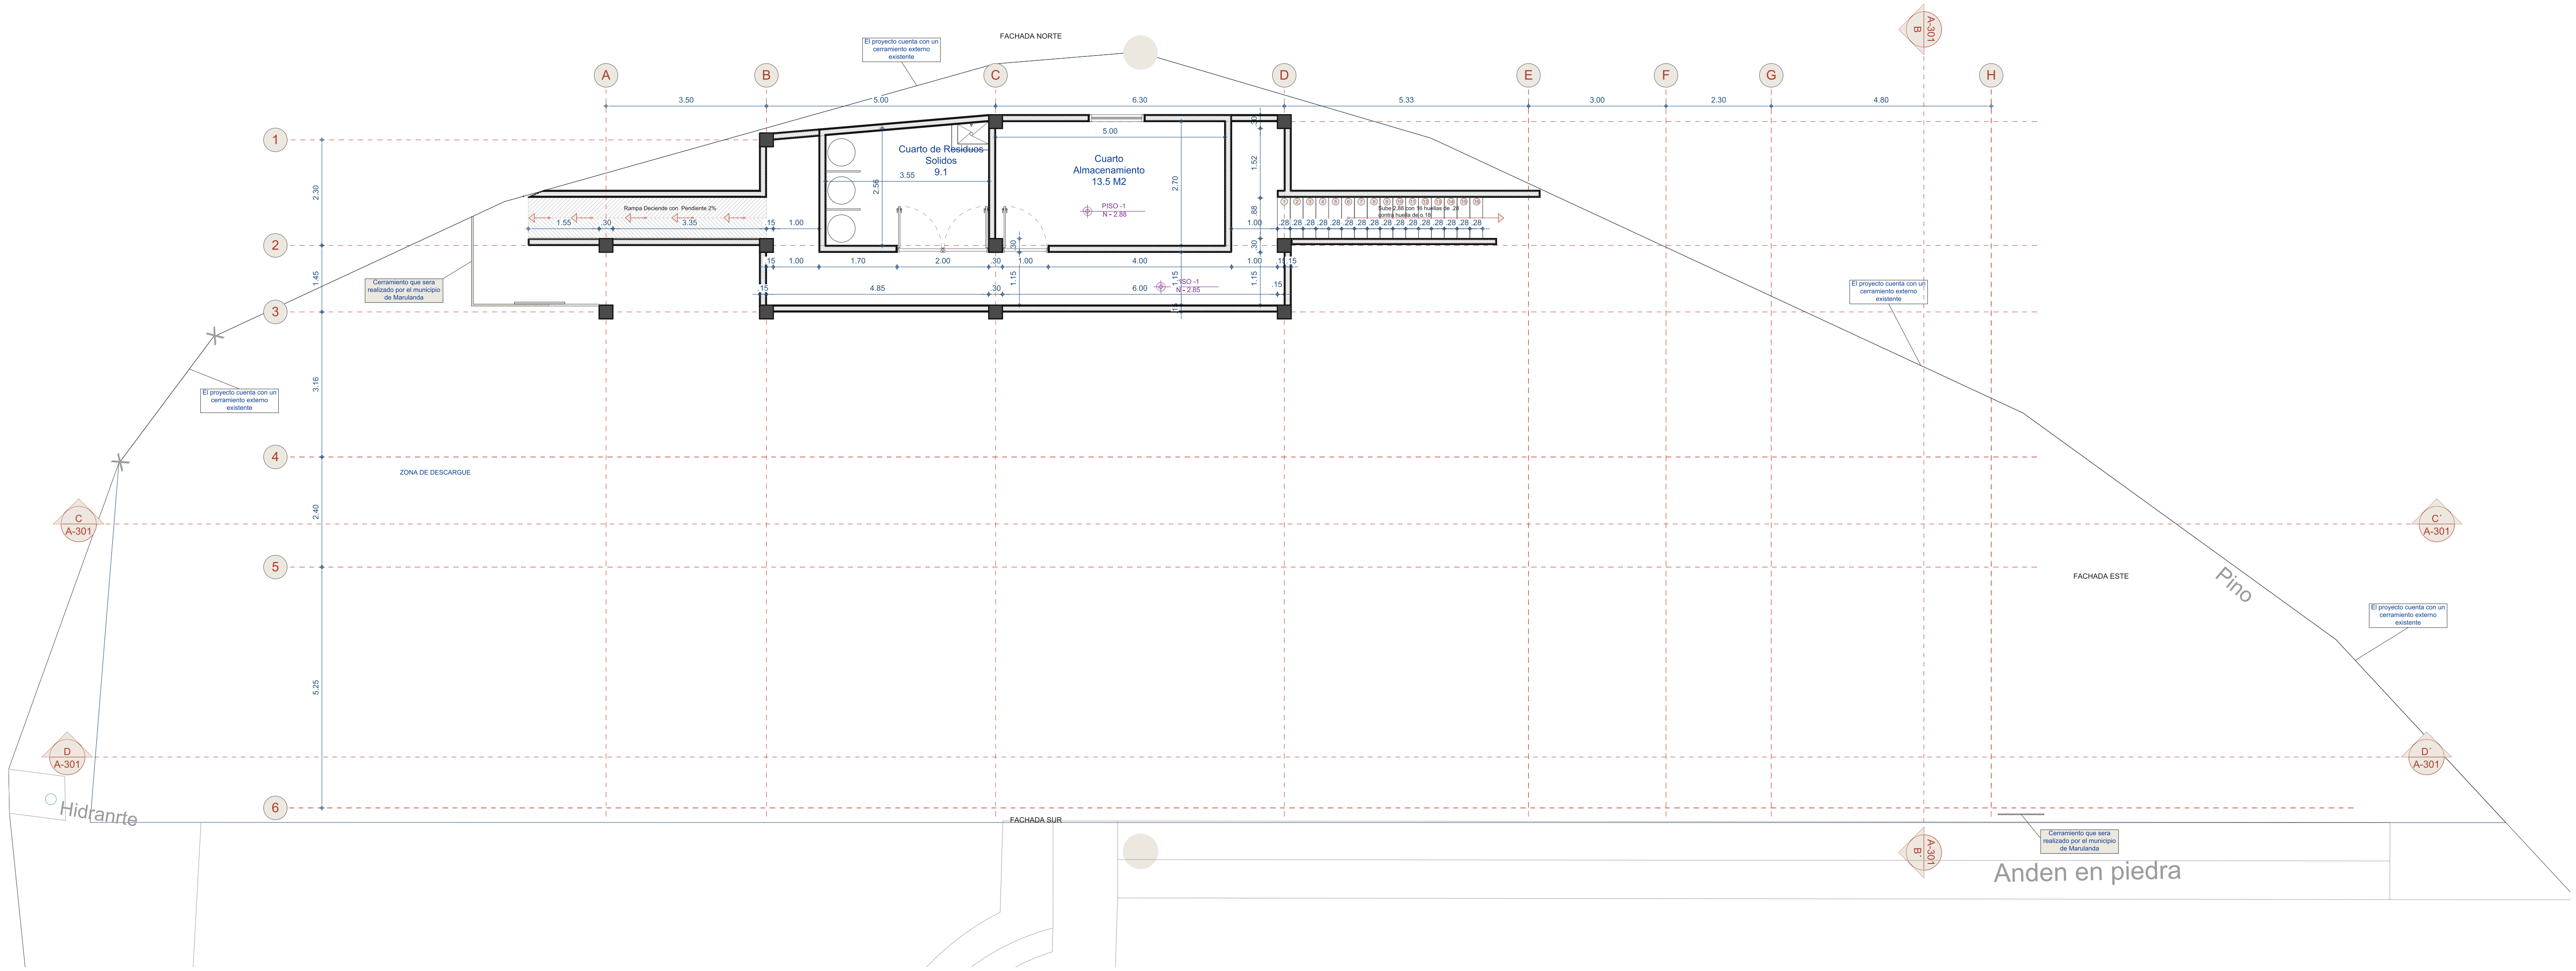
FACHADA NORTE
El proyecto cuenta con un cerramiento externo existente
A
B
C
D
E
F
G
H
3.50
5.00
6.30
5.33
3.00
2.30
4.80
1
2
3
4
5
6
2.30
1.45
3.16
2.40
5.25
Cuarto de Residuos Solidos 9.1
3.55
2.56
Cuarto Almacenamiento 13.5 M2
5.00
2.70
PISO -1 N - 2.88
PISO -1 N - 2.85
Rampa Deciende con Pendiente 2%
1.55
.30
3.35
.15
1.00
1.70
2.00
4.00
4.85
6.00
1.15
1.52
.88
Sube 2.88 con 16 huellas de .28 contra huella de o.18
.28
Cerramiento que sera realizado por el municipio de Marulanda
ZONA DE DESCARGUE
C A-301
D A-301
C´ A-301
D´ A-301
B A-301
B´ A-301
FACHADA ESTE
Pino
Hidranrte
FACHADA SUR
Anden en piedra

0 10 m

Muros

Puertas/ventanas

Equipos/mobiliario

Cotas (m)

Ejes

Aa Niveles

Aa Espacios

PLANTA PISO 1

Planta de transformación de lácteos

Nivel N ±0.00 / N +0.15 — zona de producción · Plancha A-003 · Escala original 1:75 · En esta hoja A3 ≈ 1:139

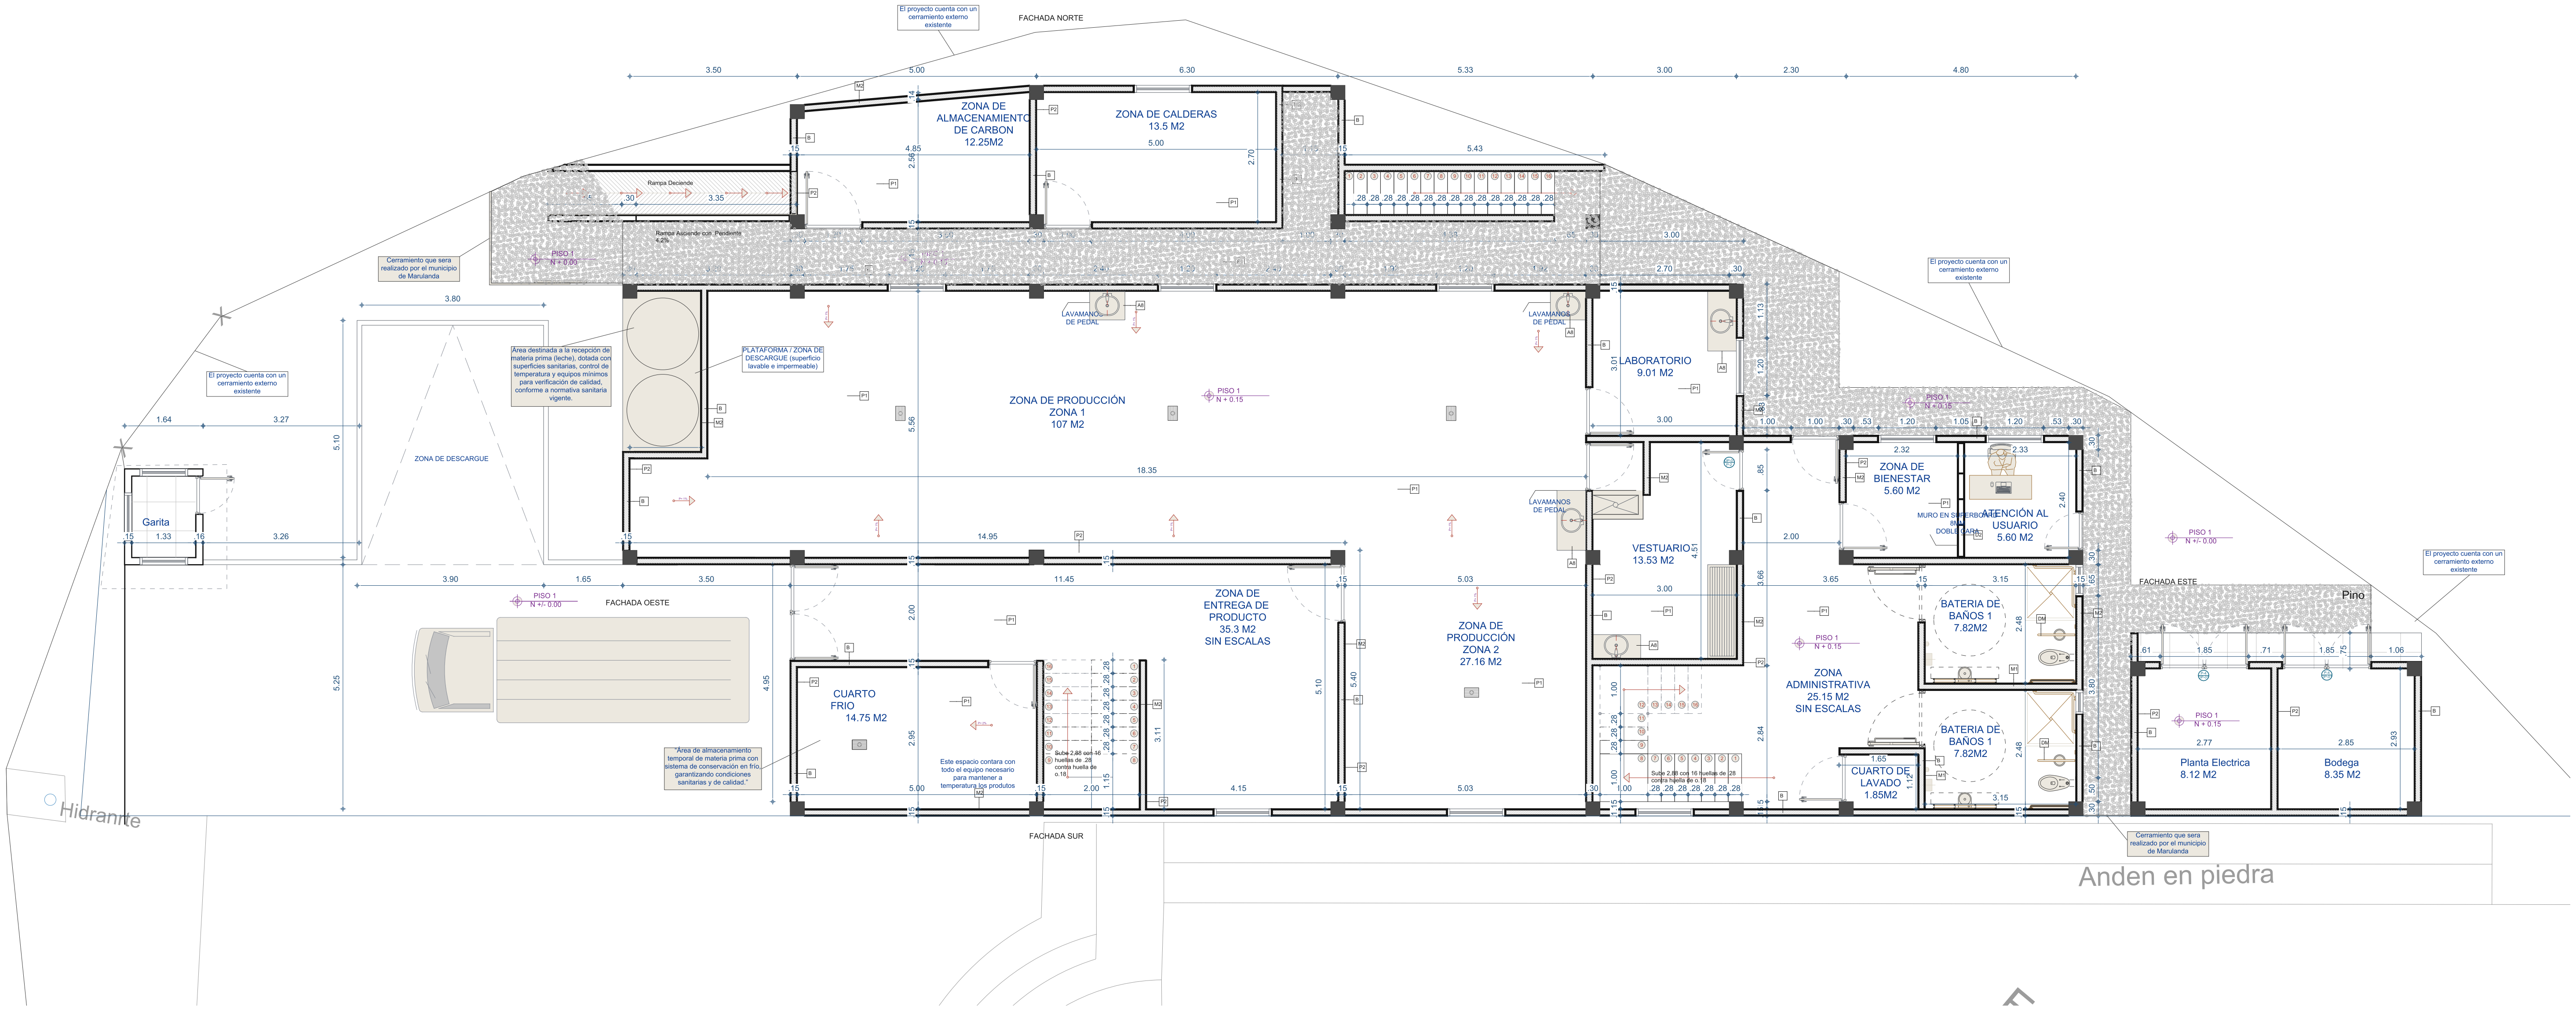
FACHADA NORTE
El proyecto cuenta con un cerramiento externo existente
ZONA DE ALMACENAMIENTO DE CARBON 12.25M2
ZONA DE CALDERAS 13.5 M2
Rampa Desciende
Rampa Asciende con Pendiente 4.2%
Cerramiento que sera realizado por el municipio de Marulanda
PISO 1 N + 0.15
Area destinada a la recepción de materia prima (leche), dotada con superficies sanitarias, control de temperatura y equipos mínimos para verificación de calidad, conforme a normativa sanitaria vigente.
PLATAFORMA / ZONA DE DESCARGUE (superficie lavable e impermeable)
LAVAMANOS DE PEDAL
ZONA DE PRODUCCIÓN ZONA 1 107 M2
LABORATORIO 9.01 M2
ZONA DE DESCARGUE
Garita
ZONA DE BIENESTAR 5.60 M2
ATENCIÓN AL USUARIO 5.60 M2
MURO EN SUPERBOARD DOBLE CARA
VESTUARIO 13.53 M2
FACHADA OESTE
PISO 1 N +- 0.00
ZONA DE ENTREGA DE PRODUCTO 35.3 M2 SIN ESCALAS
ZONA DE PRODUCCIÓN ZONA 2 27.16 M2
FACHADA ESTE
Pino
BATERIA DE BAÑOS 1 7.82M2
ZONA ADMINISTRATIVA 25.15 M2 SIN ESCALAS
CUARTO FRIO 14.75 M2
"Area de almacenamiento temporal de materia prima con sistema de conservación en frío, garantizando condiciones sanitarias y de calidad."
Este espacio contara con todo el equipo necesario para mantener a temperatura los produtos
BATERIA DE BAÑOS 1 7.82M2
CUARTO DE LAVADO 1.85M2
Planta Electrica 8.12 M2
Bodega 8.35 M2
Hidrante
FACHADA SUR
Anden en piedra

0 10 m

Muros

Puertas/ventanas

Equipos/mobiliario

Cotas (m)

Ejes

Aa Niveles

Aa Espacios

PLANTA PISO 2

Nivel N +3.19 — almacén de empaques, oficina · Plancha A-003 · Escala original 1:75 · En esta hoja A3 ≈ 1:150

Planta de transformación de lácteos

Municipio de Marulanda – Caldas ·

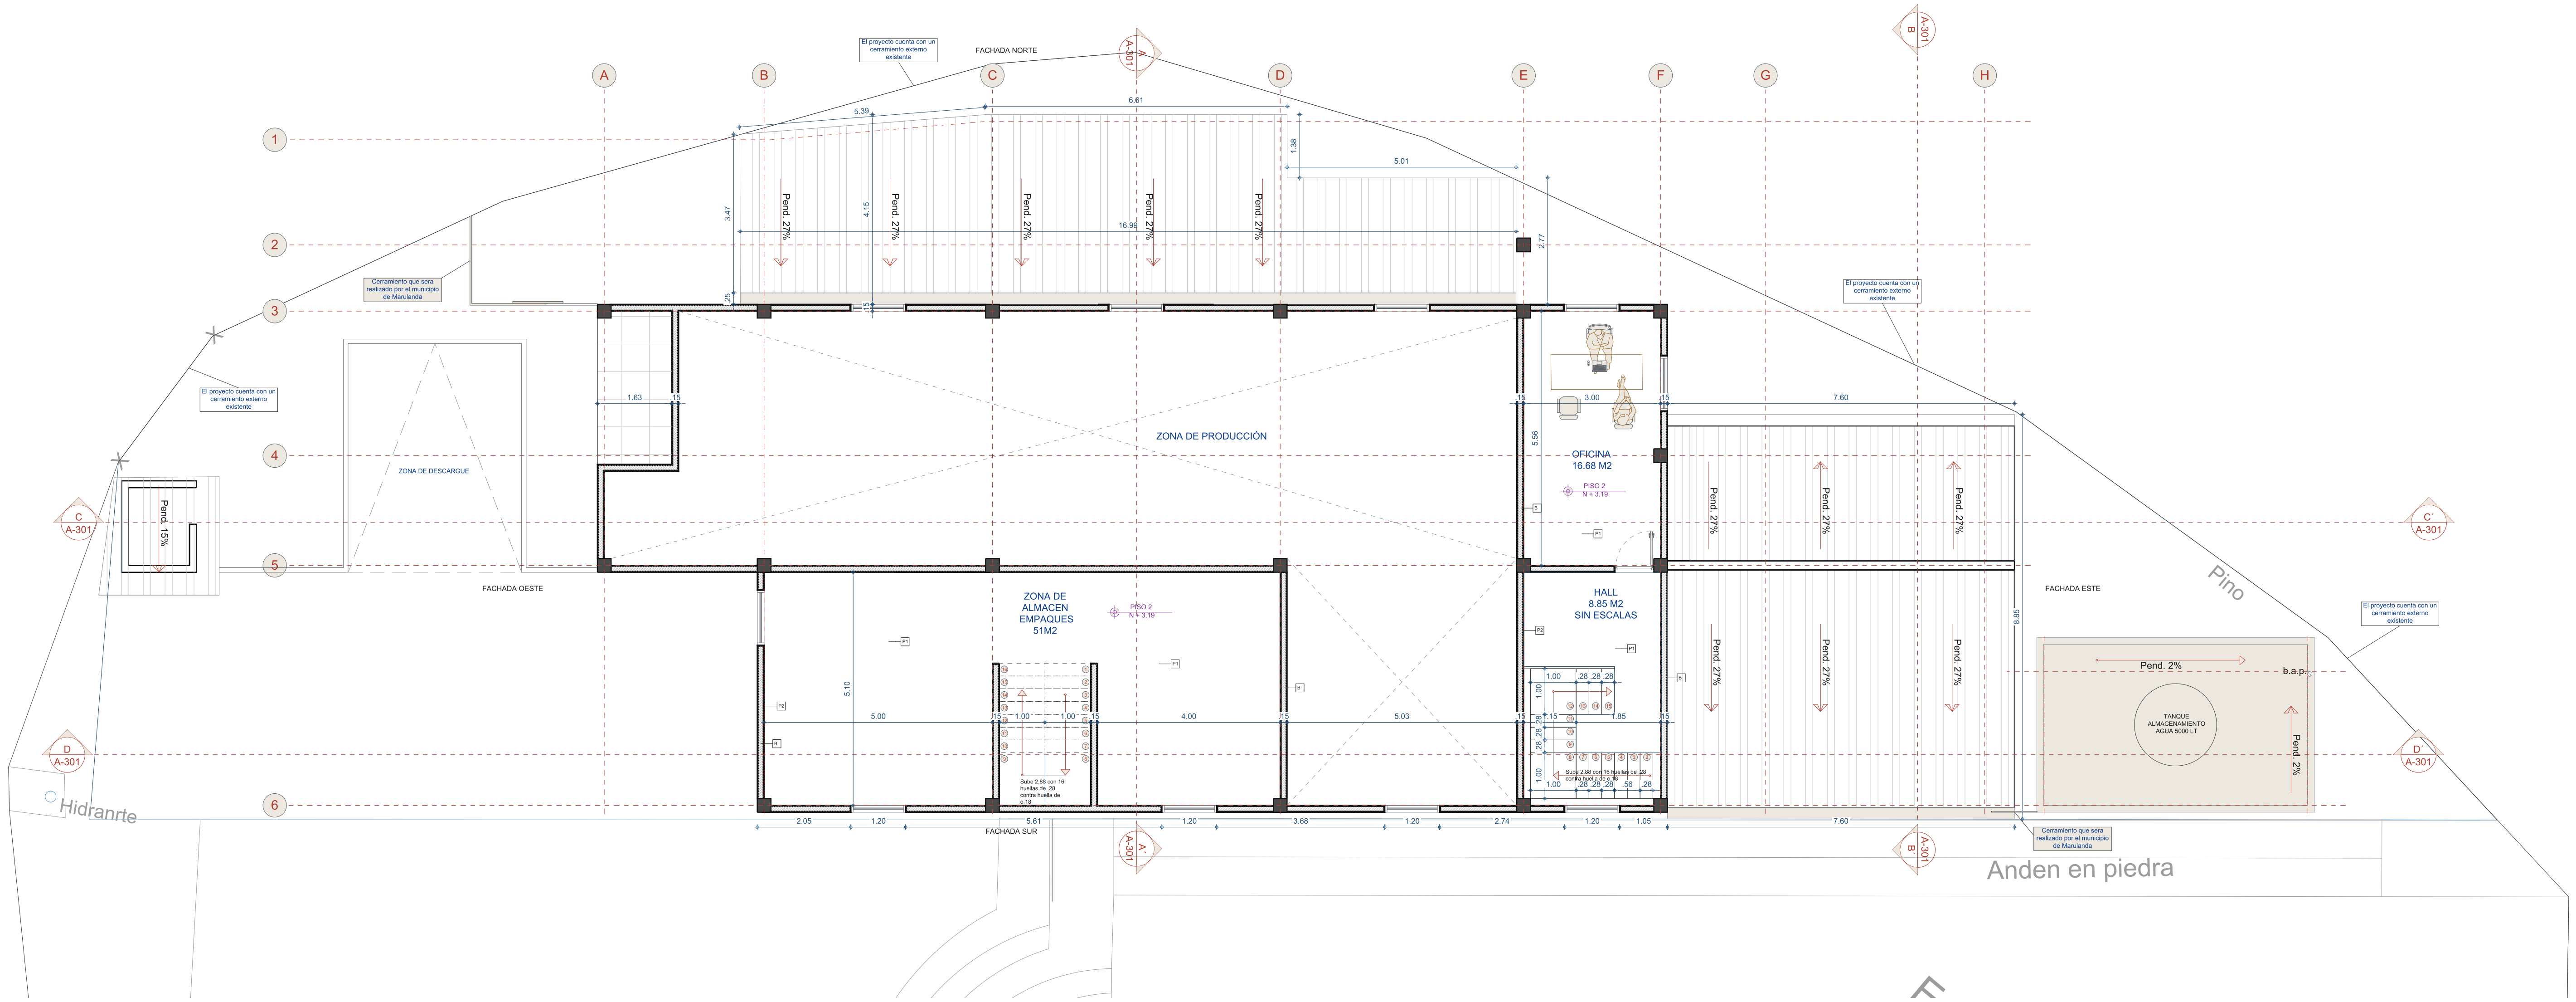
FACHADA NORTE
El proyecto cuenta con un cerramiento externo existente
A B C D E F G H
1 2 3 4 5 6
5.39
6.61
1.38
5.01
3.47
4.15
16.99
2.77
.25
Pend. 27%
Cerramiento que sera realizado por el municipio de Marulanda
El proyecto cuenta con un cerramiento externo existente
1.63
.15
ZONA DE DESCARGUE
ZONA DE PRODUCCIÓN
C A-301
Pend. 15%
FACHADA OESTE
OFICINA 16.68 M2
PISO 2 N + 3.19
3.00
5.56
7.60
HALL 8.85 M2 SIN ESCALAS
Sube 2,88 con 16 huellas de .28 contra huella de o.18
1.00
.28 .28 .28
1.85
.56
8.85
FACHADA ESTE
Pino
El proyecto cuenta con un cerramiento externo existente
C´ A-301
D´ A-301
Pend. 2%
b.a.p.
TANQUE ALMACENAMIENTO AGUA 5000 LT
ZONA DE ALMACEN EMPAQUES 51M2
PISO 2 N + 3.19
P1
P2
B
5.10
5.00
4.00
5.03
D A-301
Hidranrte
2.05
1.20
5.61
3.68
2.74
1.05
FACHADA SUR
A´ A-301
B´ A-301
Cerramiento que sera realizado por el municipio de Marulanda
Anden en piedra

0 10

m

Muros

Puertas/ventanas

Equipos/mobiliario

Cotas (m)

Ejes

Aa Niveles

Aa Espacios

PLANTA DE CUBIERTAS

Nivel N +8.41 · Plancha A-002 · Escala original 1:75 · En esta hoja A3 ≈ 1:148

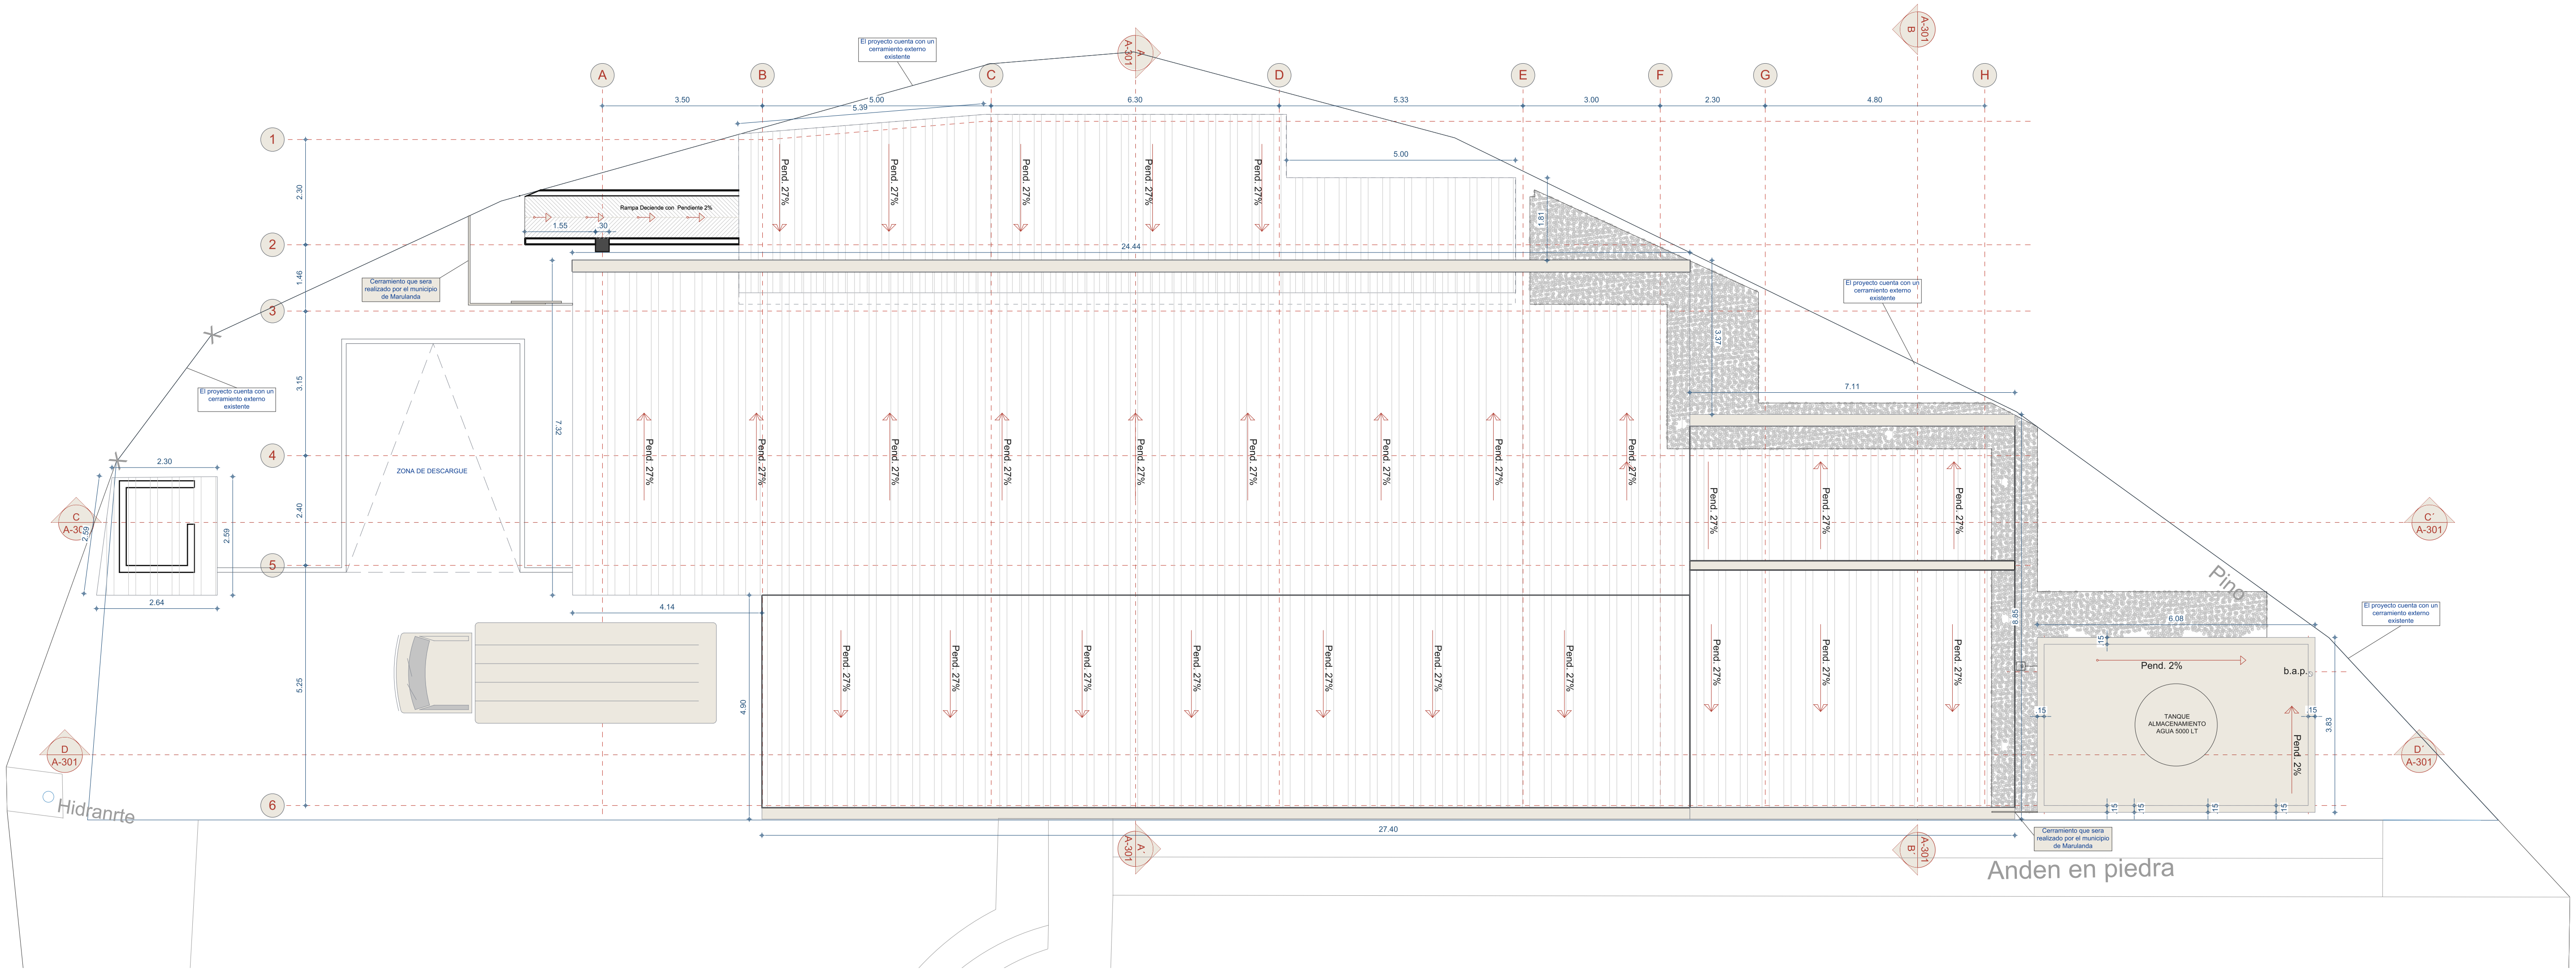
A
B
C
D
E
F
G
H
1
2
3
4
5
6
3.50
5.00
5.39
6.30
5.33
3.00
2.30
4.80
5.00
24.44
7.11
6.08
8.85
3.83
27.40
4.14
4.90
7.32
2.30
1.46
3.15
2.40
5.25
2.59
2.64
1.55
.30
.15
El proyecto cuenta con un cerramiento externo existente
Cerramiento que sera realizado por el municipio de Marulanda
Rampa Deciende con Pendiente 2%
Pend. 27%
Pend. 2%
b.a.p.
ZONA DE DESCARGUE
TANQUE ALMACENAMIENTO AGUA 5000 LT
A A-301
B A-301
C A-301
C´ A-301
D A-301
D´ A-301
A´ A-301
B´ A-301
Pino
Hidranrte
Anden en piedra

0 10 m

Muros
Puertas/ventanas
Equipos/mobiliario
Cotas (m)
Ejes
Aa Niveles
Aa Espacios

FACHADA NORTE

Plancha A-004 · Escala original 1:50 · En esta hoja A3 ≈ 1:104

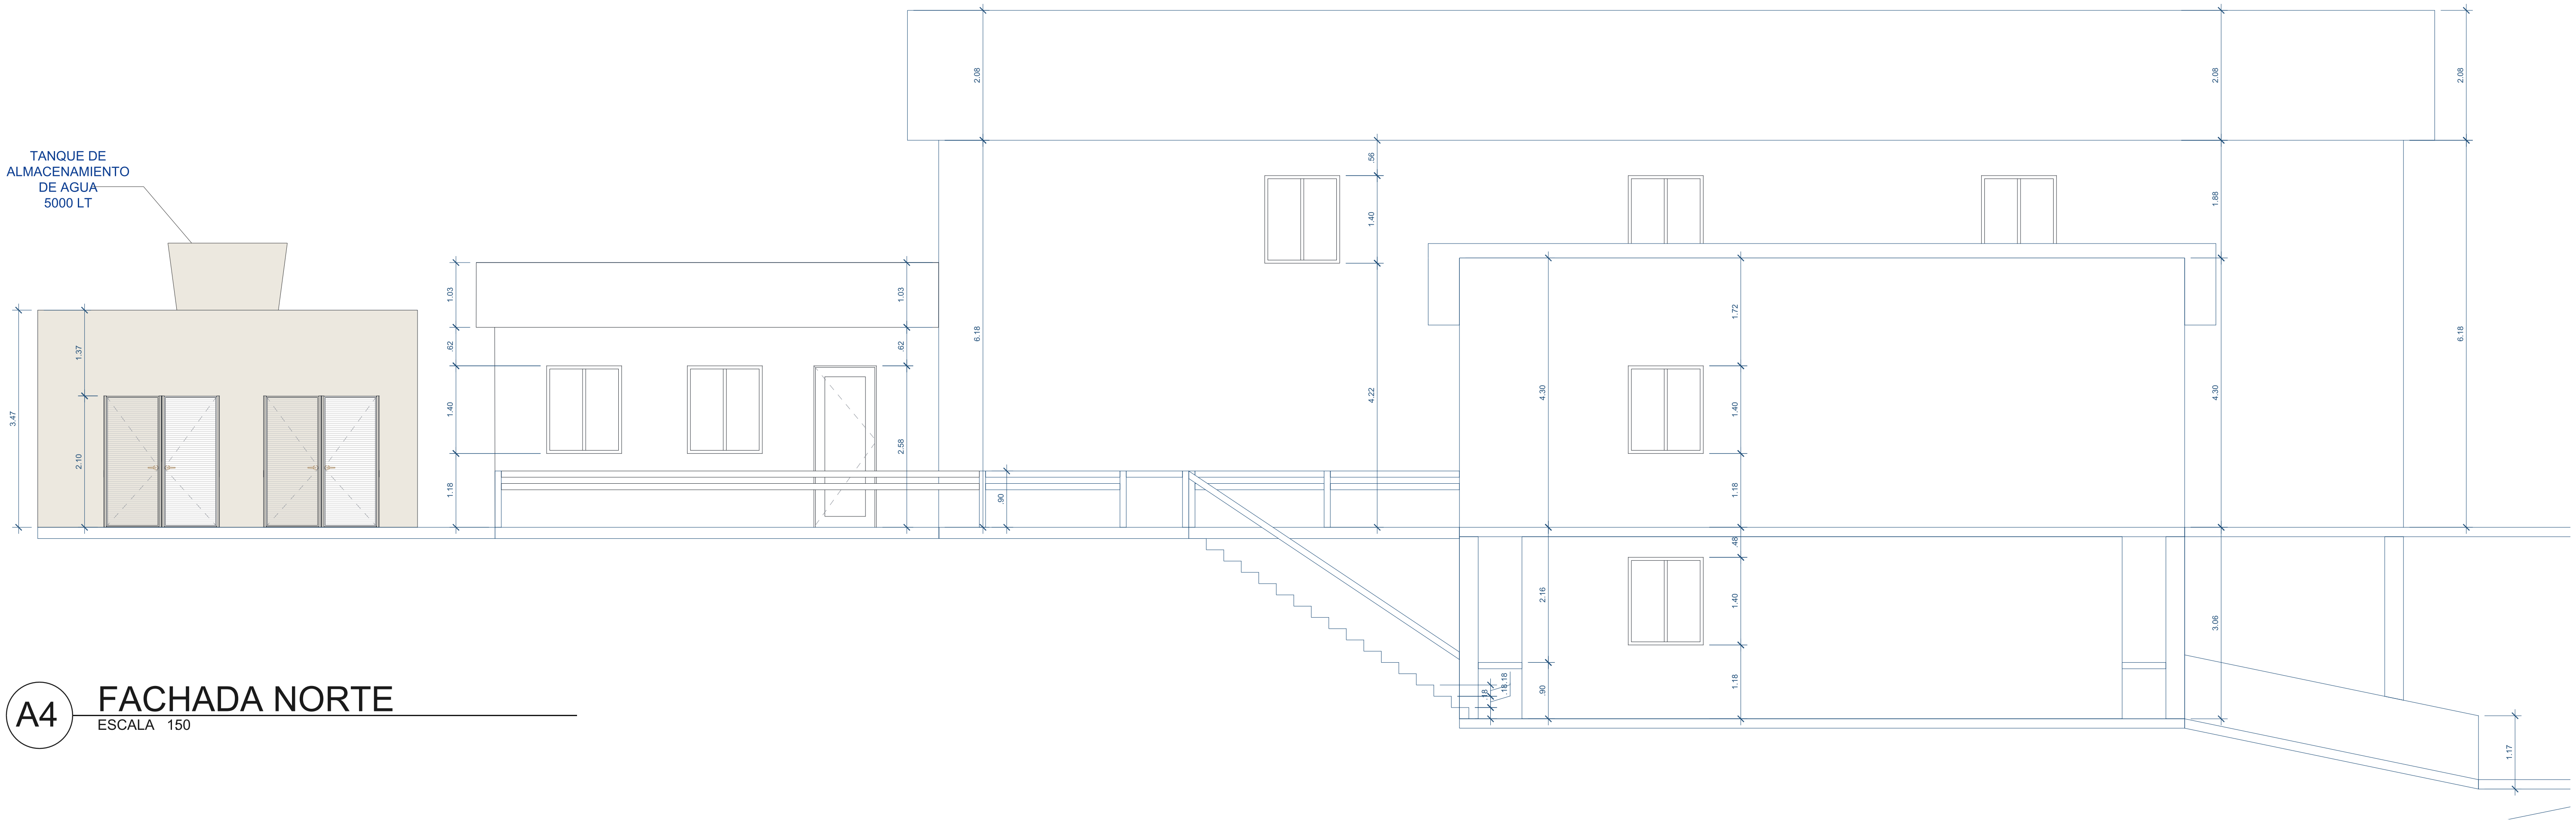
TANQUE DE ALMACENAMIENTO DE AGUA 5000 LT
3.47
1.37
2.10
1.03
.62
1.40
1.18
2.58
2.08
6.18
.90
.56
4.22
4.30
1.72
.48
2.16
3.06
1.88
1.17

A4 FACHADA NORTE

ESCALA 150

0 5 m

▬ Muros

— Puertas/ventanas

— Equipos/mobiliario

— Cotas (m)

-·-·- Ejes

Aa Niveles

Aa Espacios

ALZADO FACHADA OESTE

Plancha A-004 · Escala original 1:50 · En esta hoja A3 ≈ 1:60

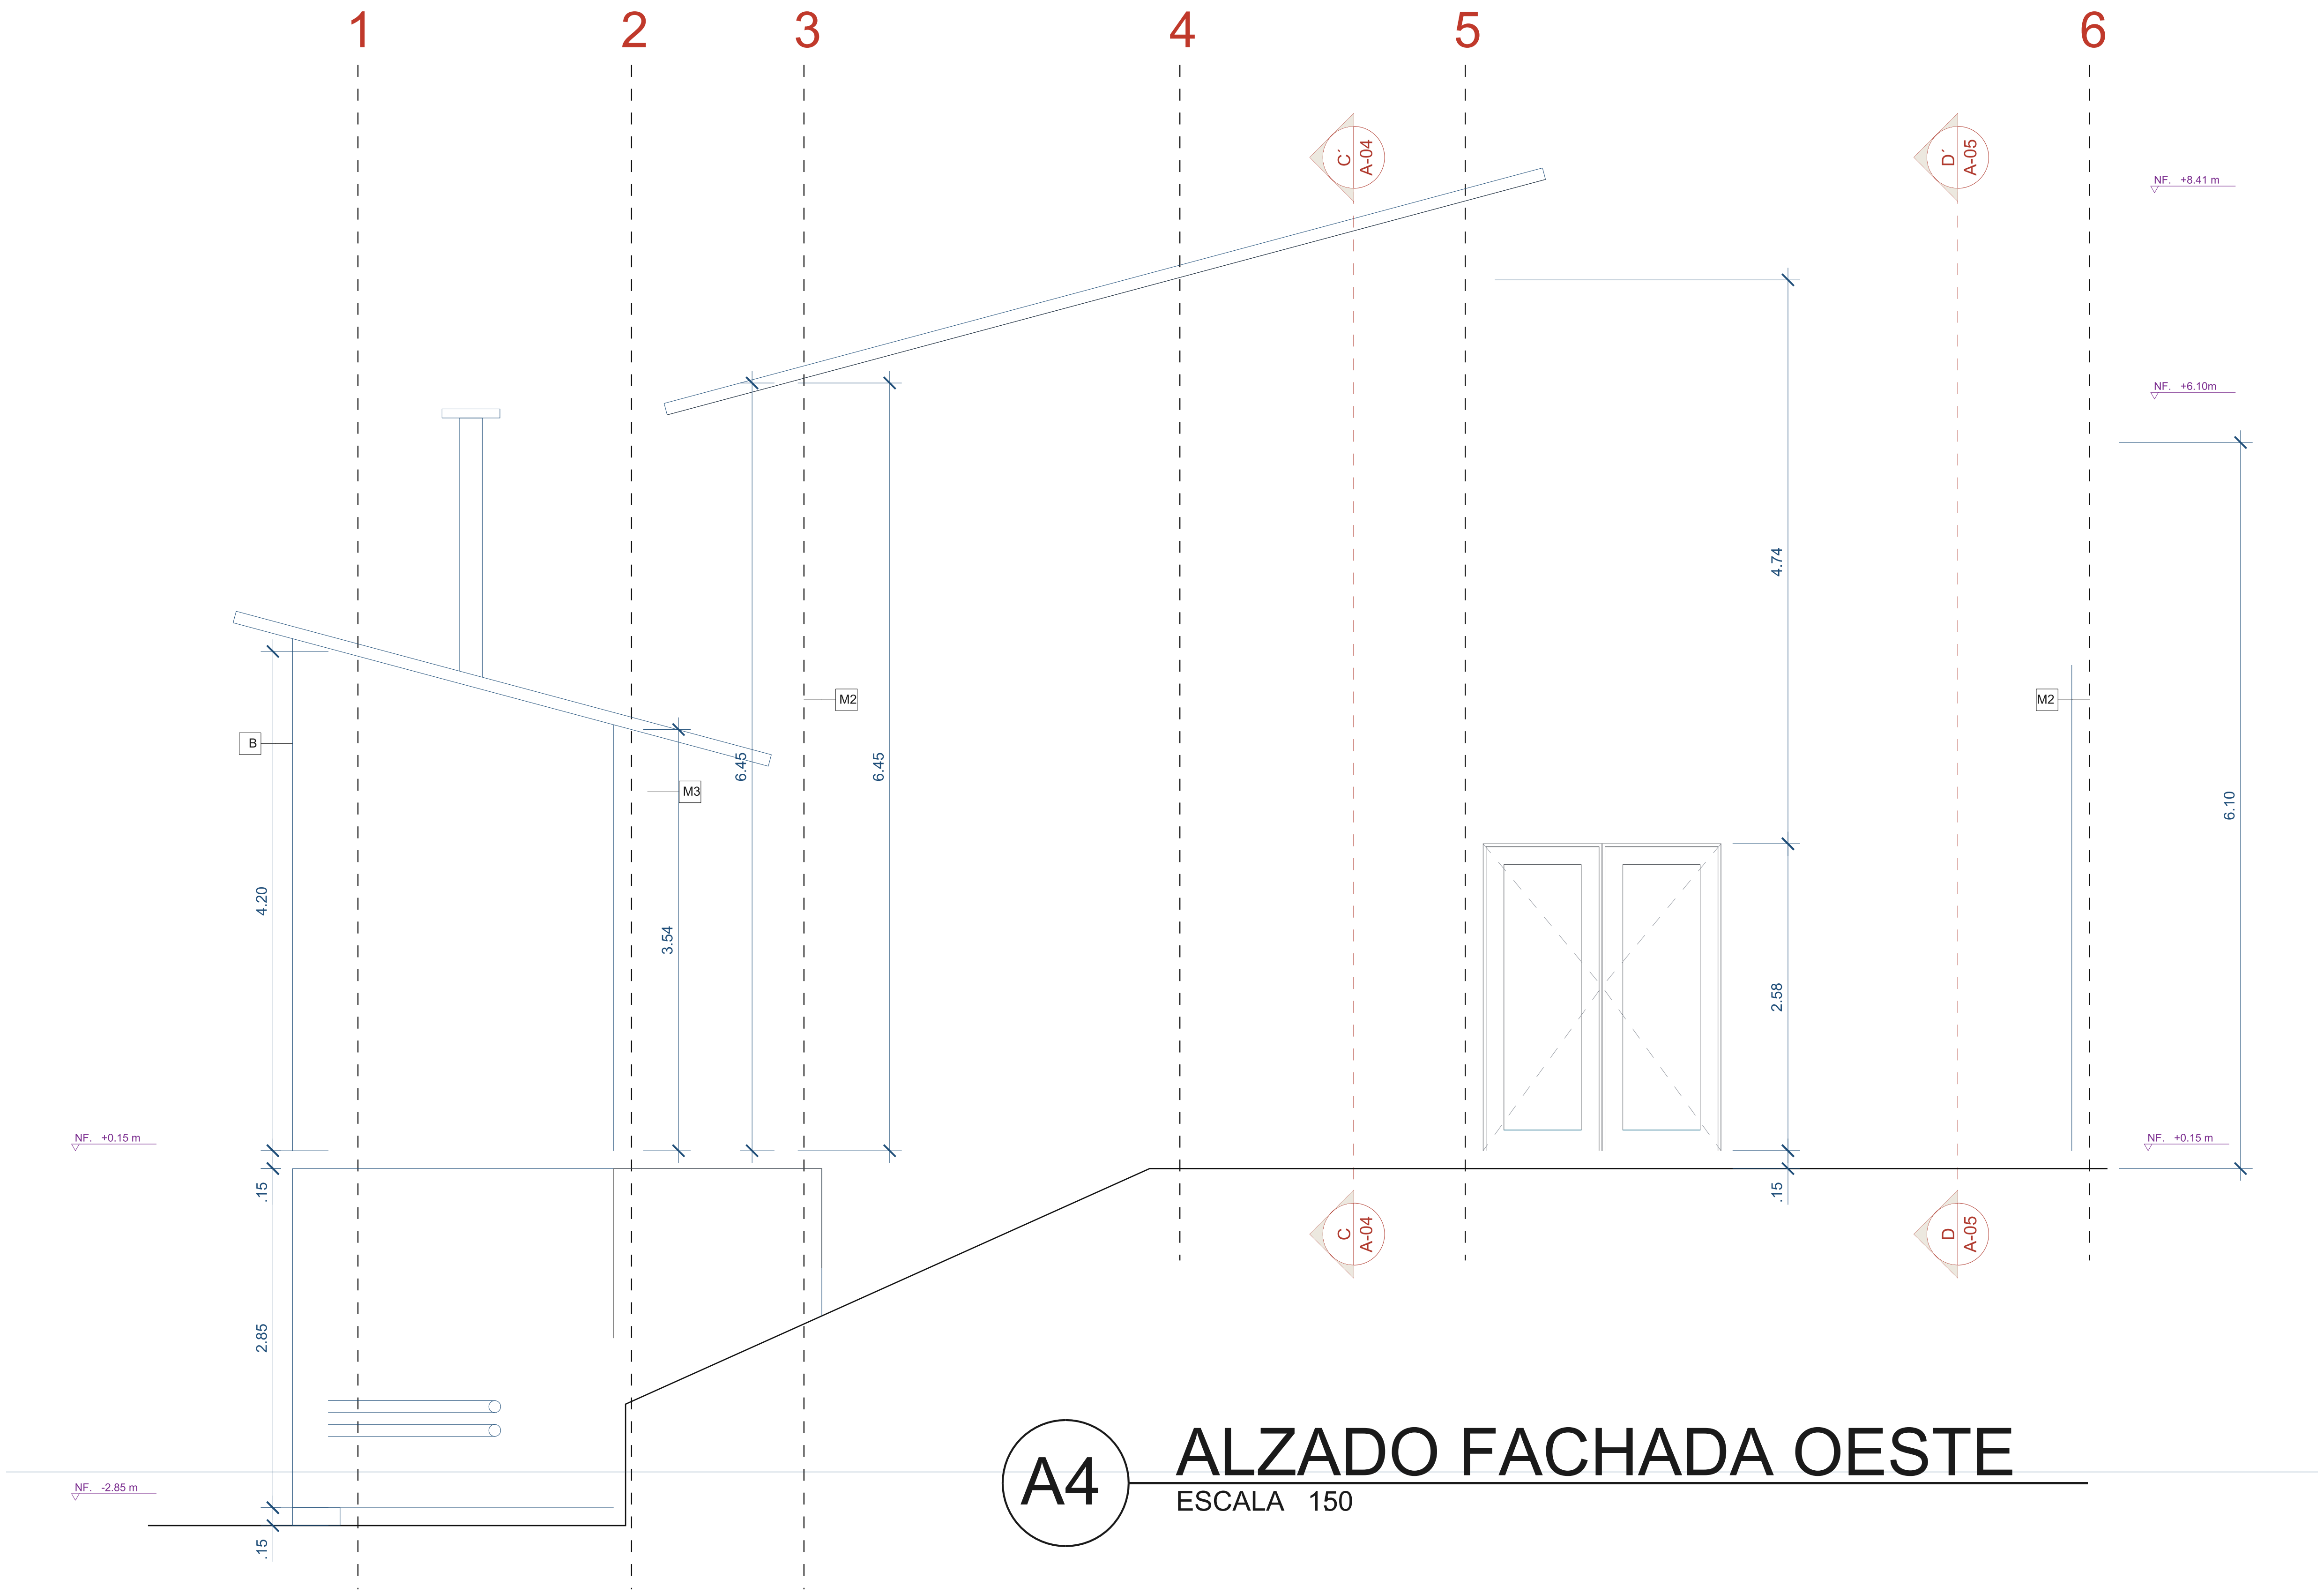
1
2
3
4
5
6
C'
A-04
D'
A-05
C
A-04
D
A-05
NF. +8.41 m
NF. +6.10m
NF. +0.15 m
NF. +0.15 m
NF. -2.85 m
B
M2
M2
M3
4.20
.15
2.85
.15
3.54
6.45
6.45
4.74
2.58
.15
6.10

A4 ALZADO FACHADA OESTE

ESCALA 150

0 5 m

- Muros
- Puertas/ventanas
- Equipos/mobiliario
- Cotas (m)
- Ejes
- **Aa** Niveles
- **Aa** Espacios

ALZADO FACHADA ESTE

Plancha A-004 · Escala original 1:50 · En esta hoja A3 ≈ 1:58

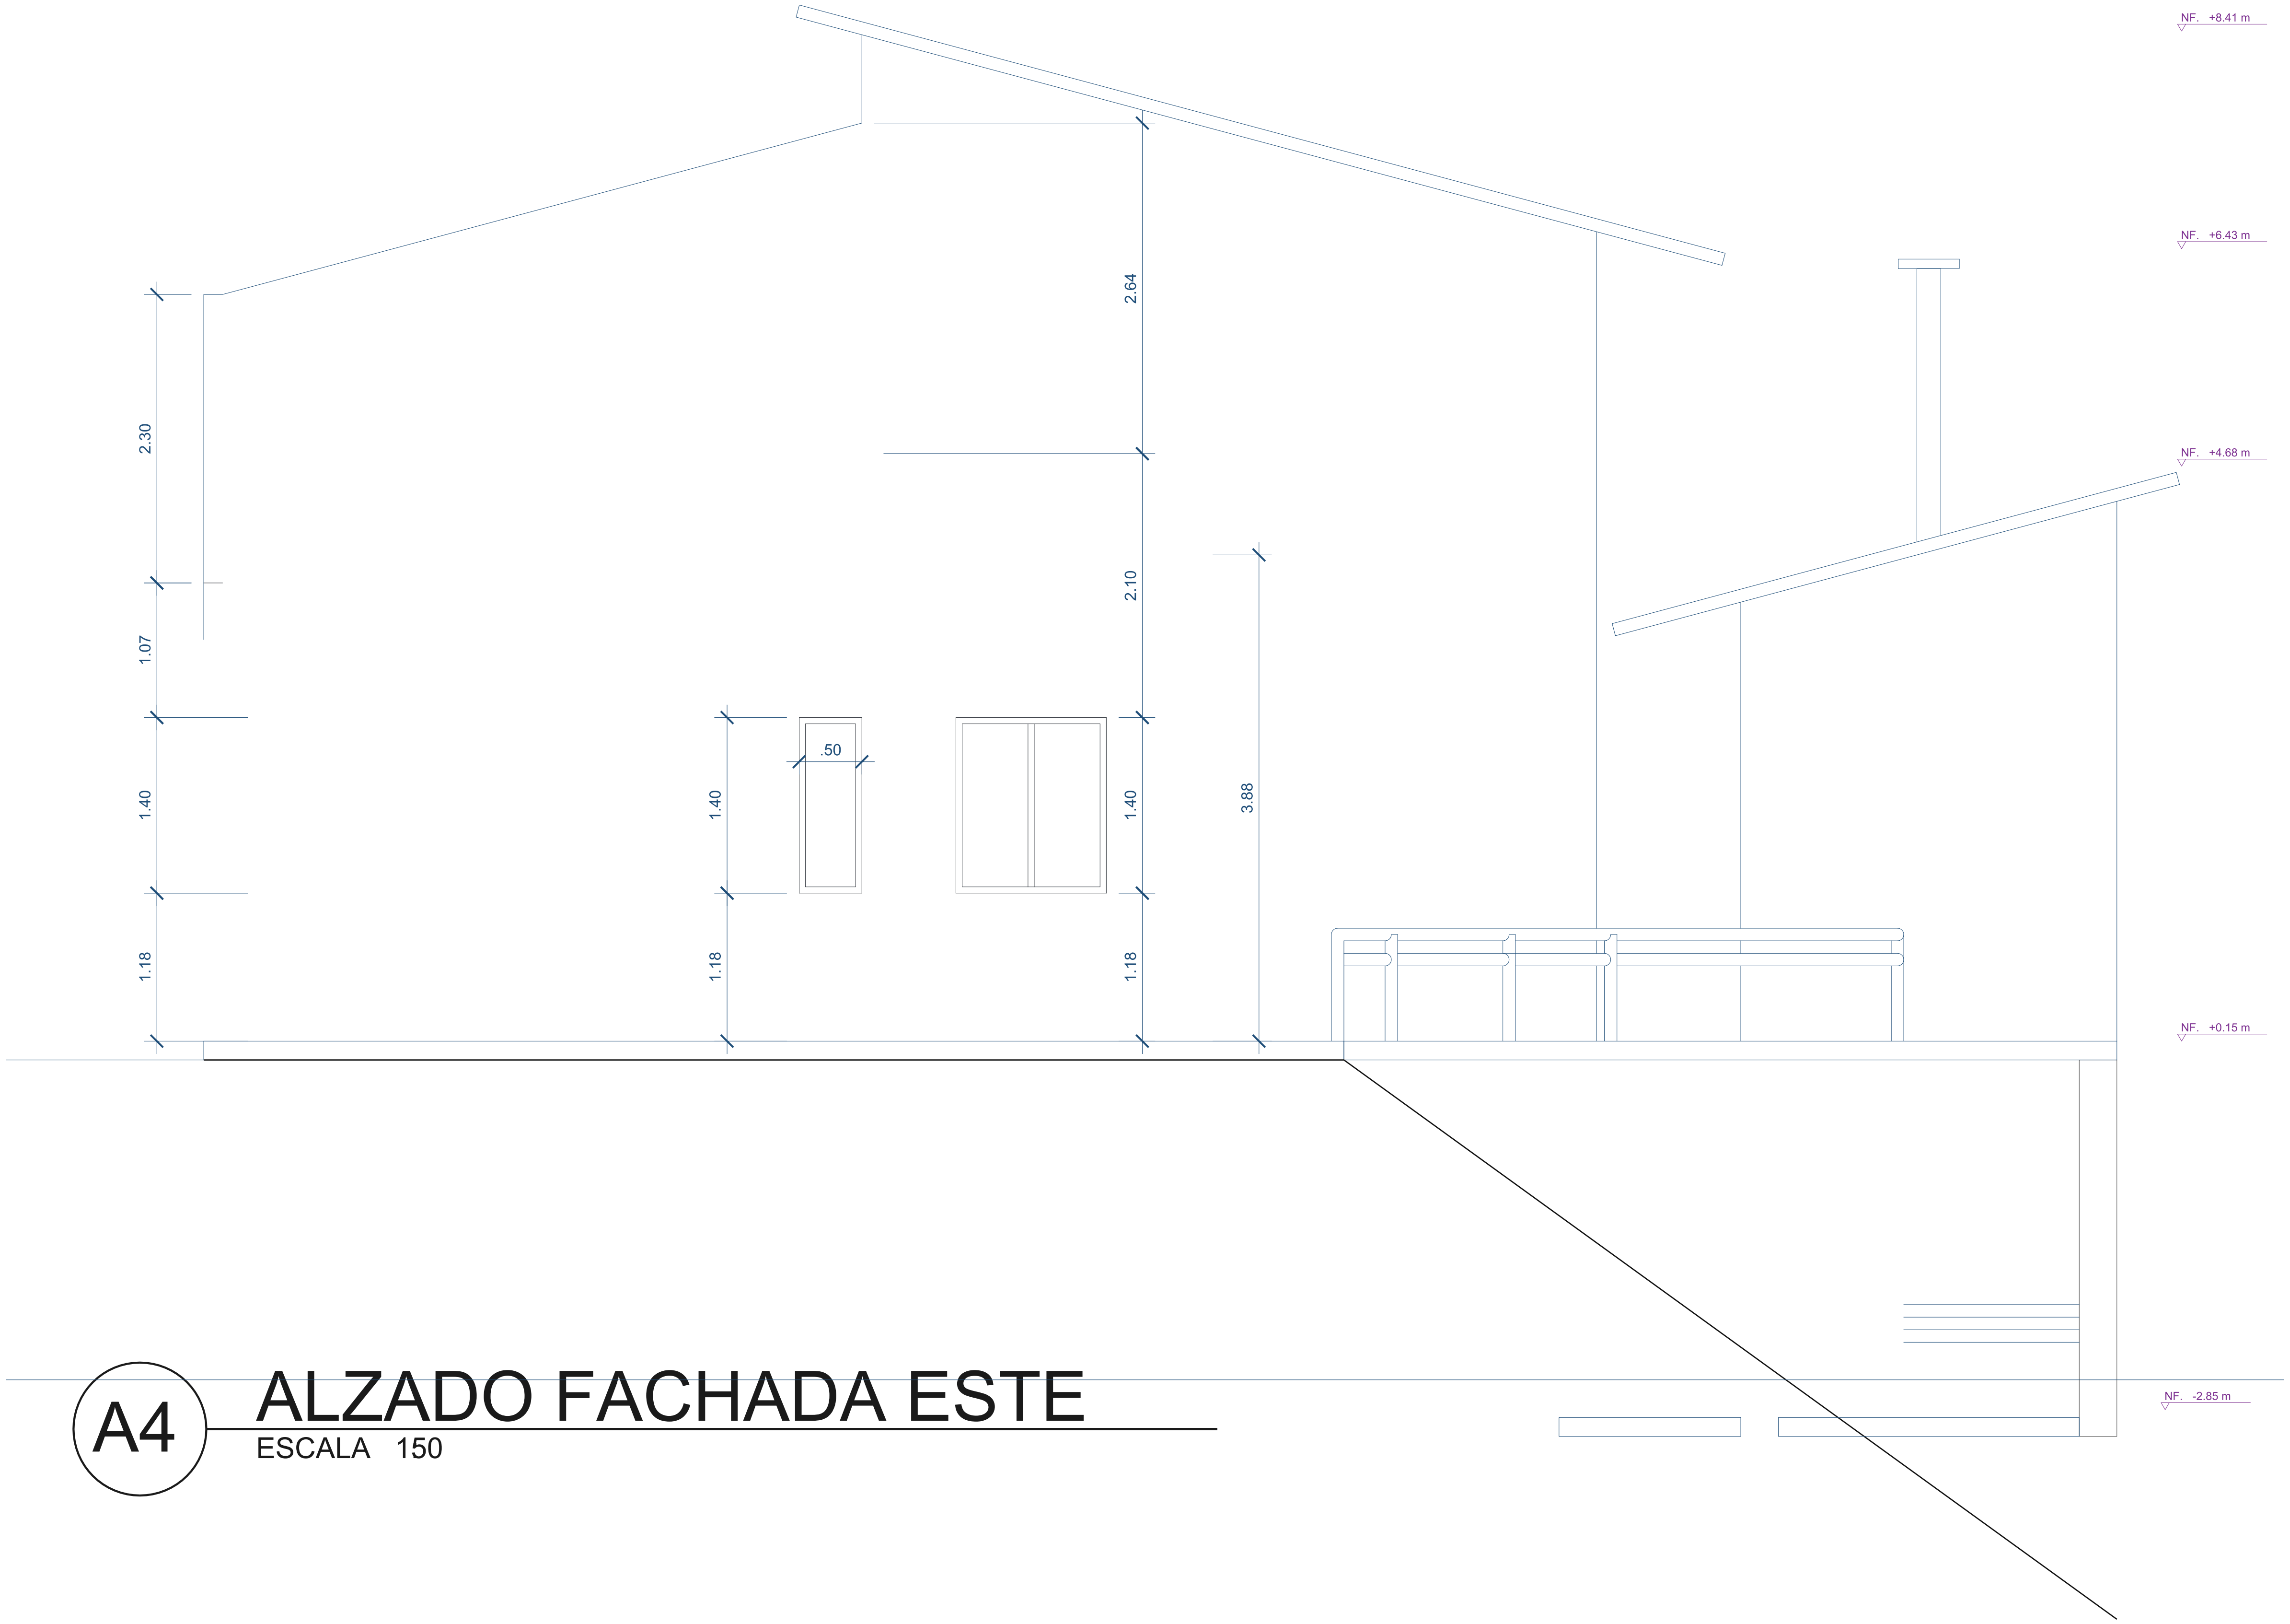
NF. +8.41 m
NF. +6.43 m
NF. +4.68 m
NF. +0.15 m
NF. -2.85 m
2.30
1.07
1.40
1.18
1.40
.50
1.18
2.64
2.10
1.40
1.18
3.88

A4 **ALZADO FACHADA ESTE**

ESCALA 150

0 5 m

━ Muros ― Puertas/ventanas ― Equipos/mobiliario ― Cotas (m) -·-· Ejes **Aa** Niveles **Aa** Espacios

CORTE A-A'

Plancha A-005 · Escala original 1:50 · En esta hoja A3 ≈ 1:62

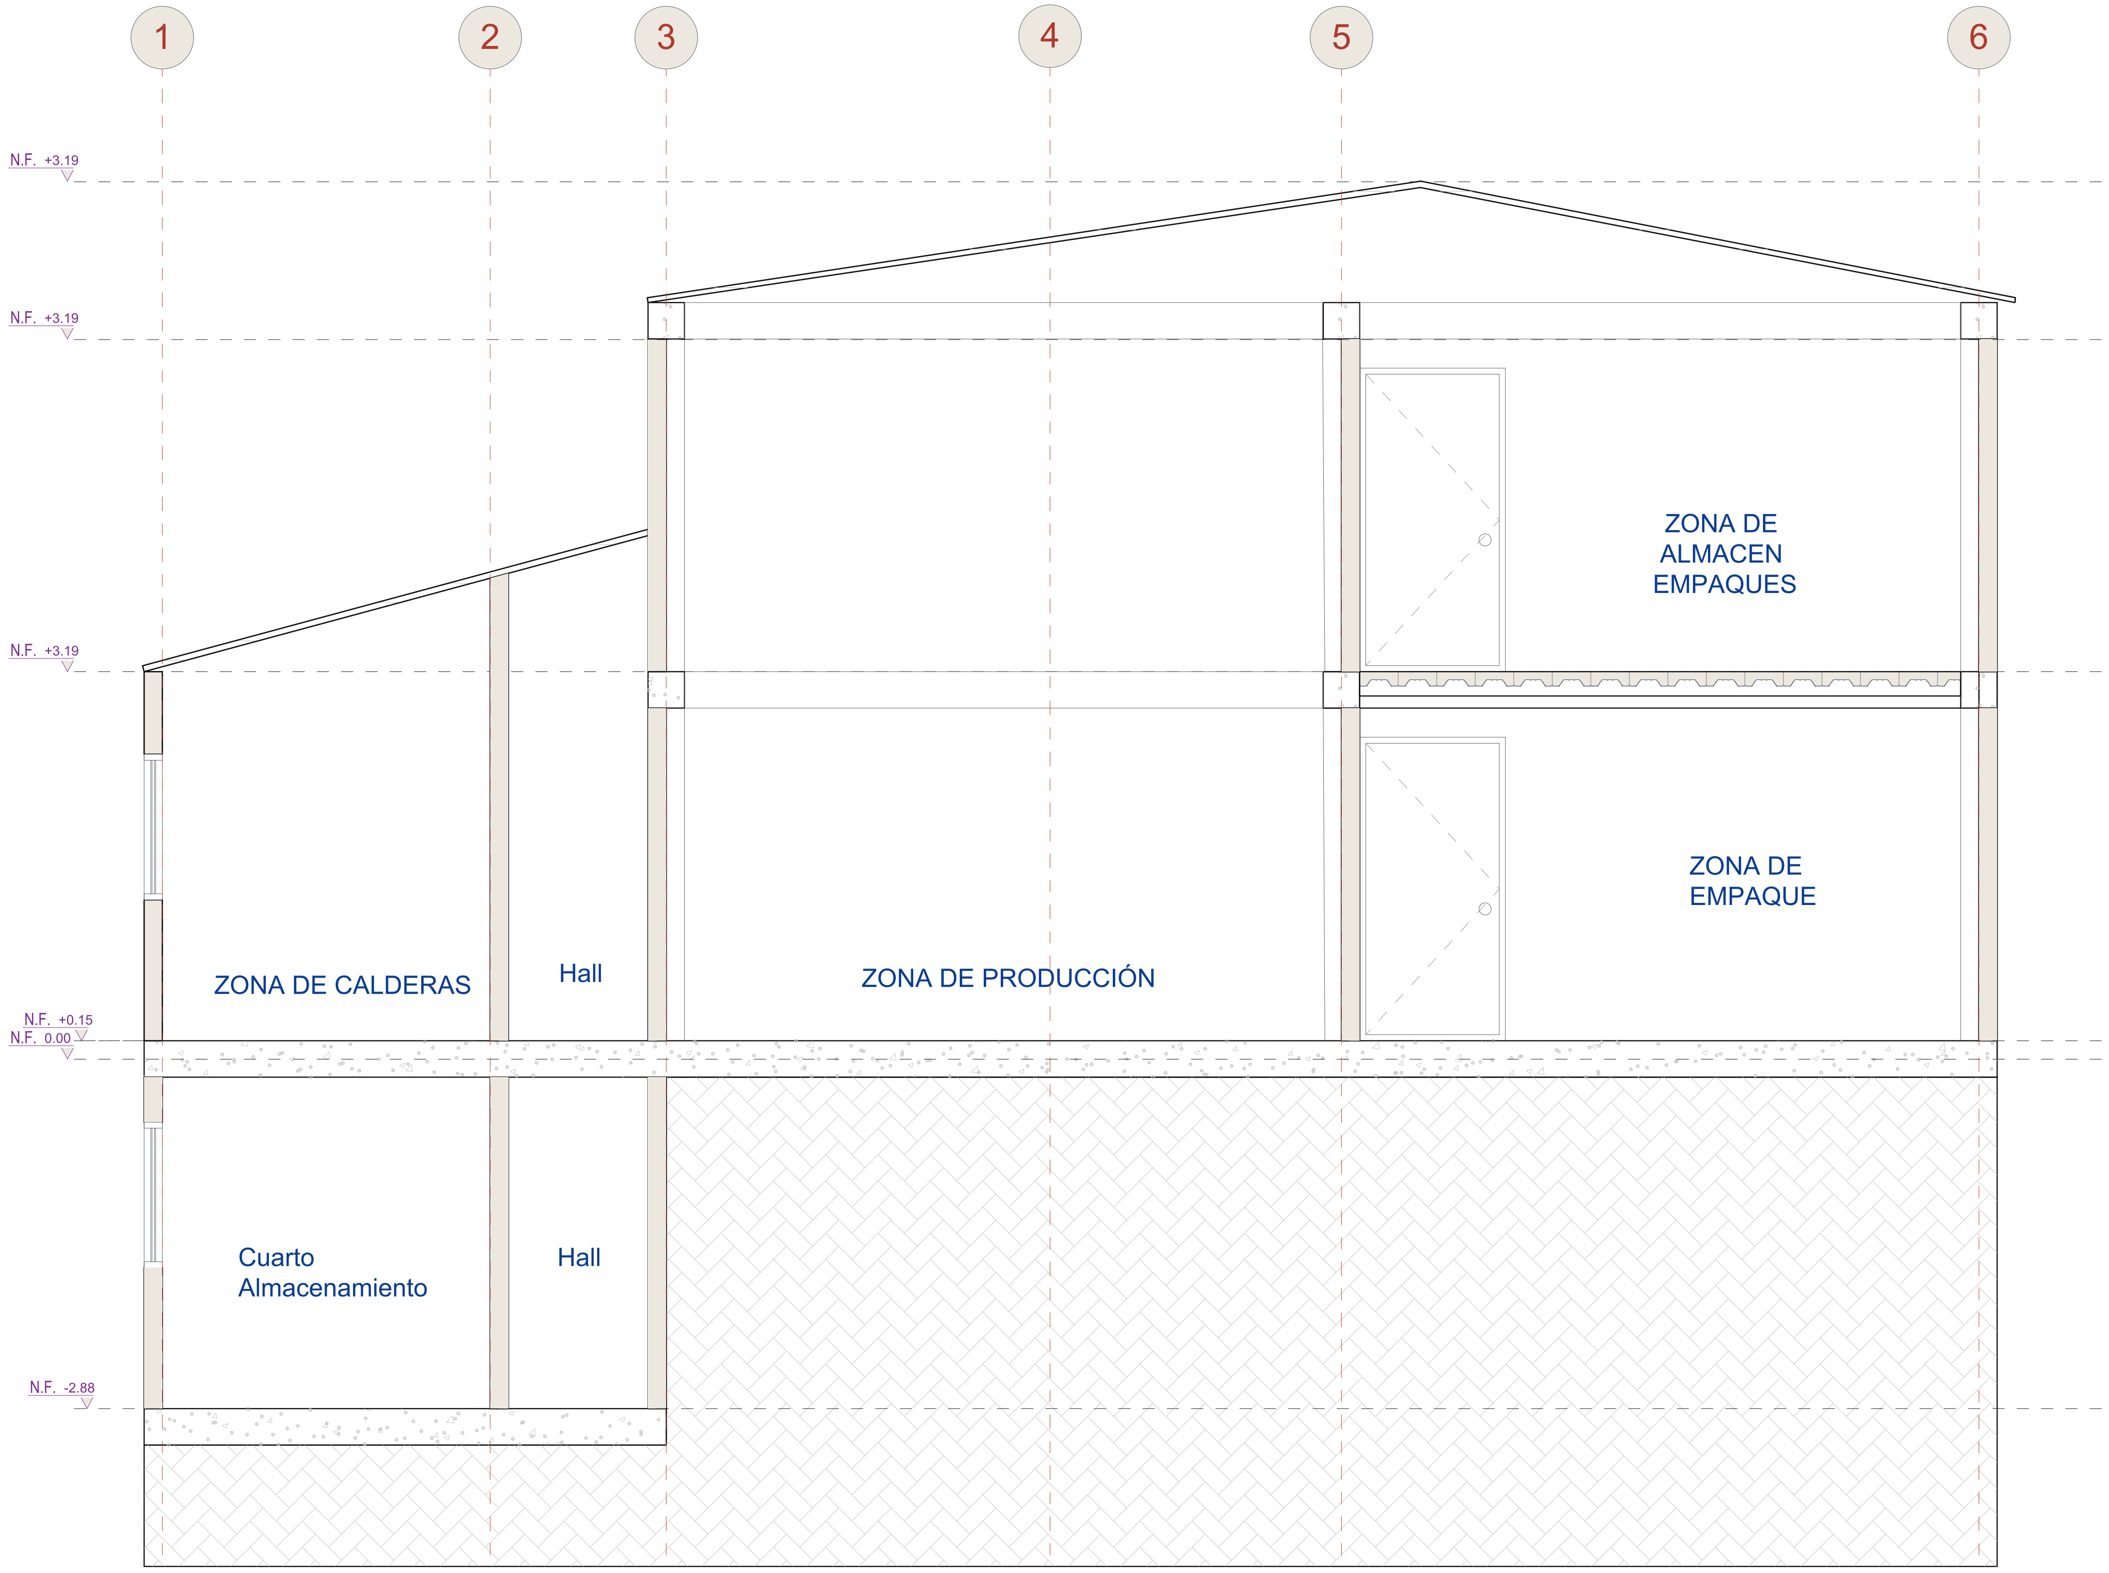
1
2
3
4
5
6
N.F. +3.19
N.F. +3.19
N.F. +3.19
N.F. +0.15
N.F. 0.00
N.F. -2.88
ZONA DE
ALMACEN
EMPAQUES
ZONA DE
EMPAQUE
ZONA DE CALDERAS
Hall
ZONA DE PRODUCCIÓN
Cuarto
Almacenamiento
Hall

A1 CORTE A - A'

ESCALA 150

0 — 5 m

— Muros · — Puertas/ventanas · — Equipos/mobiliario · — Cotas (m) · -·-·- Ejes · **Aa** Niveles · **Aa** Espacios

CORTE B-B'

Plancha A-005 · Escala original 1:31 · En esta hoja A3 ≈ 1:36

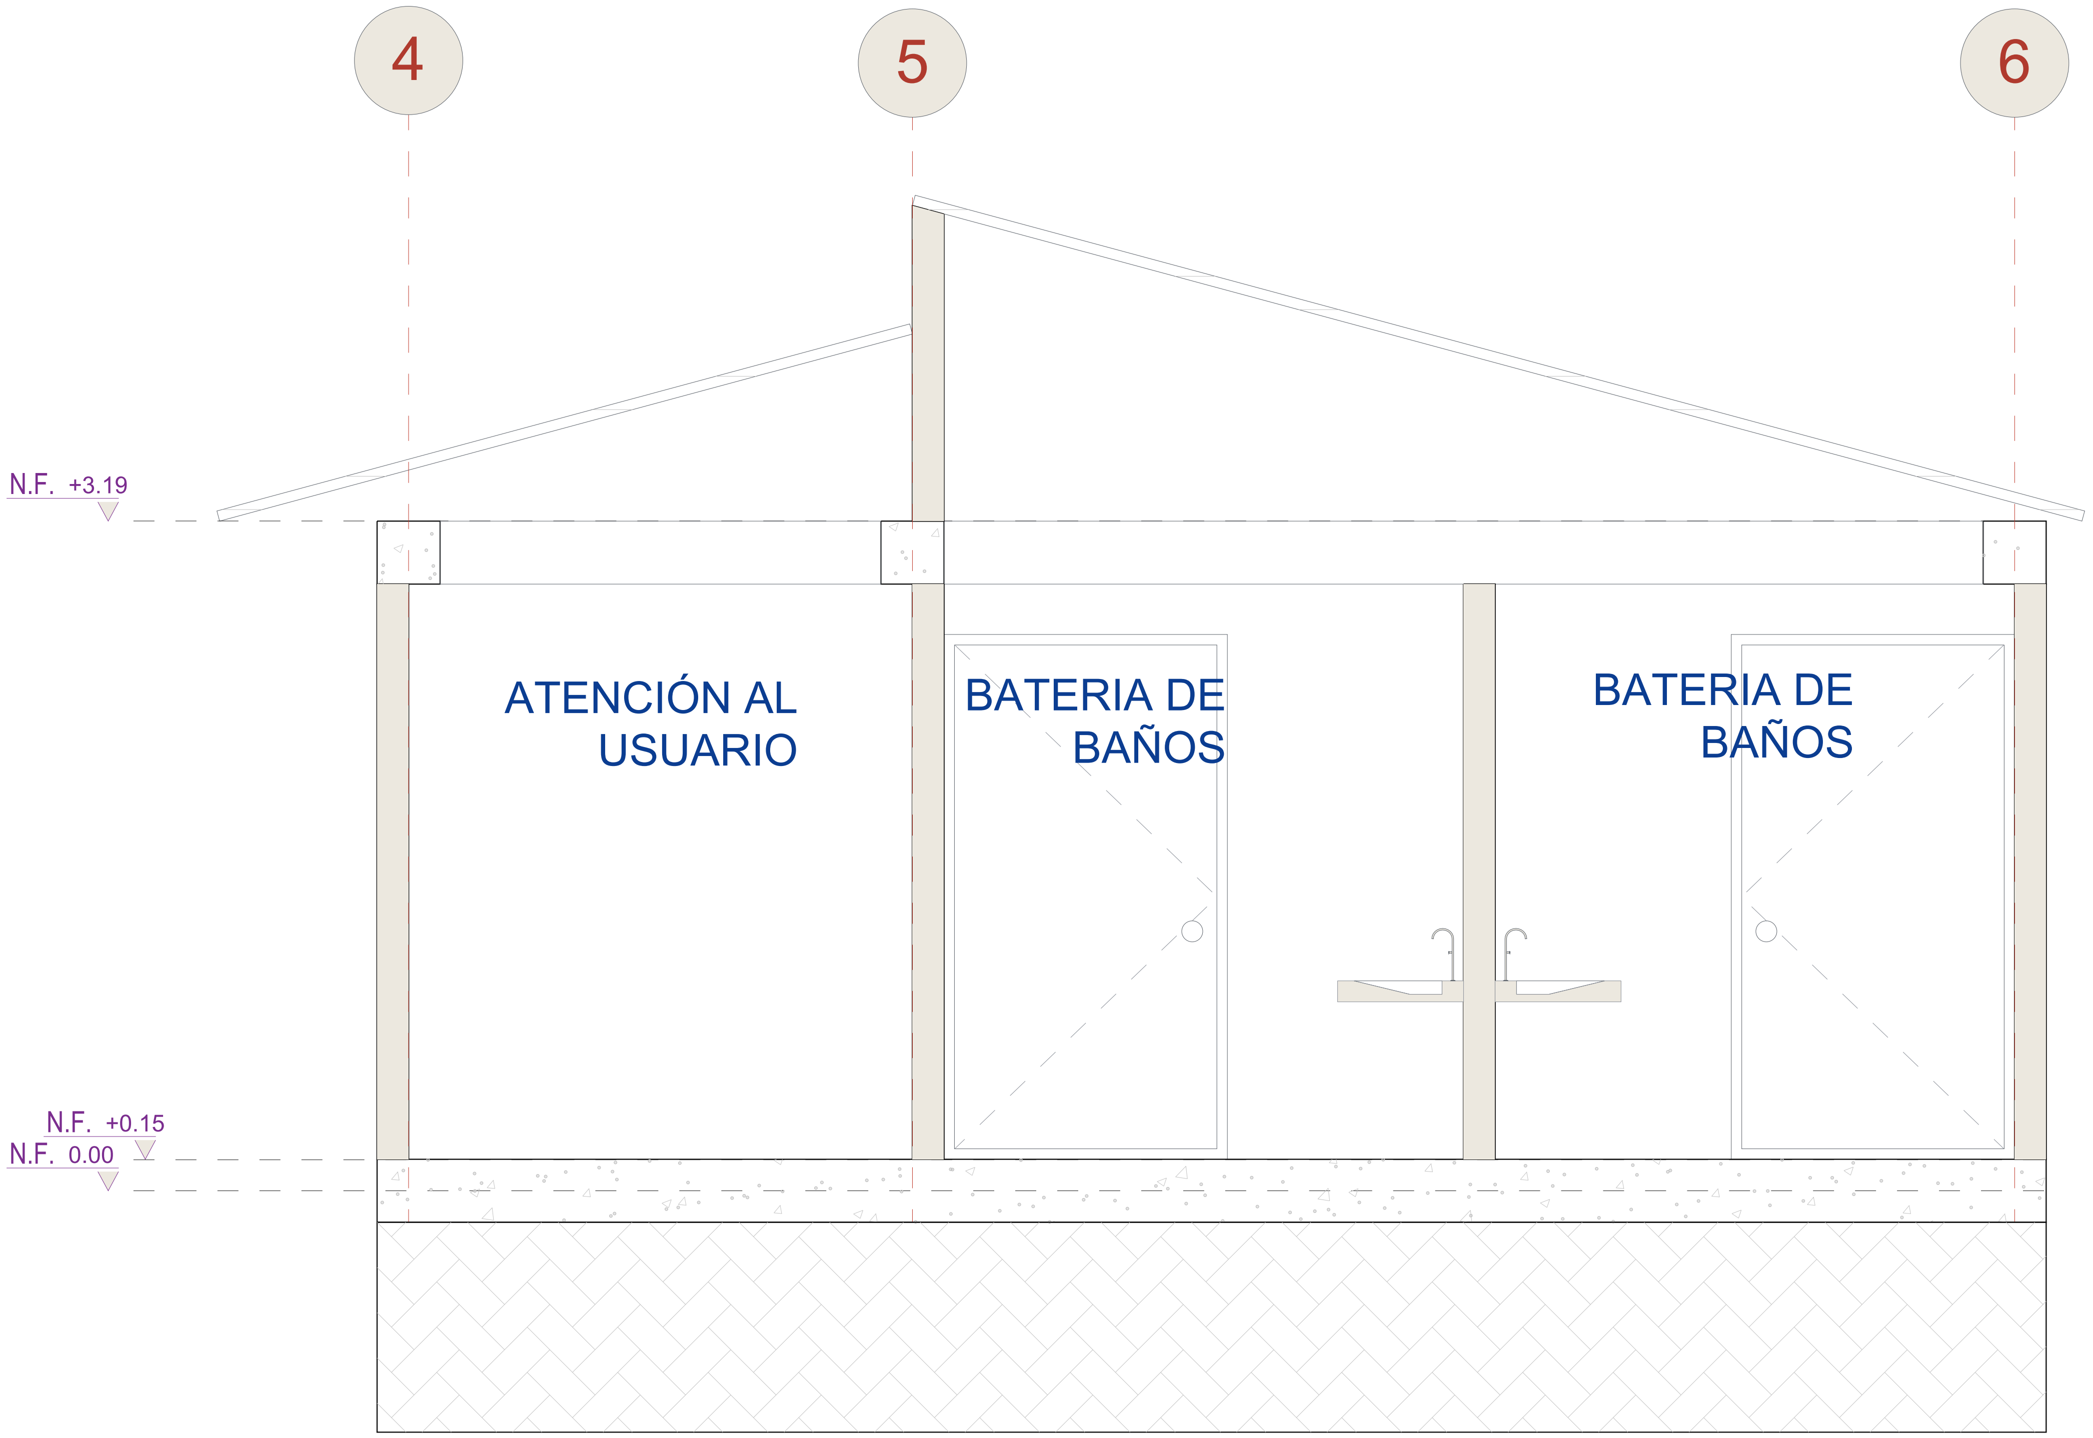
4
5
6
N.F. +3.19
N.F. +0.15
N.F. 0.00
ATENCIÓN AL USUARIO
BATERIA DE BAÑOS
BATERIA DE BAÑOS

A1

CORTE B - B'

ESCALA 150

0 2 m

━ Muros · ━ Puertas/ventanas · ━ Equipos/mobiliario · ━ Cotas (m) · -·-·- Ejes · Aa Niveles · Aa Espacios

CORTE C-C'

Plancha A-005 · Escala original 1:75 · En esta hoja A3 ≈ 1:116

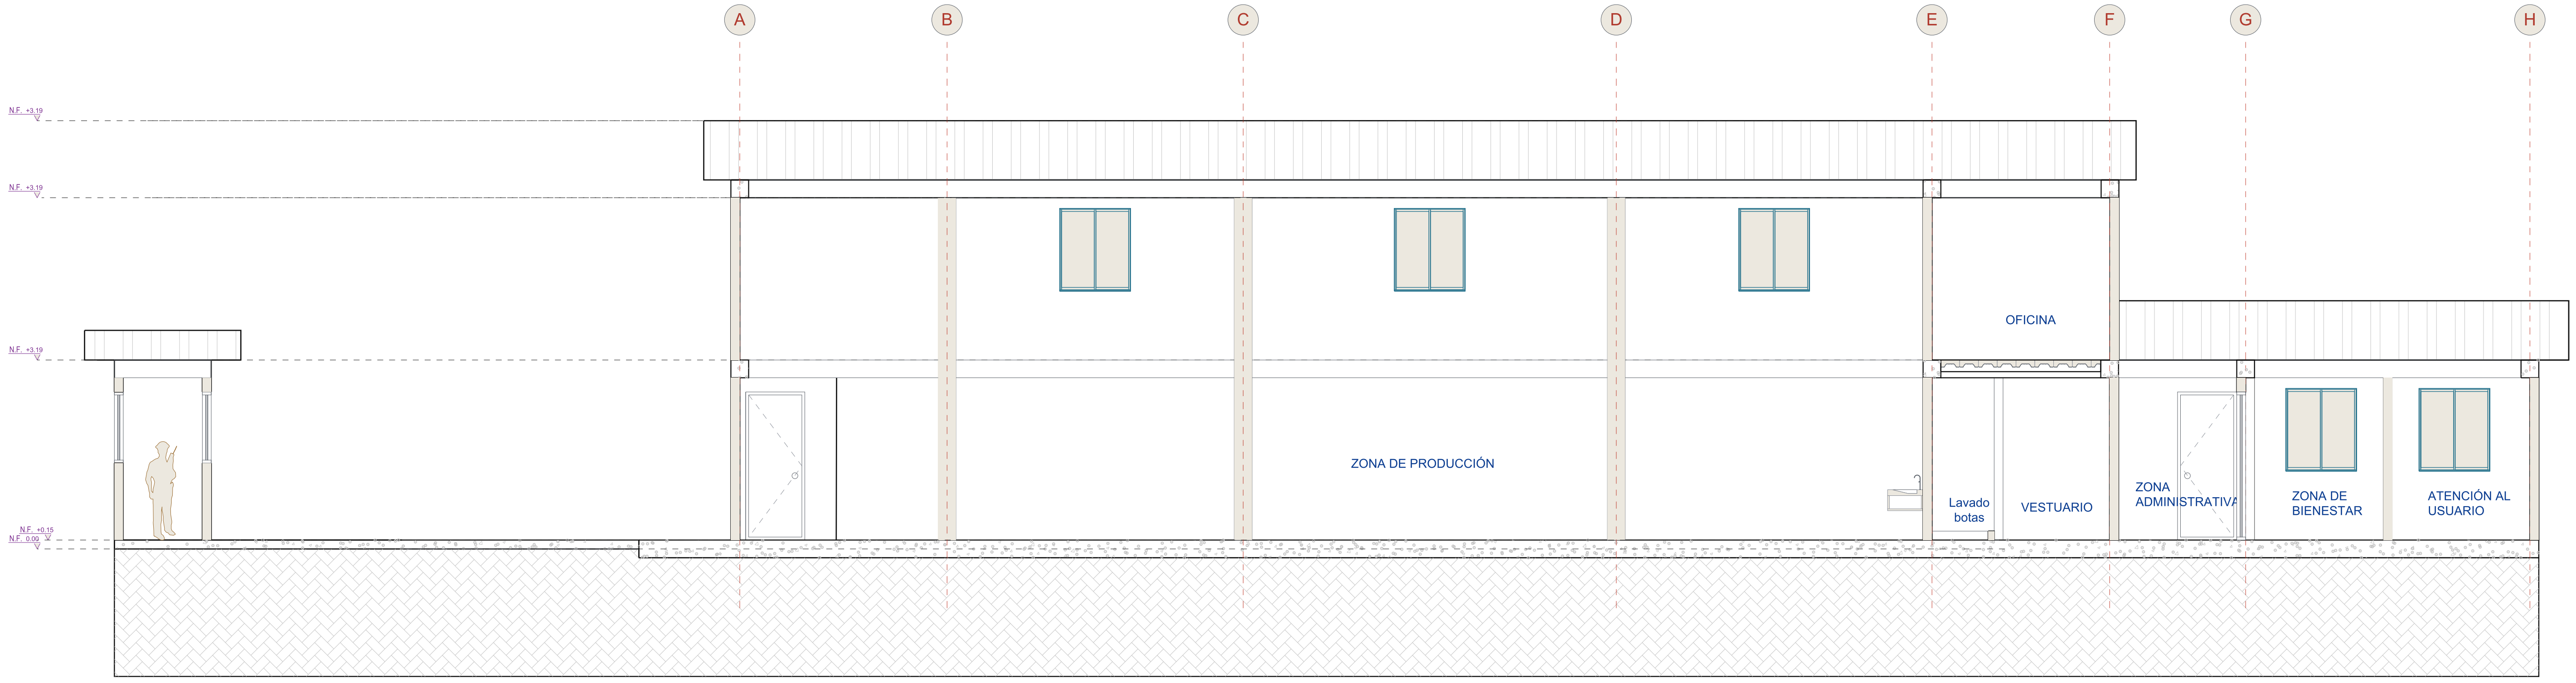
A
B
C
D
E
F
G
H
N.F. +3.19
N.F. +3.19
N.F. +3.19
N.F. +0.15
N.F. 0.00
OFICINA
ZONA DE PRODUCCIÓN
Lavado botas
VESTUARIO
ZONA ADMINISTRATIVA
ZONA DE BIENESTAR
ATENCIÓN AL USUARIO

A1 CORTE C - C'
ESCALA 175

0 10 m

▬ Muros
— Puertas/ventanas
— Equipos/mobiliario
— Cotas (m)
-·-·- Ejes
Aa Niveles
Aa Espacios

CORTE D-D'

Plancha A-005 · Escala original 1:75 · En esta hoja A3 ≈ 1:134

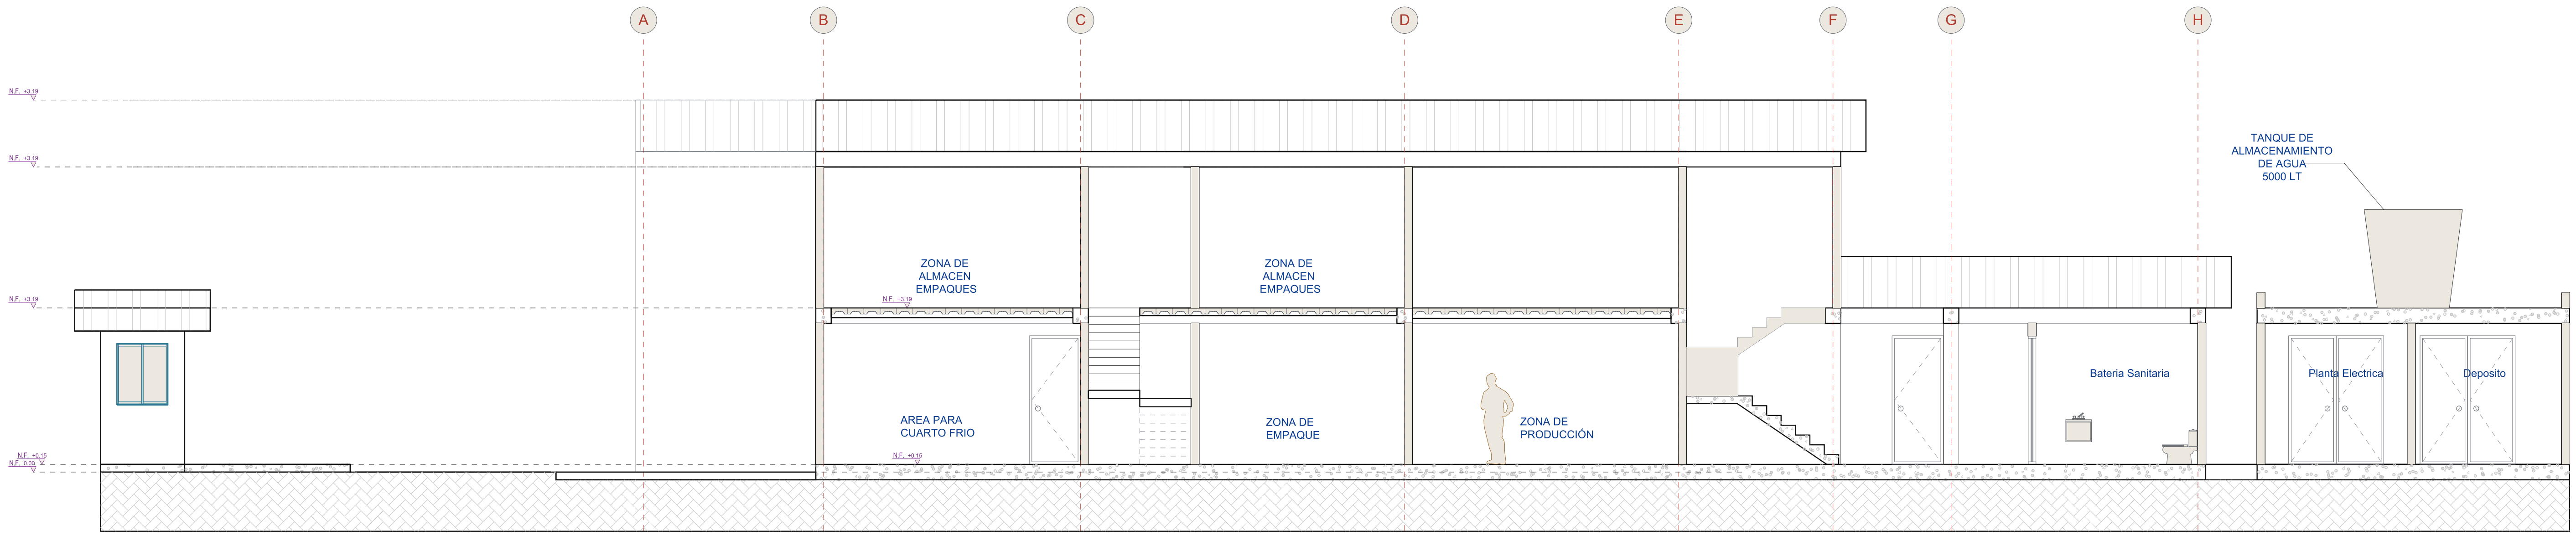
A
B
C
D
E
F
G
H
N.F. +3.19
N.F. +3.19
N.F. +3.19
N.F. +0.15
N.F. 0.00
ZONA DE ALMACEN EMPAQUES
N.F. +3.19
ZONA DE ALMACEN EMPAQUES
TANQUE DE ALMACENAMIENTO DE AGUA 5000 LT
Bateria Sanitaria
Planta Electrica
Deposito
AREA PARA CUARTO FRIO
N.F. +0.15
ZONA DE EMPAQUE
ZONA DE PRODUCCIÓN

A1 CORTE D - D'
ESCALA 1:75

0 10 m

▬ Muros — Puertas/ventanas — Equipos/mobiliario — Cotas (m) -·-·- Ejes **Aa** Niveles **Aa** Espacios

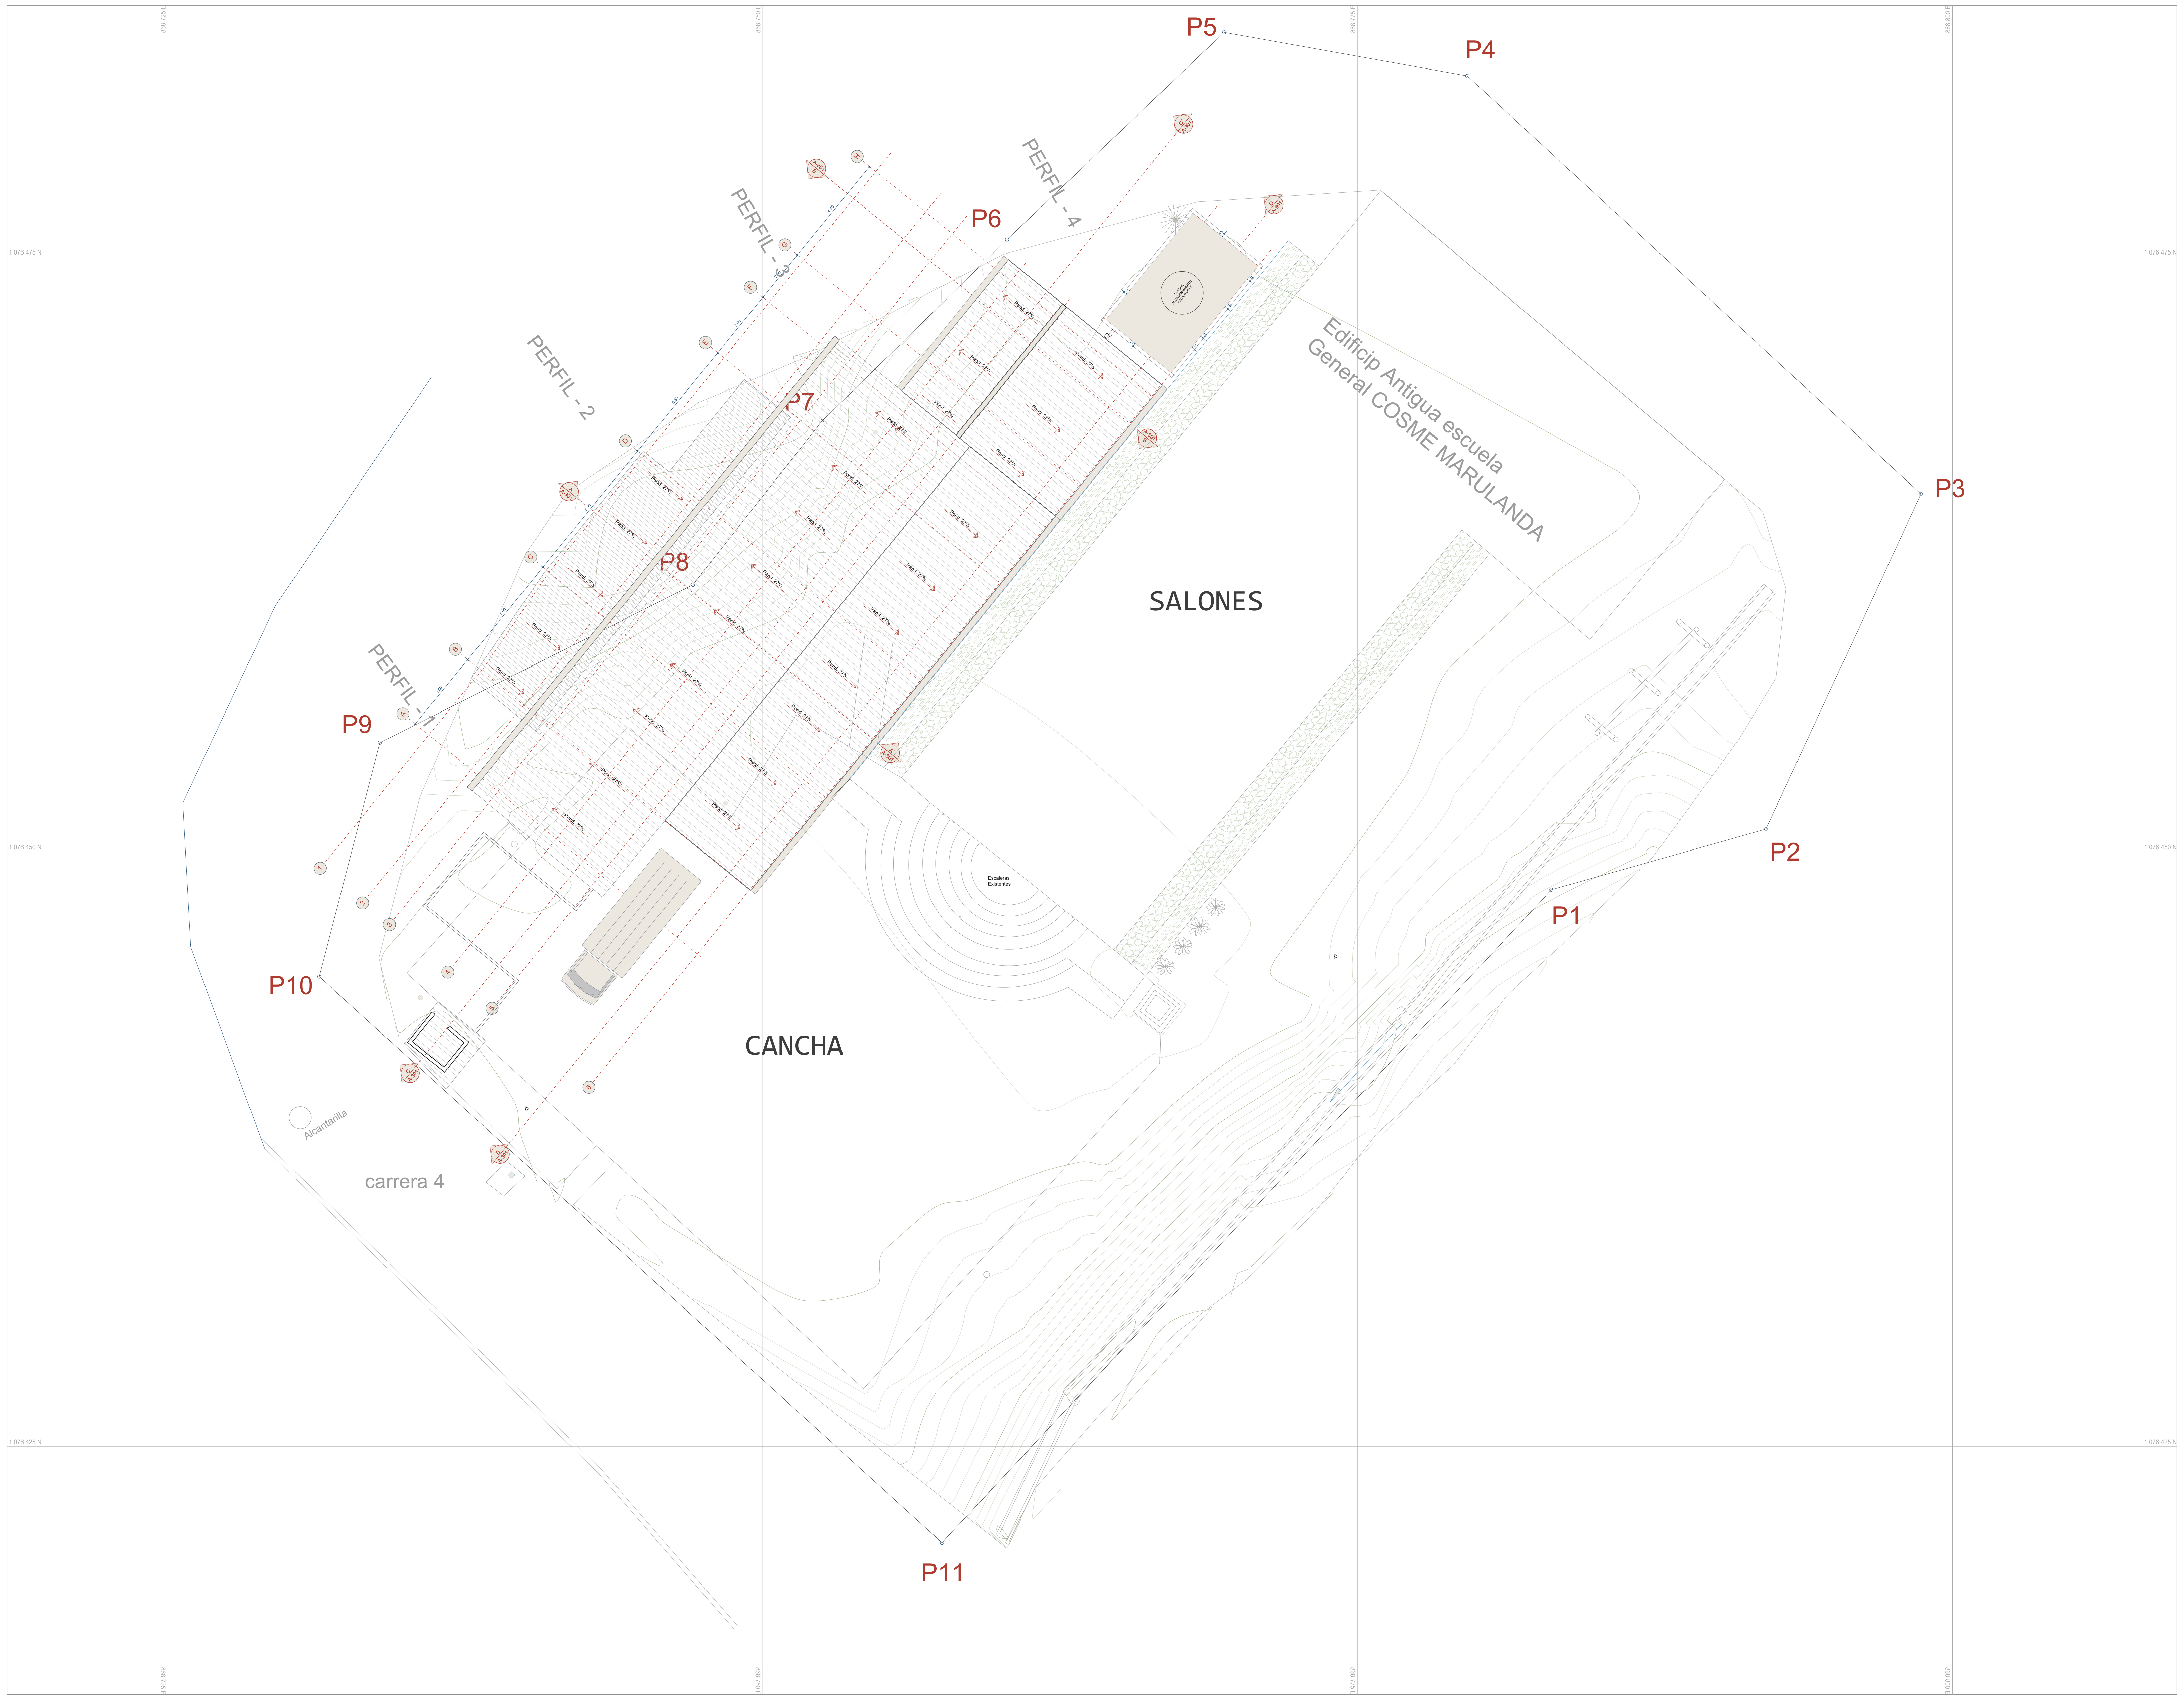

IMPLANTACIÓN

ESCALA GRAFICA

NOTAS GENERALES CIVILES

1. Prever dilataciones en cielo raso para columnas de 2 cm.
2. Cerramiento en muro con altura de 3.15m, referirse a planos de detalle.

NOTAS GENERALES DE PLANCHA

1. El norte hace referencia a la forma en que se debe orientar el proyecto al momento de ser implantado

NOTAS DE REFERENCIA

DIVISIONES Y MUROS

B	Muro en bloque N° 5	B
D1	Muro en fibrocemento de una cara	D1
D2	Muro en fibrocemento de 12 cm	D2
DM	División y puerta en acero inoxidable calibre 18, separadas del piso 0,20 m	DM

ACABADOS DE MURO

1	Enchape ceramico blanco formato 0.25 x 0.40	M1
2	Estuco plastico y pintura vinilo 3 manos blanco.	M2
3	Pintura acrilica para exteriores color blanco.	M3
4	Pintura epóxica blanca	M4

ACABADOS DE PISO

1	PISO CON RECUBRIMIENTO POLIMÉRO DE ALTA RESISTENCIA.	P1
2	MEDIACAÑA CON MORTERO EPOXICO DE ALTA RESISTENCIA.	P2
3	Guardaescoba media caña fundido en granito	P3
		P4
4	Piso en baldosa ceramica trafico pesado 33.8 X 33.8	P5
5	Loseta de cemento prepulida gris	P6
6	Bocapuerta en granito perlato	

ACABADO CIELO RASO — CI1

1	Lamina de1.20 x 0.60 m de fibra mineral, color blanco.	

APARATOS

1	Meson en concreto, acabado en granito pulido.	A1
2	Sanitario con fluxometro y asiento institucional o similar	A2
3	Lavamanos tipo marsella blanco o similar, con griferia galaxia 8 o similar.	A3
4	Ducharegistro tipo prisma o similar.	A4
5	Lavaplatos en acero inoxidable con poceta y escurridero.	A5
6	Protector para papel higuienico accesorios y acabados o similar	A6
7	Barra de seguridad para discapacitados en acero inoxidable de 36".	A7
8	Barra de seguridad para discapacitados en acero inoxidable de 24".	A8
9	Espejo con borde biselado de 0.70 x 1.30 / E: 0.04 m	A9
10	Dispensador de jabon para muro	A10
11	Canecas para basura en verde, rojo y gris	A11

A-001

PLANO No:

PLANCHA No: **01**

DE: **0**

PROYECTO:

CONSTRUCCIÓN DE LA
INFRAESTRUCTURA DE LA PLANTA DE
TRANSFORMACIÓN DE LÁCTEOS
MUNICIPIO MARULANDA

MUNICIPIO DE MARULANDA - CALDAS
DIRECCIO: CARRERA 6 # 5 - 02

SUPERVISOR:

ING, MAYRA ALEJANDRA RAMIREZ RAMIREZ
SECRETARIA DE PLANEACIÓN

PROFESIONAL RESPONSABLE:

ARQ. DANIEL GONZALEZ AGUIRRE
M.P. A451492024-1000047231

DISEÑADOR DE ELEMENTOS NO ESTRUCTURALES

ING. CRISTIAN FERNEY HERRERA H
MAT. P. 17202-359548CLD

GRADO DE DESEMPEÑO DE ELEMENTOS NO ESTRUCTURALES (BAJO), GRUPO DE USO FABRIL E INDUSTRIAL (F), SUBGRUPO DE OCUPACION FABRIL E INDUSTRIAL DE RIESGO BAJO (F-2).

PROYECTO:

OBJETO: "CONSTRUCCIÓN DE LA
INFRAESTRUCTURA DE LA PLANTA DE
TRANSFORMACIÓN DE LÁCTEOS
MUNICIPIO MARULANDA**"**

OBRA NUEVA DE EDIFICACIÓN CON USO FABRIL E INDUSTRIAL 2 (F-2)

CONTENIDO

LOCALIZACIÓN

CONVENCIONES

P. PISOS
M. ACABADOS MUROS
T. ACABDO CIELO RASO
N. NIVEL FINO
G. GUARDAESCOBA
H. ALTURA LIBRE

MATERIALES

G. GRANITO
MR. MARMOL
V. VINILO
L. LADRILLO TOLETE
BL. BLOQUE N°5
C. CONCRETO ABUJARDADO
C. CONCRETO ESMALTADO

LOCALIZACIÓN:

NOTA: ESCALA **GRAFICA**

FECHA **2O26**

Todas las Medidas deberán ser Rectificadas en Obra,
Cuenta y Riesgo de Cada uno de los Contratistas.

PLANO No: **A-001**

PLANCHA No: **01**

DE: **0**

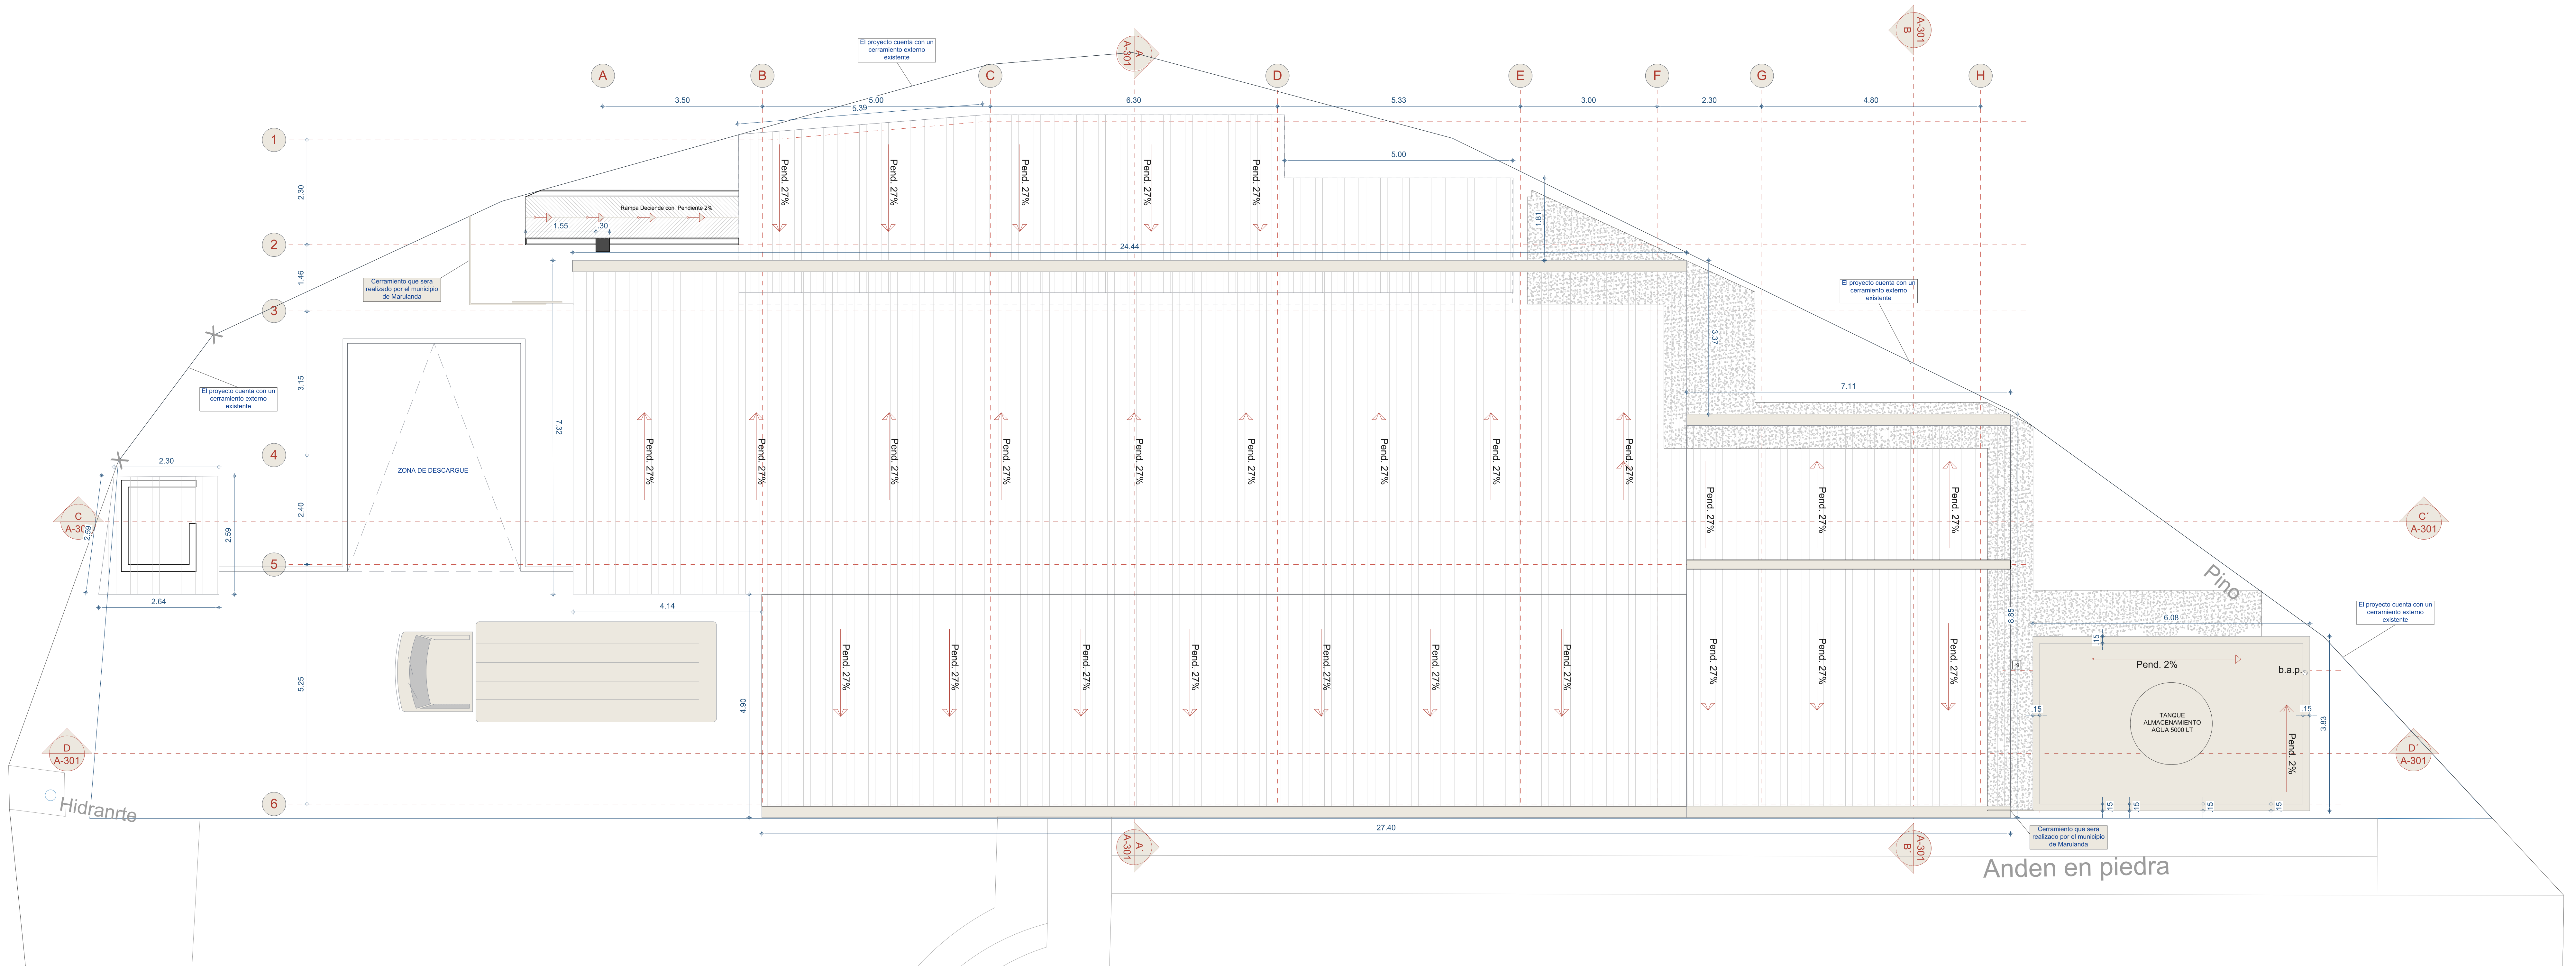

El proyecto cuenta con un cerramiento externo existente
A
B
C
D
E
F
G
H
1
2
3
4
5
6
3.50
5.00
5.39
6.30
5.33
3.00
2.30
4.80
24.44
27.40
7.11
6.08
8.85
3.83
2.30
1.46
3.15
2.40
5.25
7.32
4.14
4.90
2.64
2.59
Rampa Deciende con Pendiente 2%
1.55
.30
Pend. 27%
Cerramiento que sera realizado por el municipio de Marulanda
ZONA DE DESCARGUE
Pend. 2%
b.a.p.
TANQUE ALMACENAMIENTO AGUA 5000 LT
.15
Pino
Hidranrte
Anden en piedra
A A-301
B A-301
B´ A-301
C A-301
C´ A-301
D A-301
D´ A-301

PLANTA DE CUBIERTAS
ESCALA 1:75

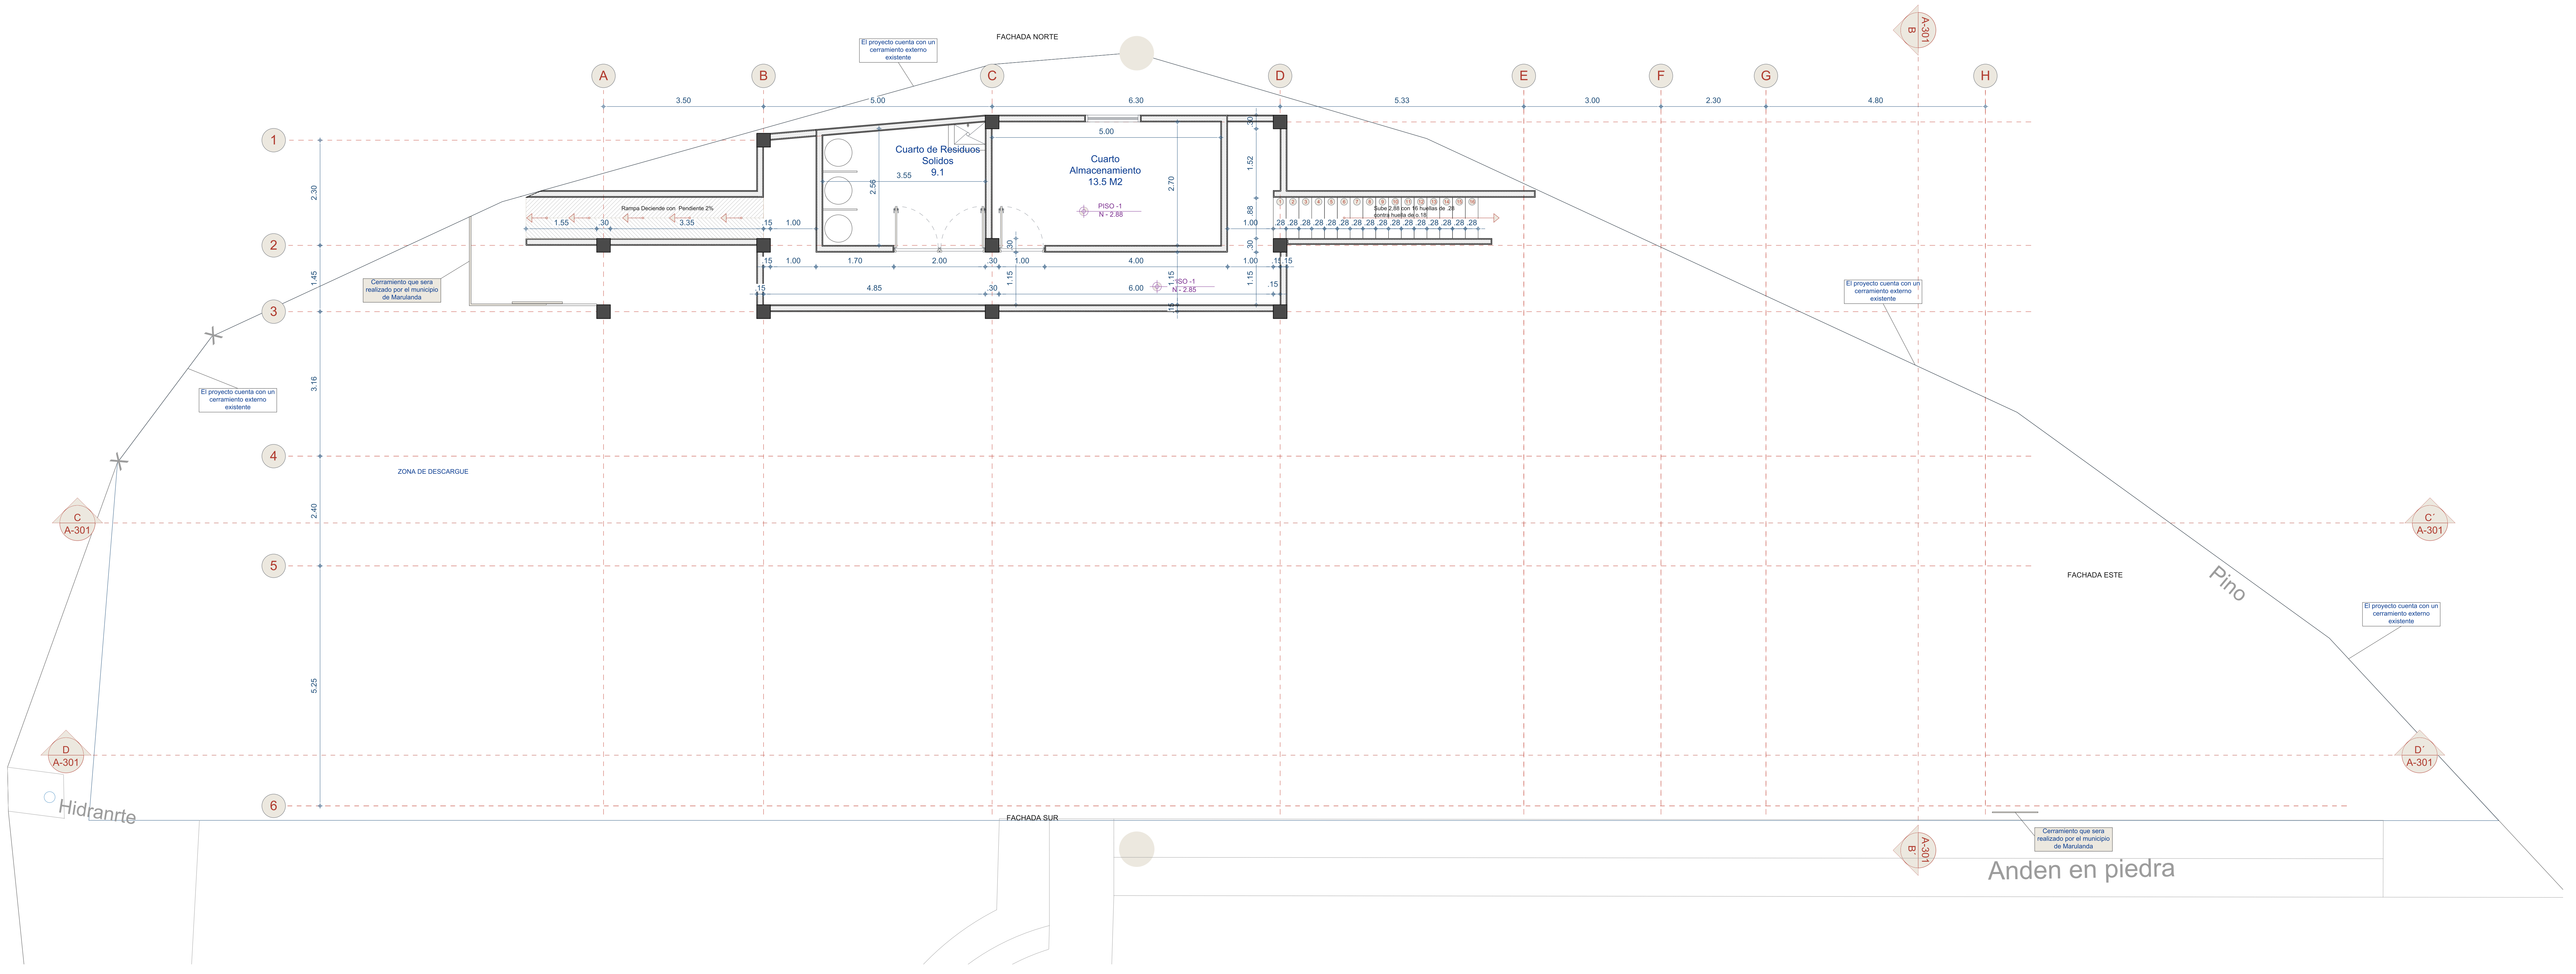

FACHADA NORTE
El proyecto cuenta con un cerramiento externo existente
A
B
C
D
E
F
G
H
1
2
3
4
5
6
3.50
5.00
6.30
5.33
3.00
2.30
4.80
Cuarto de Residuos Solidos 9.1
Cuarto Almacenamiento 13.5 M2
PISO -1 N - 2.88
PISO -1 N - 2.85
Rampa Deciende con Pendiente 2%
Sube 2.88 con 16 huellas de .28 contra huella de o.18
1.55
.30
3.35
1.00
1.70
2.00
4.00
4.85
6.00
3.55
2.56
2.70
1.52
.88
1.15
.15
.28
Cerramiento que sera realizado por el municipio de Marulanda
ZONA DE DESCARGUE
FACHADA ESTE
FACHADA SUR
Pino
Hidranrte
Anden en piedra
B A-301
C A-301
C´ A-301
D A-301
D´ A-301

PLANTA PISO -1
ESCALA 1:75

A-002
PLANO No:
PLANCHA No: **02**
DE: **05**

PROYECTO:

CONSTRUCCIÓN DE LA
INFRAESTRUCTURA DE LA PLANTA DE
TRANSFORMACIÓN DE LÁCTEOS
MUNICIPIO MARULANDA

MUNICIPIO DE MARULANDA - CALDAS
DIRECCIO: CARRERA 6 # 5 - 02

SUPERVISOR:

ING, MAYRA ALEJANDRA RAMIREZ RAMIREZ
SECRETARIA DE PLANEACIÓN

PROFESIONAL RESPONSABLE:

ARQ. DANIEL GONZALEZ AGUIRRE
M.P. A451492024-1000047231

DISEÑADOR DE ELEMENTOS NO ESTRUCTURALES

ING. CRISTIAN FERNEY HERRERA H
MAT. P. 17202-359548CLD
GRADO DE DESEMPEÑO DE ELEMENTOS NO ESTRUCTURALES (BAJO), GRUPO DE USO FABRIL E INDUSTRIAL (F), SUBGRUPO DE OCUPACION FABRIL E INDUSTRIAL DE RIESGO BAJO (F-2).

PROYECTO:

OBJETO: "CONSTRUCCIÓN DE LA
INFRAESTRUCTURA DE LA PLANTA DE
TRANSFORMACIÓN DE LÁCTEOS
MUNICIPIO MARULANDA**"**

OBRA NUEVA DE EDIFICACIÓN CON USO FABRIL E INDUSTRIAL 2 (F-2)

CONTENIDO

PLANTA N - 2.85
PLANTA DE CUBIERTAS N+ 8.41

CONVENCIONES

P. PISOS
M. ACABADOS MUROS
T. ACABDO CIELO RASO
N. NIVEL FINO
G. GUARDAESCOBA
H. ALTURA LIBRE

MATERIALES

G. GRANITO
MR. MARMOL
V. VINILO
L. LADRILLO TOLETE
BL. BLOQUE N°5
C. CONCRETO ABUJARDADO
C. CONCRETO ESMALTADO

LOCALIZACION:

NOTA: ESCALA
GRAFICA

FECHA
2026

Todas las Medidas deberán ser Rectificadas en Obra, Cuenta y Riesgo de Cada uno de los Contratistas.

PLANO No:
A-002
PLANCHA No: **02**
DE: **05**

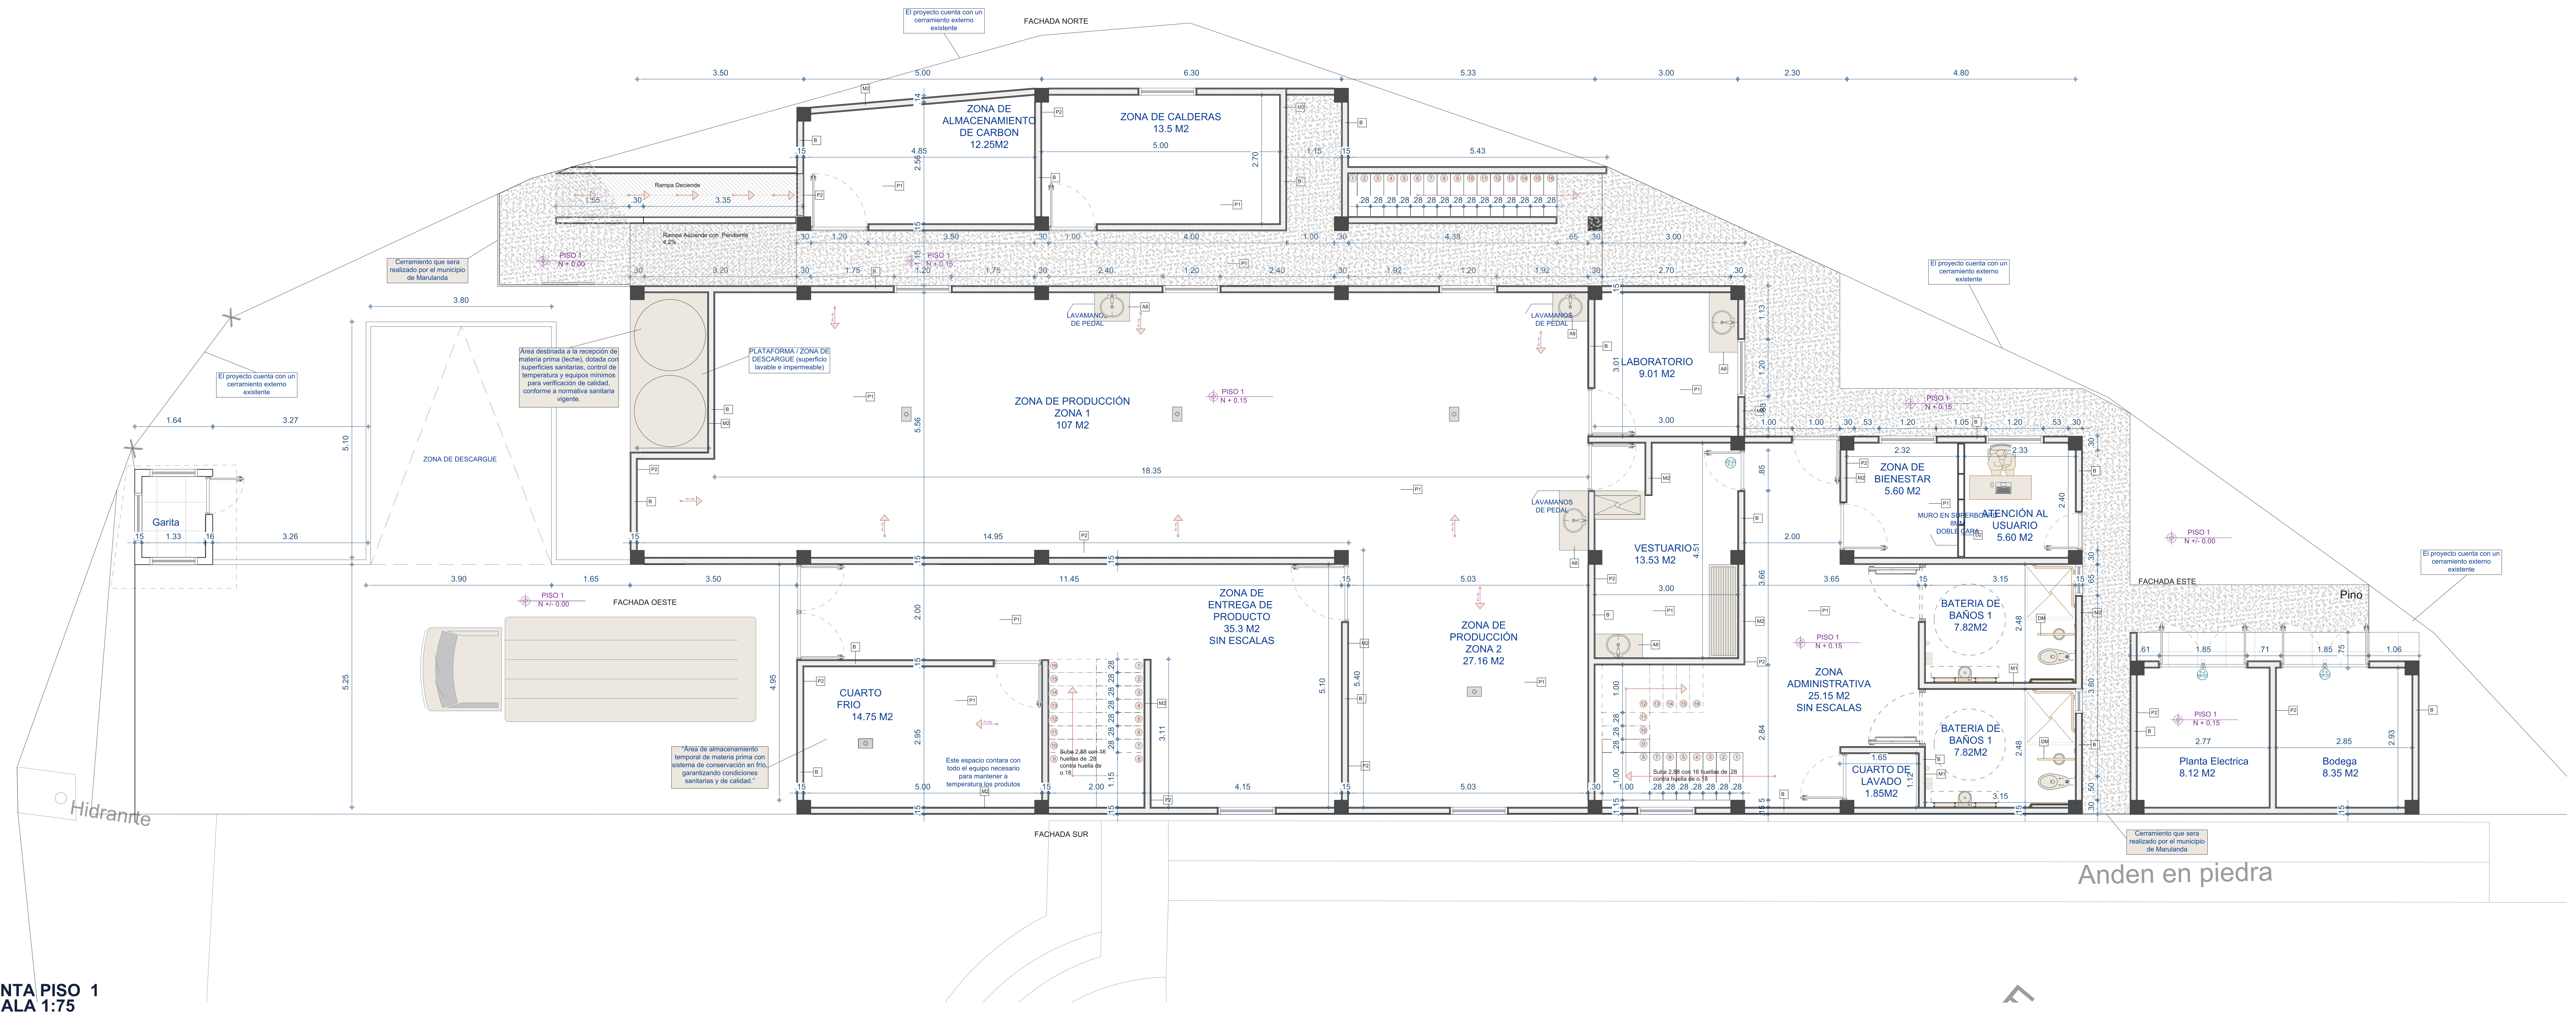
FACHADA NORTE
ZONA DE ALMACENAMIENTO DE CARBON 12.25M2
ZONA DE CALDERAS 13.5 M2
ZONA DE PRODUCCIÓN ZONA 1 107 M2
LABORATORIO 9.01 M2
ZONA DE BIENESTAR 5.60 M2
ATENCIÓN AL USUARIO 5.60 M2
VESTUARIO 13.53 M2
ZONA ADMINISTRATIVA 25.15 M2 SIN ESCALAS
BATERIA DE BAÑOS 1 7.82M2
BATERIA DE BAÑOS 1 7.82M2
CUARTO DE LAVADO 1.85M2
Planta Electrica 8.12 M2
Bodega 8.35 M2
ZONA DE ENTREGA DE PRODUCTO 35.3 M2 SIN ESCALAS
ZONA DE PRODUCCIÓN ZONA 2 27.16 M2
CUARTO FRIO 14.75 M2
ZONA DE DESCARGUE
Garita
FACHADA OESTE
FACHADA ESTE
FACHADA SUR
Pino
Hidranrte
Anden en piedra

PLANTA PISO 1
ESCALA 1:75

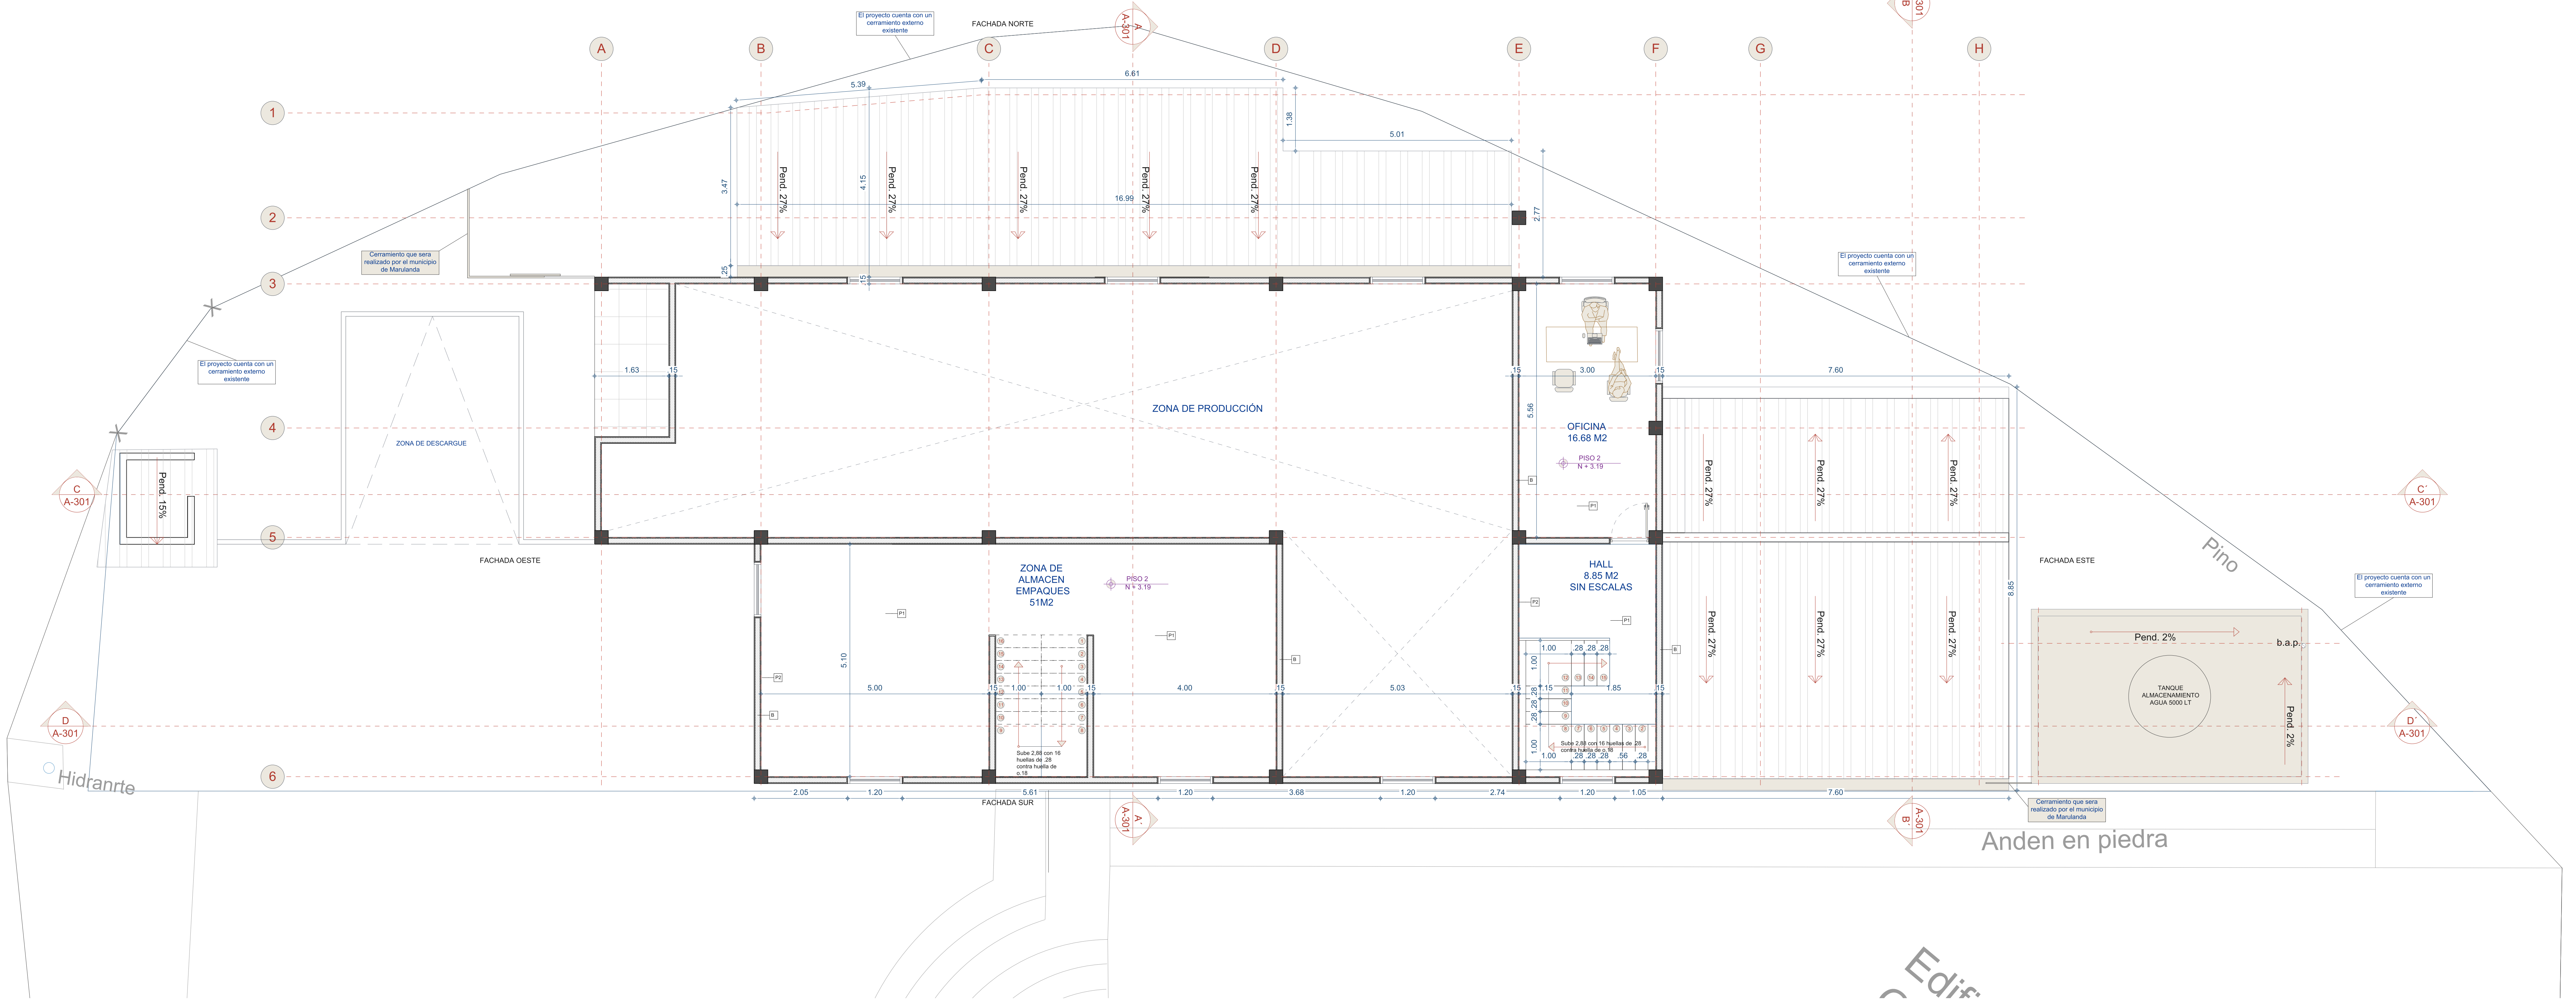
FACHADA NORTE
A B C D E F G H
1 2 3 4 5 6
Pend. 27%
ZONA DE PRODUCCIÓN
ZONA DE DESCARGUE
OFICINA 16.68 M2
ZONA DE ALMACEN EMPAQUES 51M2
HALL 8.85 M2 SIN ESCALAS
TANQUE ALMACENAMIENTO AGUA 5000 LT
Pend. 2%
Pend. 15%
FACHADA OESTE
FACHADA ESTE
FACHADA SUR
Pino
Hidranrte
Anden en piedra

PLANTA PISO 2
ESCALA 1:75

NOTAS GENERALES CIVILES

1. Prever dilataciones en cielo raso para columnas de 2 cm.
2. Cerramiento en muro con altura de 3.15m, referirse a planos de detalle.

NOTAS GENERALES DE PLANCHA

1. El norte hace referencia a la forma en que se debe orientar el proyecto al momento de ser implantado

NOTAS DE REFERENCIA

DIVISIONES Y MUROS

B	Muro en bloque N° 5	B
D1	Muro en fibrocemento de una cara	D1
D2	Muro en fibrocemento de 12 cm	D2
DM	División y puerta en acero inoxidable calibre 18, separadas del piso 0,20 m	DM

ACABADOS DE MURO

1	Enchape ceramico blanco formato 0.25 x 0.40	M1
2	Estuco plastico y pintura vinilo 3 manos blanco.	M2
3	Pintura acrilica para exteriores color blanco.	M3
4	Pintura epóxica blanca	M4

ACABADOS DE PISO

1	PISO CON RECUBRIMIENTO POLIMÉRO DE ALTA RESISTENCIA.	P1
2	MEDIACAÑA CON MORTERO EPOXICO DE ALTA RESISTENCIA.	P2
3	Guardaescoba media caña fundido en granito	P3
4	Piso en baldosa ceramica trafico pesado 33.8 X 33.8	P4
5	Loseta de cemento prepulida gris	P5
6	Bocapuerta en granito perlato	P6

ACABADO CIELO RASO — CI1

1	Lamina de1.20 x 0.60 m de fibra mineral, color blanco.	

APARATOS

1	Meson en concreto, acabado en granito pulido.	A1
2	Sanitario con fluxometro y asiento institucional o similar	A2
3	Lavamanos tipo marsella blanco o similar, con griferia galaxia 8 o similar.	A3
4	Ducharegistro tipo prisma o similar.	A4
5	Lavaplatos en acero inoxidable con poceta y escurridero.	A5
6	Protector para papel higuienico accesorios y acabados o similar	A6
7	Barra de seguridad para discapacitados en acero inoxidable de 36".	A7
8	Barra de seguridad para discapacitados en acero inoxidable de 24".	A8
9	Espejo con borde biselado de 0.70 x 1.30 / E: 0.04 m	A9
10	Dispensador de jabon para muro	A10
11	Canecas para basura en verde, rojo y gris	A11

A-003
PLANO No:
PLANCHA No: **03**
DE: **05**

PROYECTO:

CONSTRUCCIÓN DE LA
INFRAESTRUCTURA DE LA PLANTA DE
TRANSFORMACIÓN DE LÁCTEOS
MUNICIPIO MARULANDA

MUNICIPIO DE MARULANDA - CALDAS
DIRECCIO: CARRERA 6 # 5 - 02

SUPERVISOR:

ING, MAYRA ALEJANDRA RAMIREZ RAMIREZ
SECRETARIA DE PLANEACIÓN

PROFESIONAL RESPONSABLE:

ARQ. DANIEL GONZALEZ AGUIRRE
M.P. A451492024-1000047231

DISEÑADOR DE ELEMENTOS NO ESTRUCTURALES

ING. CRISTIAN FERNEY HERRERA H
MAT. P. 17202-359548CLD
GRADO DE DESEMPEÑO DE ELEMENTOS NO ESTRUCTURALES (BAJO), GRUPO DE USO FABRIL E INDUSTRIAL (F), SUBGRUPO DE OCUPACION FABRIL E INDUSTRIAL DE RIESGO BAJO (F-2).

PROYECTO:

OBJETO: "CONSTRUCCIÓN DE LA
INFRAESTRUCTURA DE LA PLANTA DE
TRANSFORMACIÓN DE LÁCTEOS
MUNICIPIO MARULANDA**"**

OBRA NUEVA DE EDIFICACIÓN CON USO FABRIL E INDUSTRIAL 2 (F-2)

CONTENIDO

PLANTA N +/- 0.00
PLANTA N+/- 0.00

CONVENCIONES

P. PISOS
M. ACABADOS MUROS
T. ACABDO CIELO RASO
N. NIVEL FINO
G. GUARDAESCOBA
H. ALTURA LIBRE

MATERIALES

G. GRANITO
MR. MARMOL
V. VINILO
L. LADRILLO TOLETE
BL. BLOQUE N°5
C. CONCRETO ABUJARDADO
C. CONCRETO ESMALTADO

LOCALIZACION:

NOTA: ESCALA **GRAFICA**
FECHA **2026**

Todas las Medidas deberán ser Rectificadas en Obra, Cuenta y Riesgo de Cada uno de los Contratistas.

PLANO No: **A-003**
PLANCHA No: **03**
DE: **05**

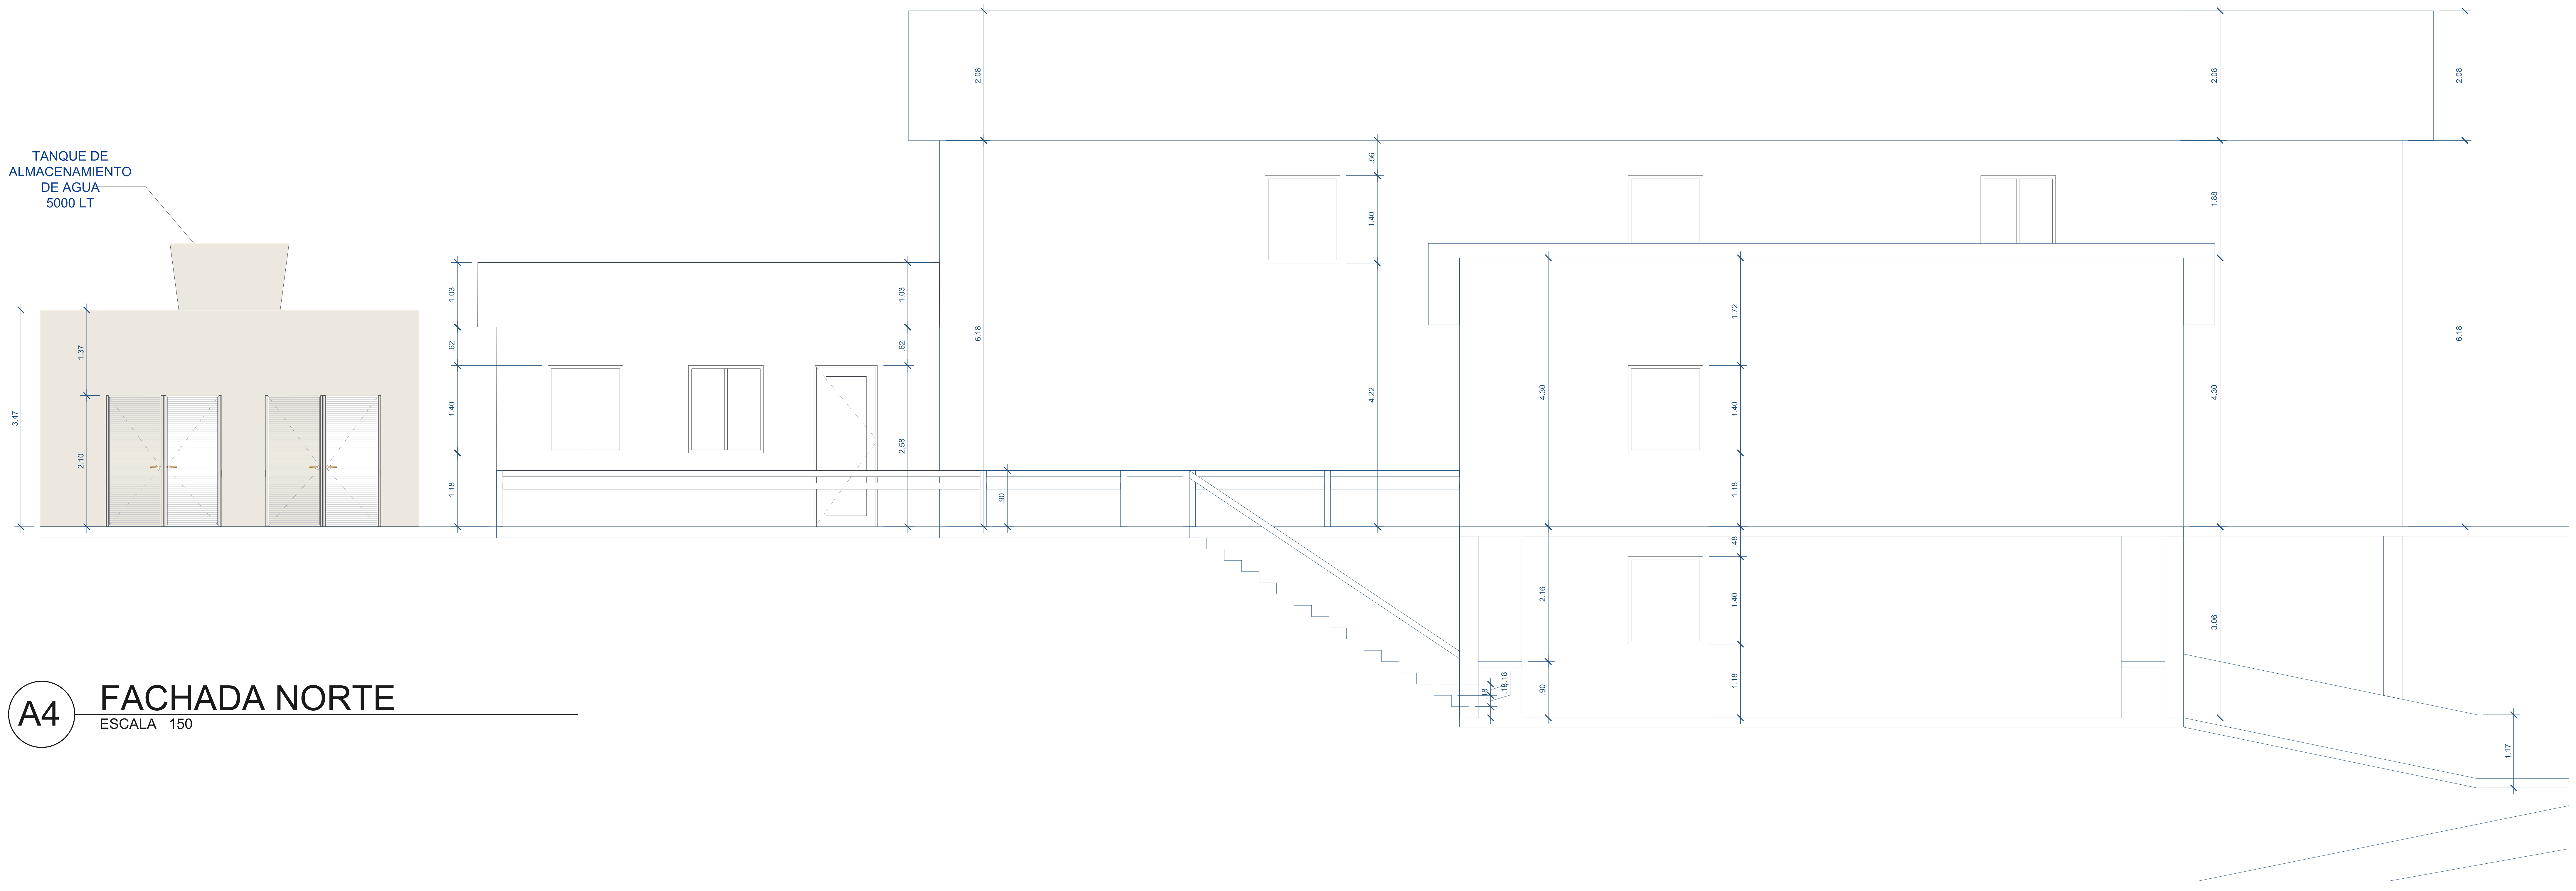

A4 FACHADA NORTE
ESCALA 150

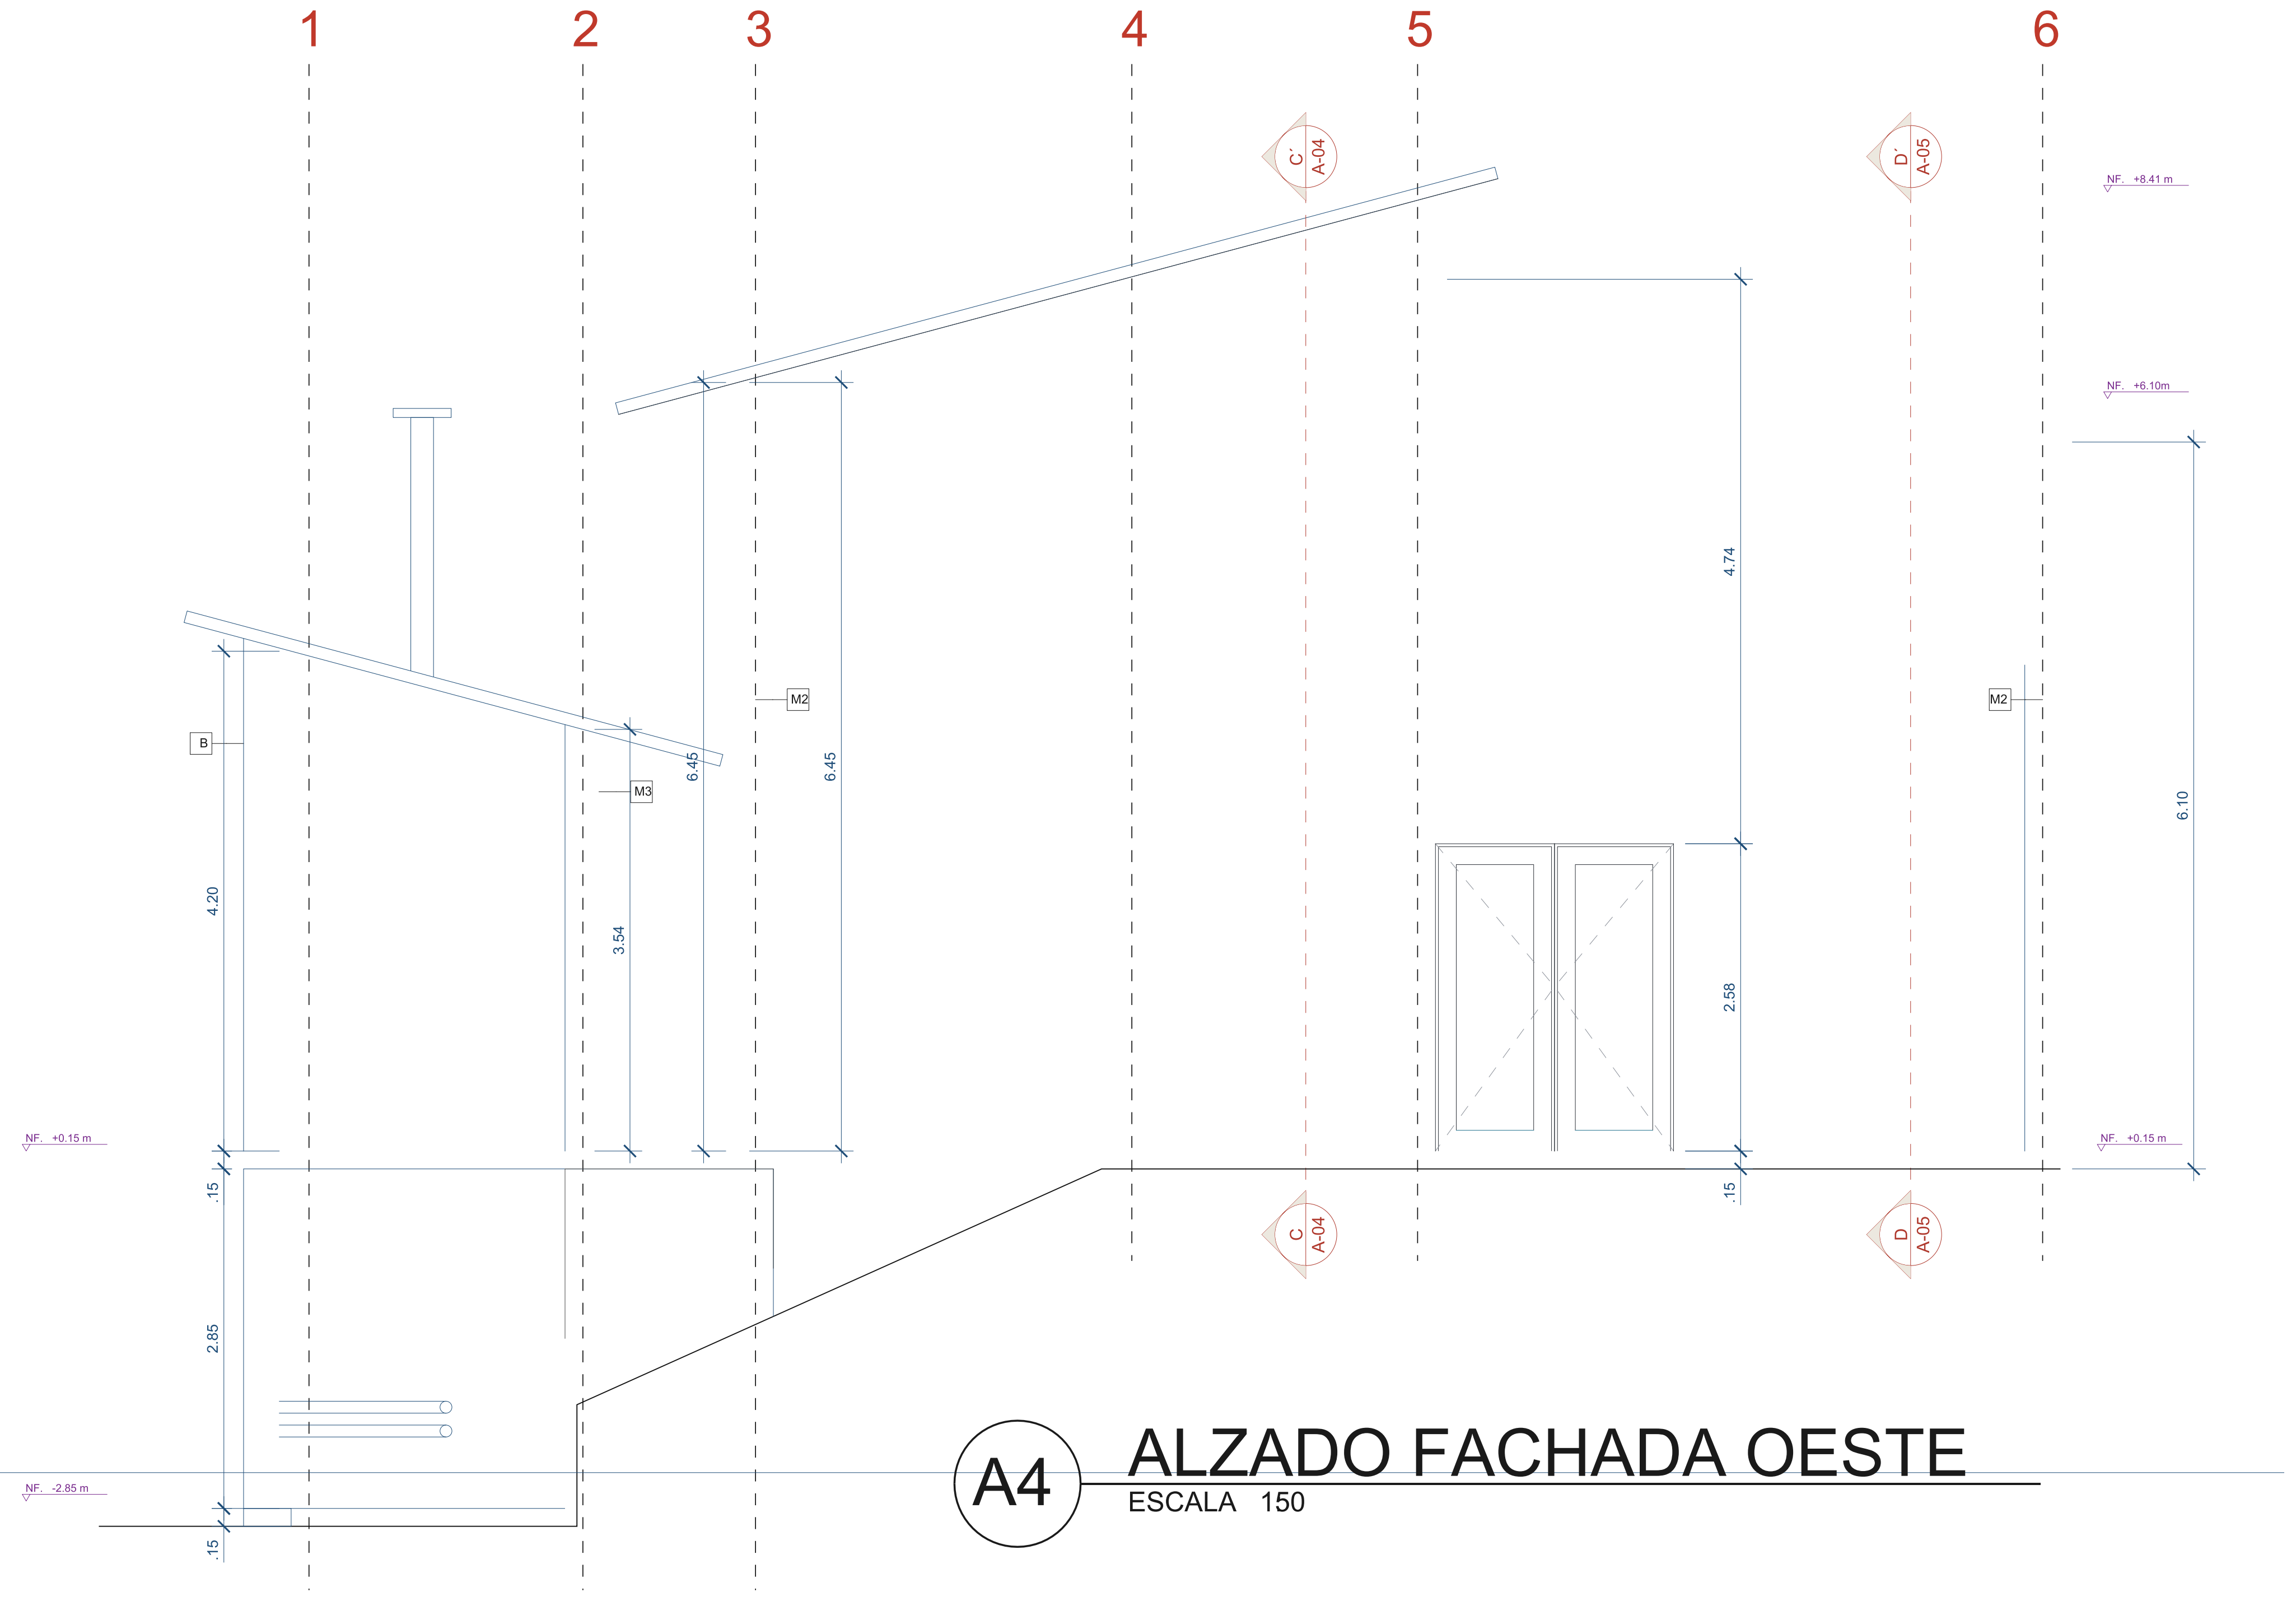

A4 ALZADO FACHADA OESTE
ESCALA 150

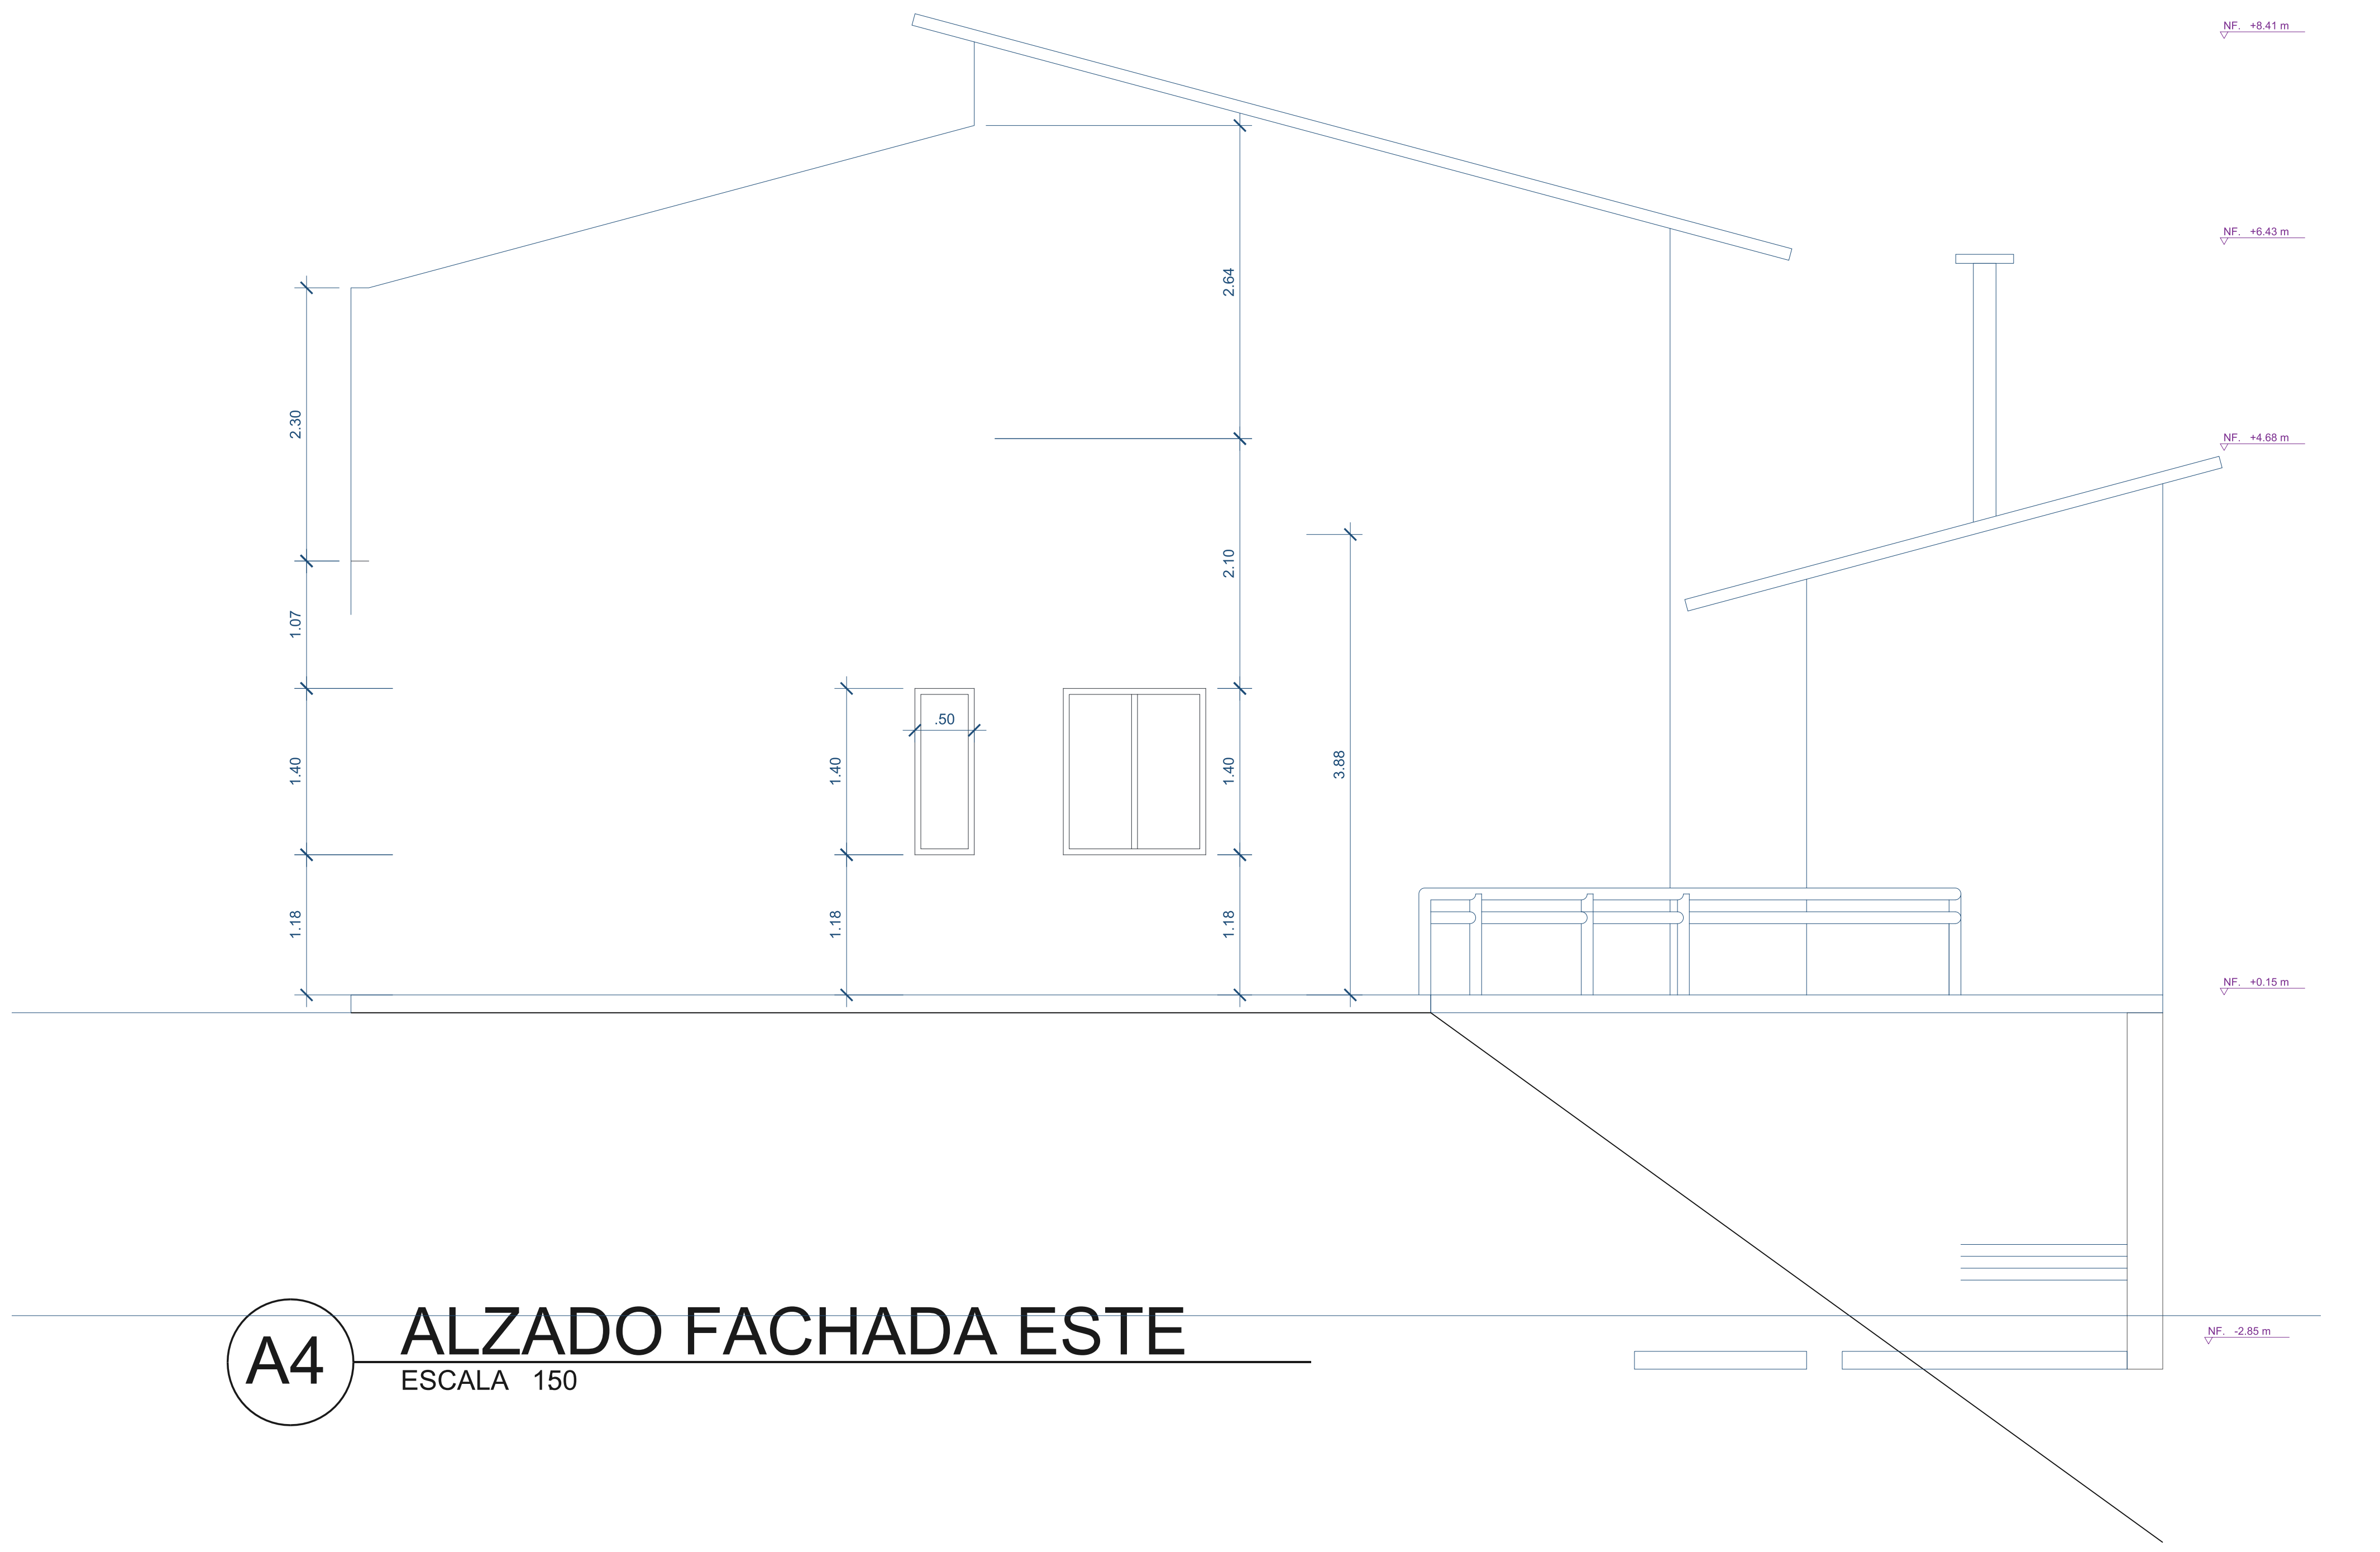

A4 ALZADO FACHADA ESTE
ESCALA 150

PLANO No:
A-004
PLANCHA No: 04
DE: 05

PROYECTO:

CONSTRUCCIÓN DE LA
INFRAESTRUCTURA DE LA PLANTA DE
TRANSFORMACIÓN DE LÁCTEOS
MUNICIPIO MARULANDA

MUNICIPIO DE MARULANDA - CALDAS
DIRECCIO: CARRERA 6 # 5 - 02

SUPERVISOR:

ING, MAYRA ALEJANDRA RAMIREZ RAMIREZ
SECRETARIA DE PLANEACIÓN

PROFESIONAL RESPONSABLE:

ARQ. DANIEL GONZALEZ AGUIRRE
M.P. A451492024-1000047231

DISEÑADOR DE ELEMENTOS NO ESTRUCTURALES

ING. CRISTIAN FERNEY HERRERA H
MAT. P. 17202-359548CLD
GRADO DE DESEMPEÑO DE ELEMENTOS NO ESTRUCTURALES (BAJO), GRUPO DE USO FABRIL E INDUSTRIAL (F), SUBGRUPO DE OCUPACION FABRIL E INDUSTRIAL DE RIESGO BAJO (F-2).

PROYECTO:

OBJETO: "CONSTRUCCIÓN DE LA
INFRAESTRUCTURA DE LA PLANTA DE
TRANSFORMACIÓN DE LÁCTEOS
MUNICIPIO MARULANDA**"**

OBRA NUEVA DE EDIFICACIÓN CON USO FABRIL E INDUSTRIAL 2 (F-2)

CONTENIDO

PLANTA N +/- 0.00
PLANTA DE CUBIERTAS N+/- 0.00

CONVENCIONES

- P. PISOS
- M. ACABADOS MUROS
- T. ACABDO CIELO RASO
- N. NIVEL FINO
- G. GUARDAESCOBA
- H. ALTURA LIBRE

MATERIALES

- G. GRANITO
- MR. MARMOL
- V. VINILO
- L. LADRILLO TOLETE
- BL. BLOQUE N°5
- C. CONCRETO ABUJARDADO
- C. CONCRETO ESMALTADO

LOCALIZACION:

NOTA: ESCALA **GRAFICA**

FECHA **2026**

Todas las Medidas deberán ser Rectificadas en Obra,
Cuenta y Riesgo de Cada uno de los Contratistas.

PLANO No: **A-004**
PLANCHA No: **04**
DE: **5**

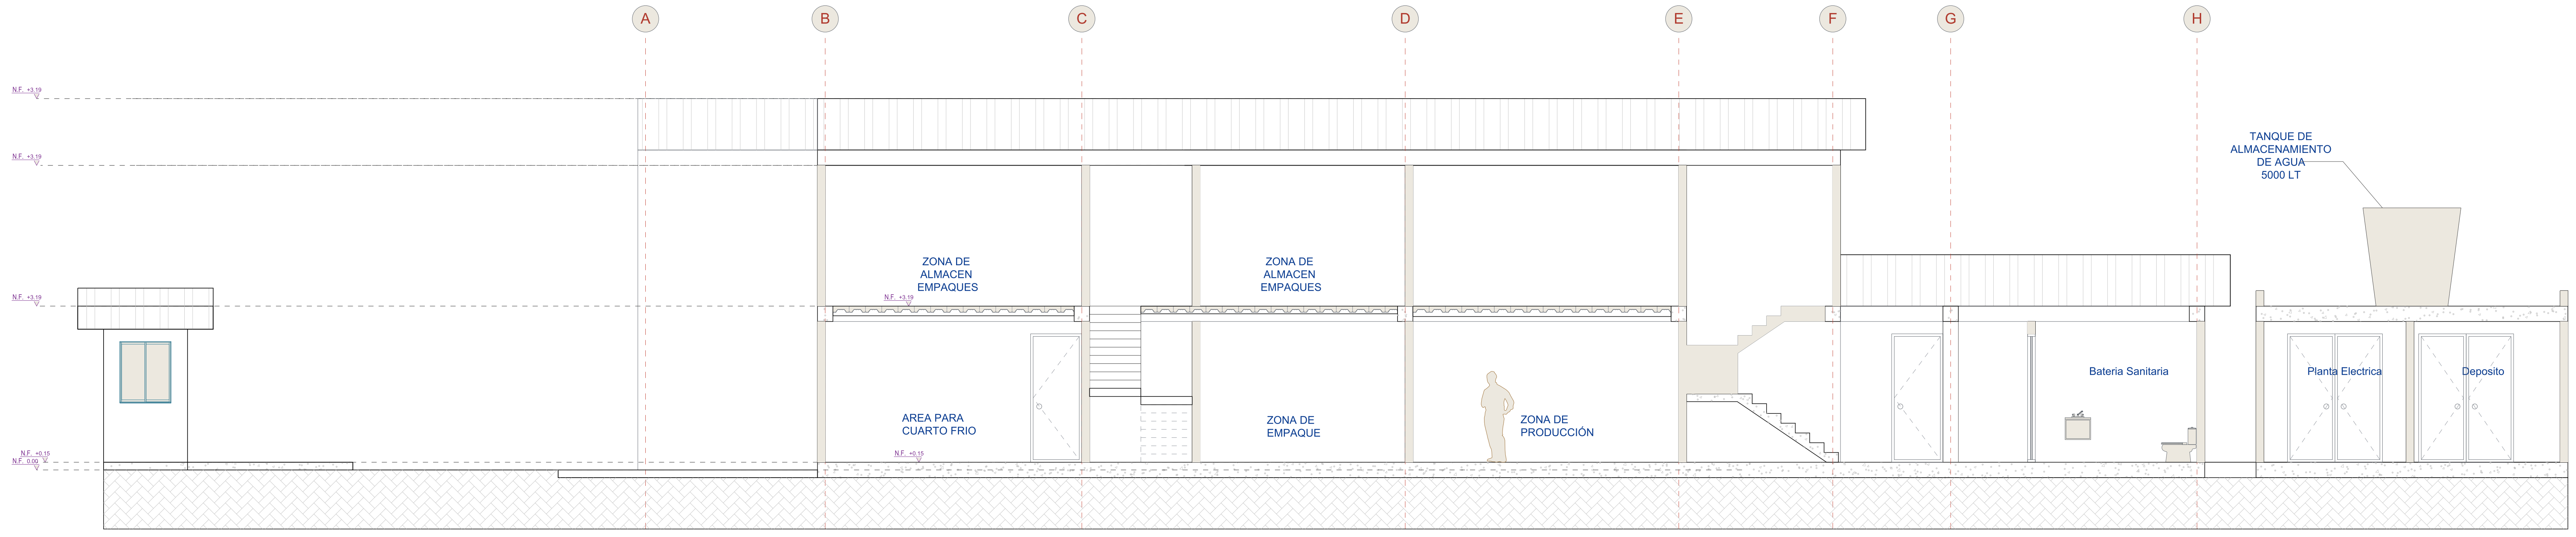
A
B
C
D
E
F
G
H
N.F. +3.19
N.F. +3.19
N.F. +3.19
N.F. +0.15
N.F. 0.00
TANQUE DE
ALMACENAMIENTO
DE AGUA
5000 LT
ZONA DE
ALMACEN
EMPAQUES
ZONA DE
ALMACEN
EMPAQUES
N.F. +3.19
AREA PARA
CUARTO FRIO
N.F. +0.15
ZONA DE
EMPAQUE
ZONA DE
PRODUCCIÓN
Bateria Sanitaria
Planta Electrica
Deposito

A1 CORTE D - D'
ESCALA 175

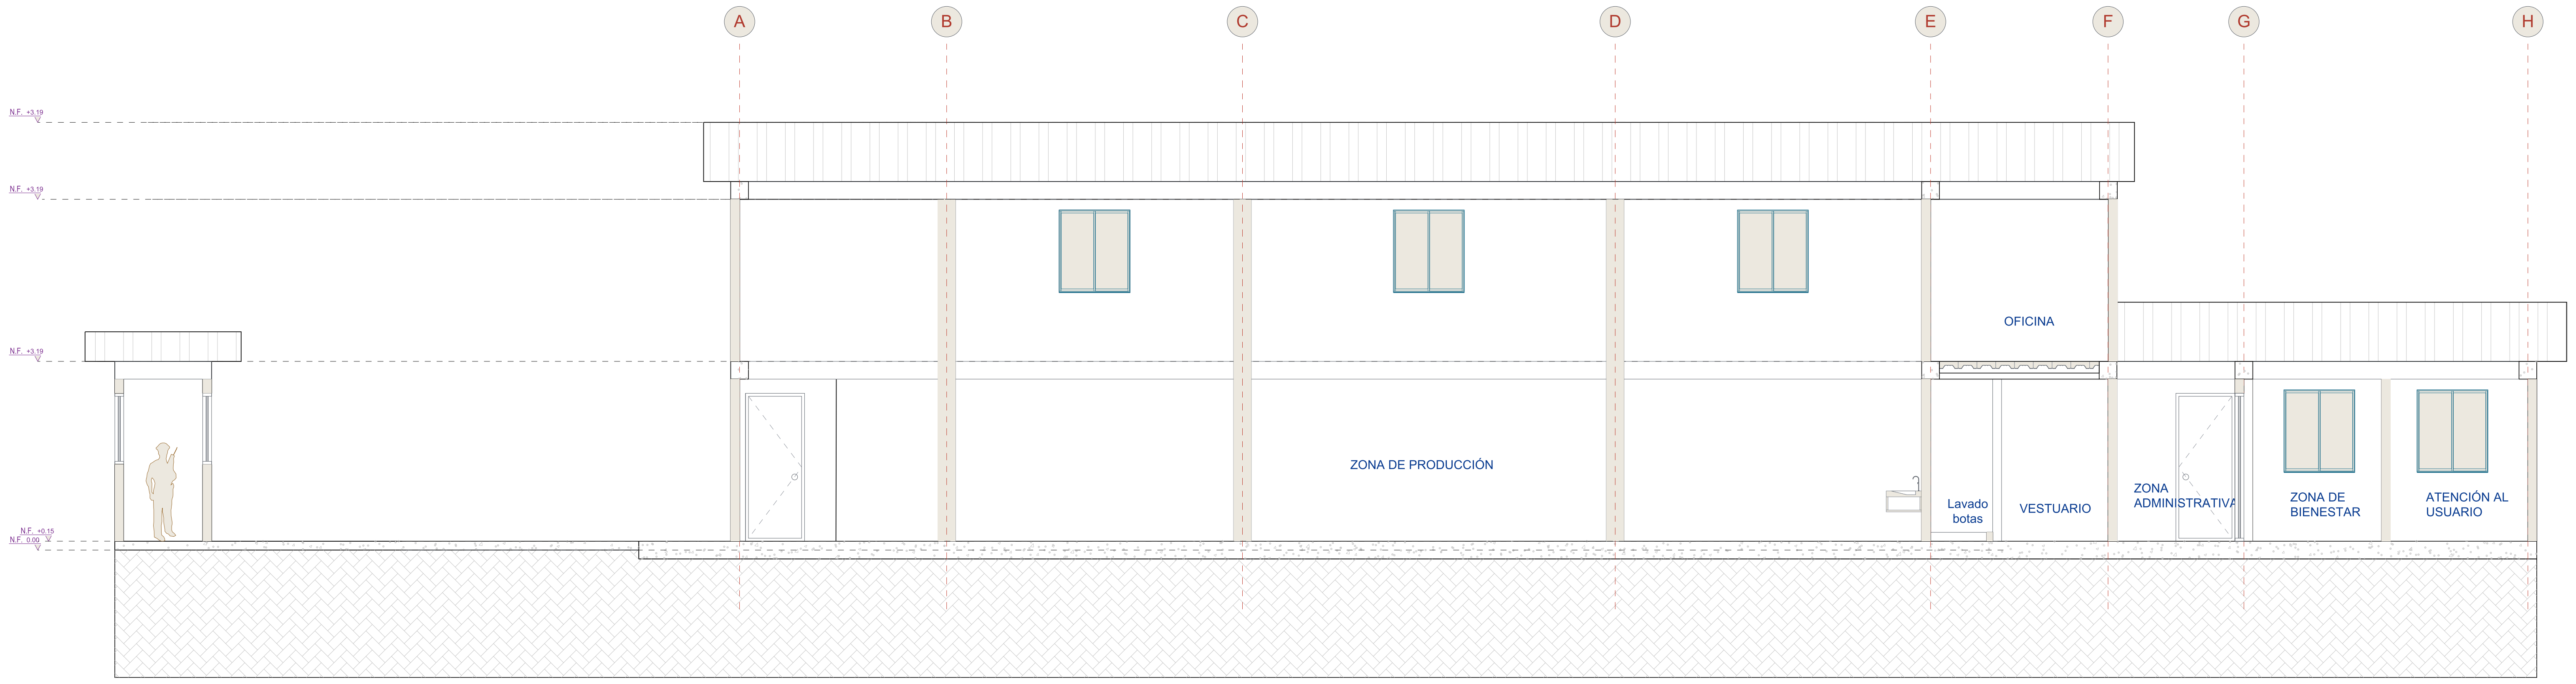
A
B
C
D
E
F
G
H
N.F. +3.19
N.F. +3.19
N.F. +3.19
N.F. +0.15
N.F. 0.00
OFICINA
ZONA DE PRODUCCIÓN
Lavado
botas
VESTUARIO
ZONA
ADMINISTRATIVA
ZONA DE
BIENESTAR
ATENCIÓN AL
USUARIO

A1 CORTE C - C'
ESCALA 175

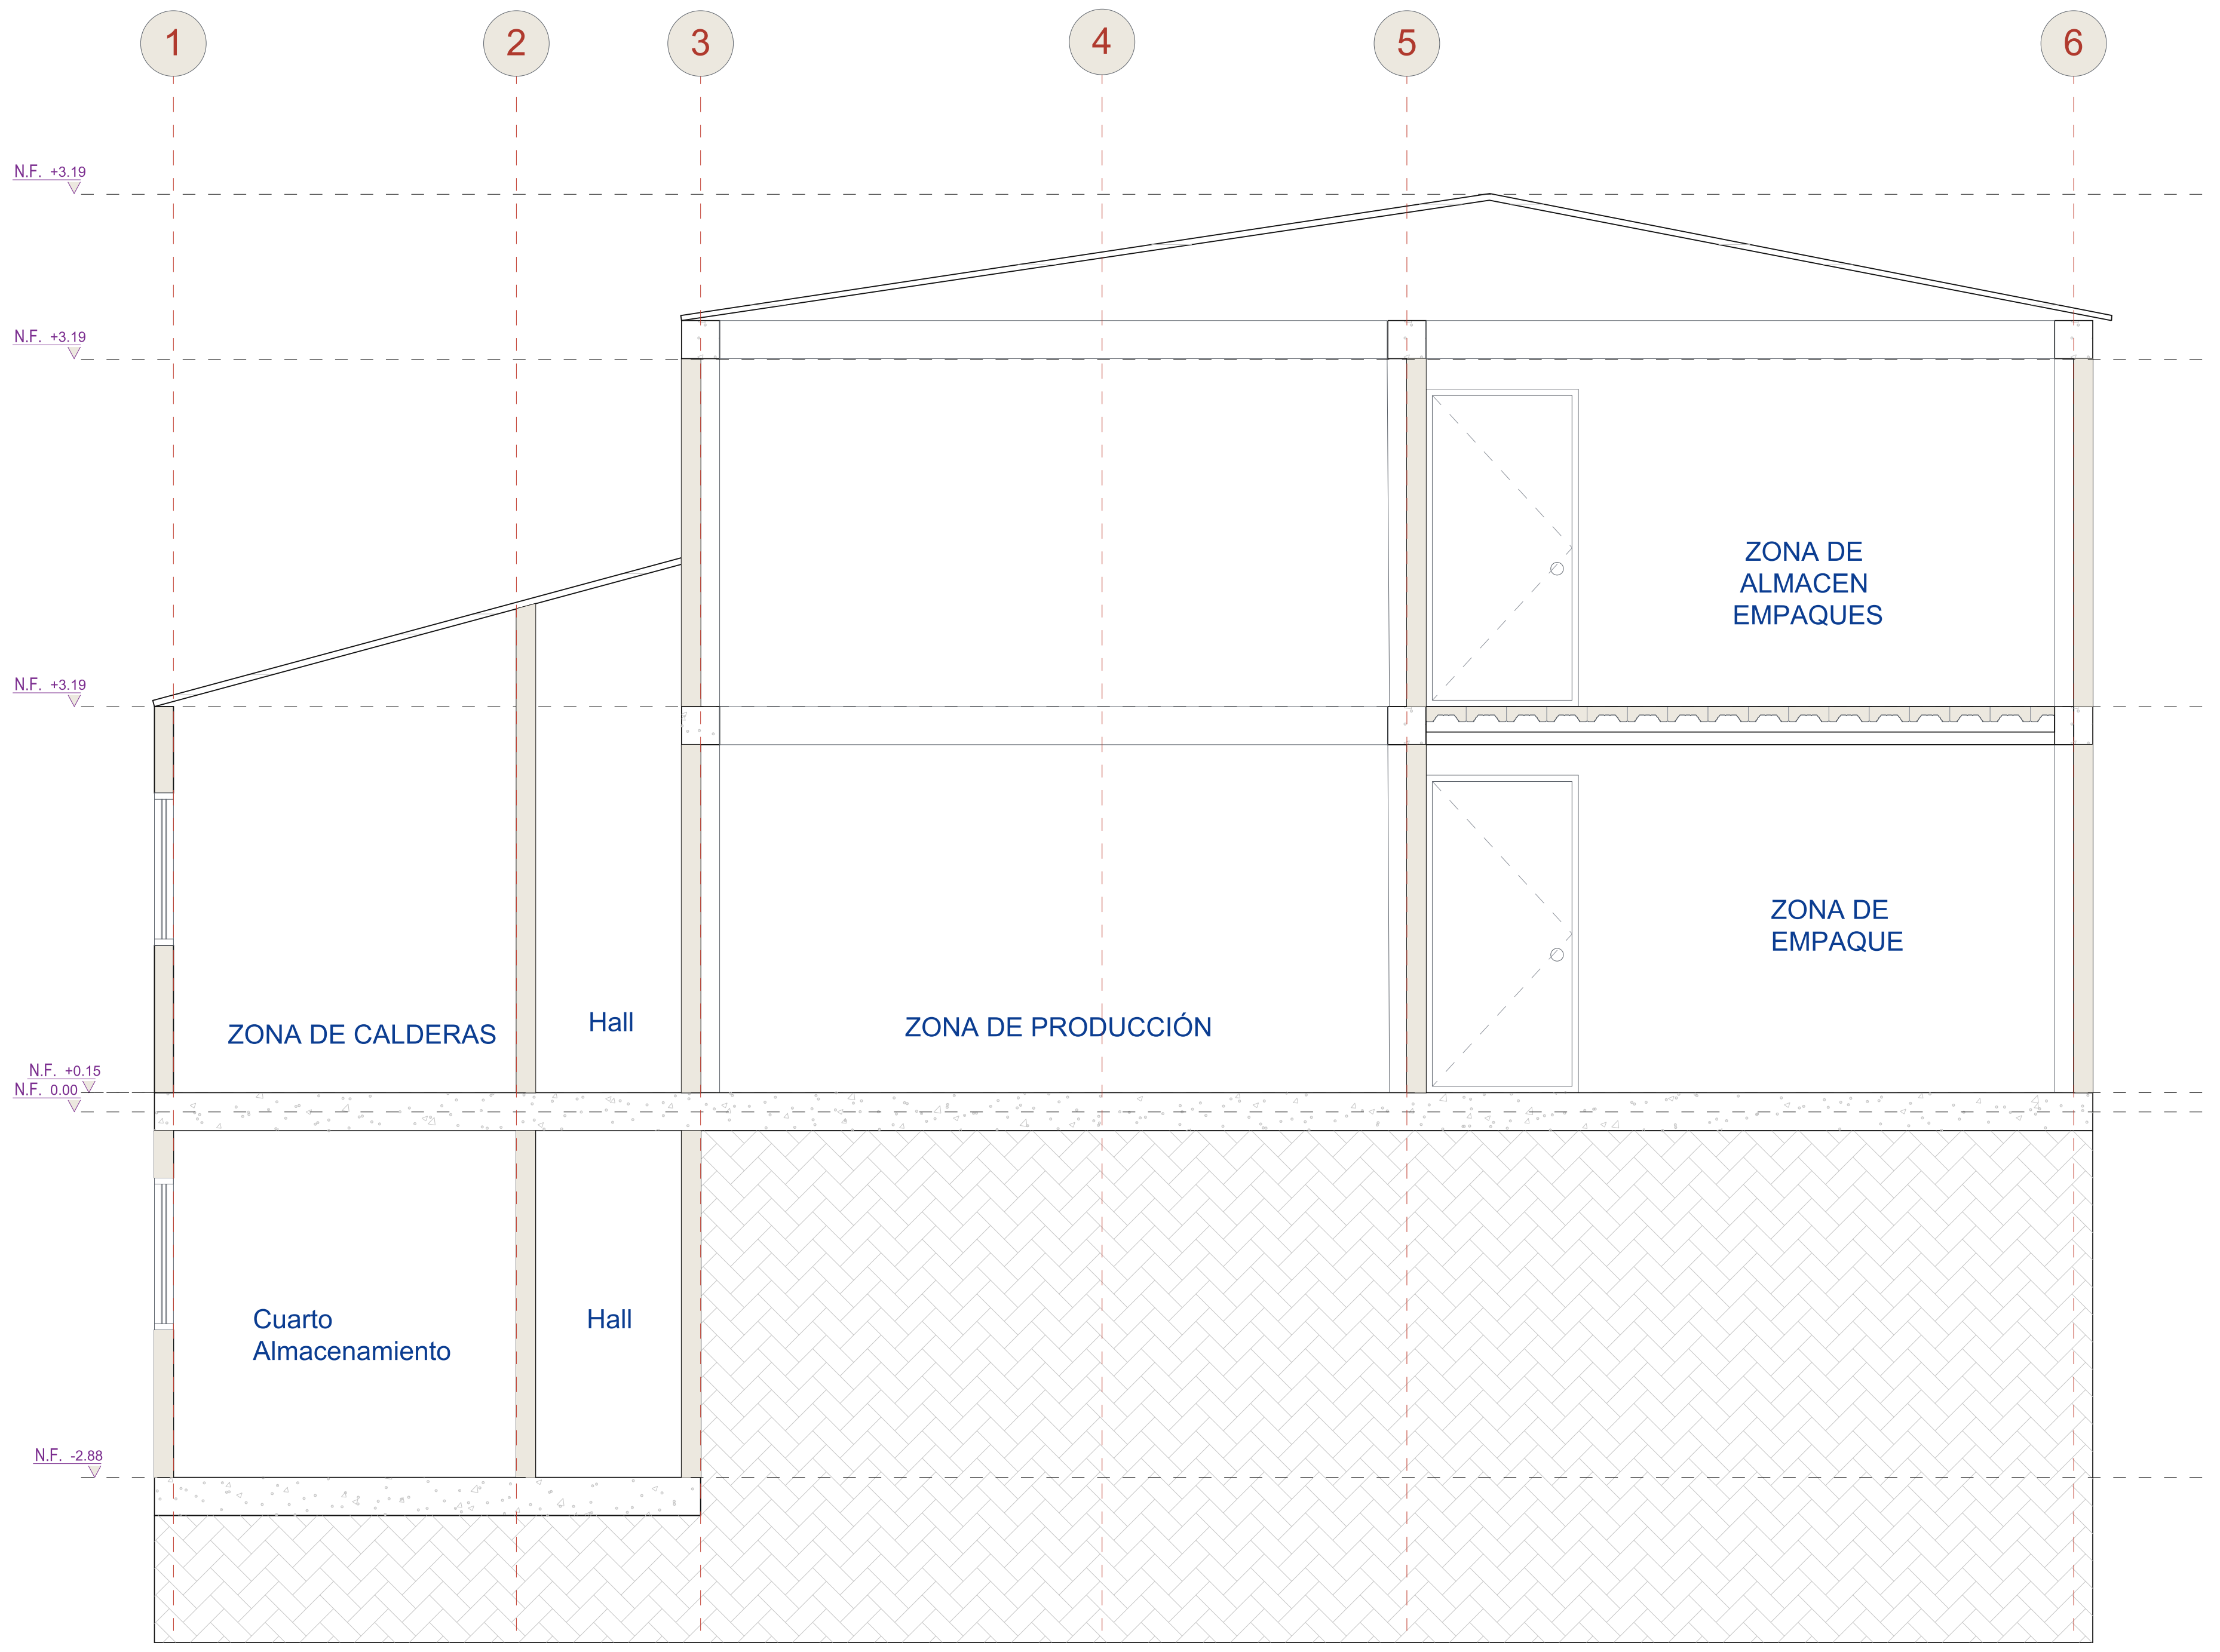
1
2
3
4
5
6
N.F. +3.19
N.F. +3.19
N.F. +3.19
N.F. +0.15
N.F. 0.00
N.F. -2.88
ZONA DE
ALMACEN
EMPAQUES
ZONA DE
EMPAQUE
ZONA DE CALDERAS
Hall
ZONA DE PRODUCCIÓN
Cuarto
Almacenamiento
Hall

A1 CORTE A - A'
ESCALA 150

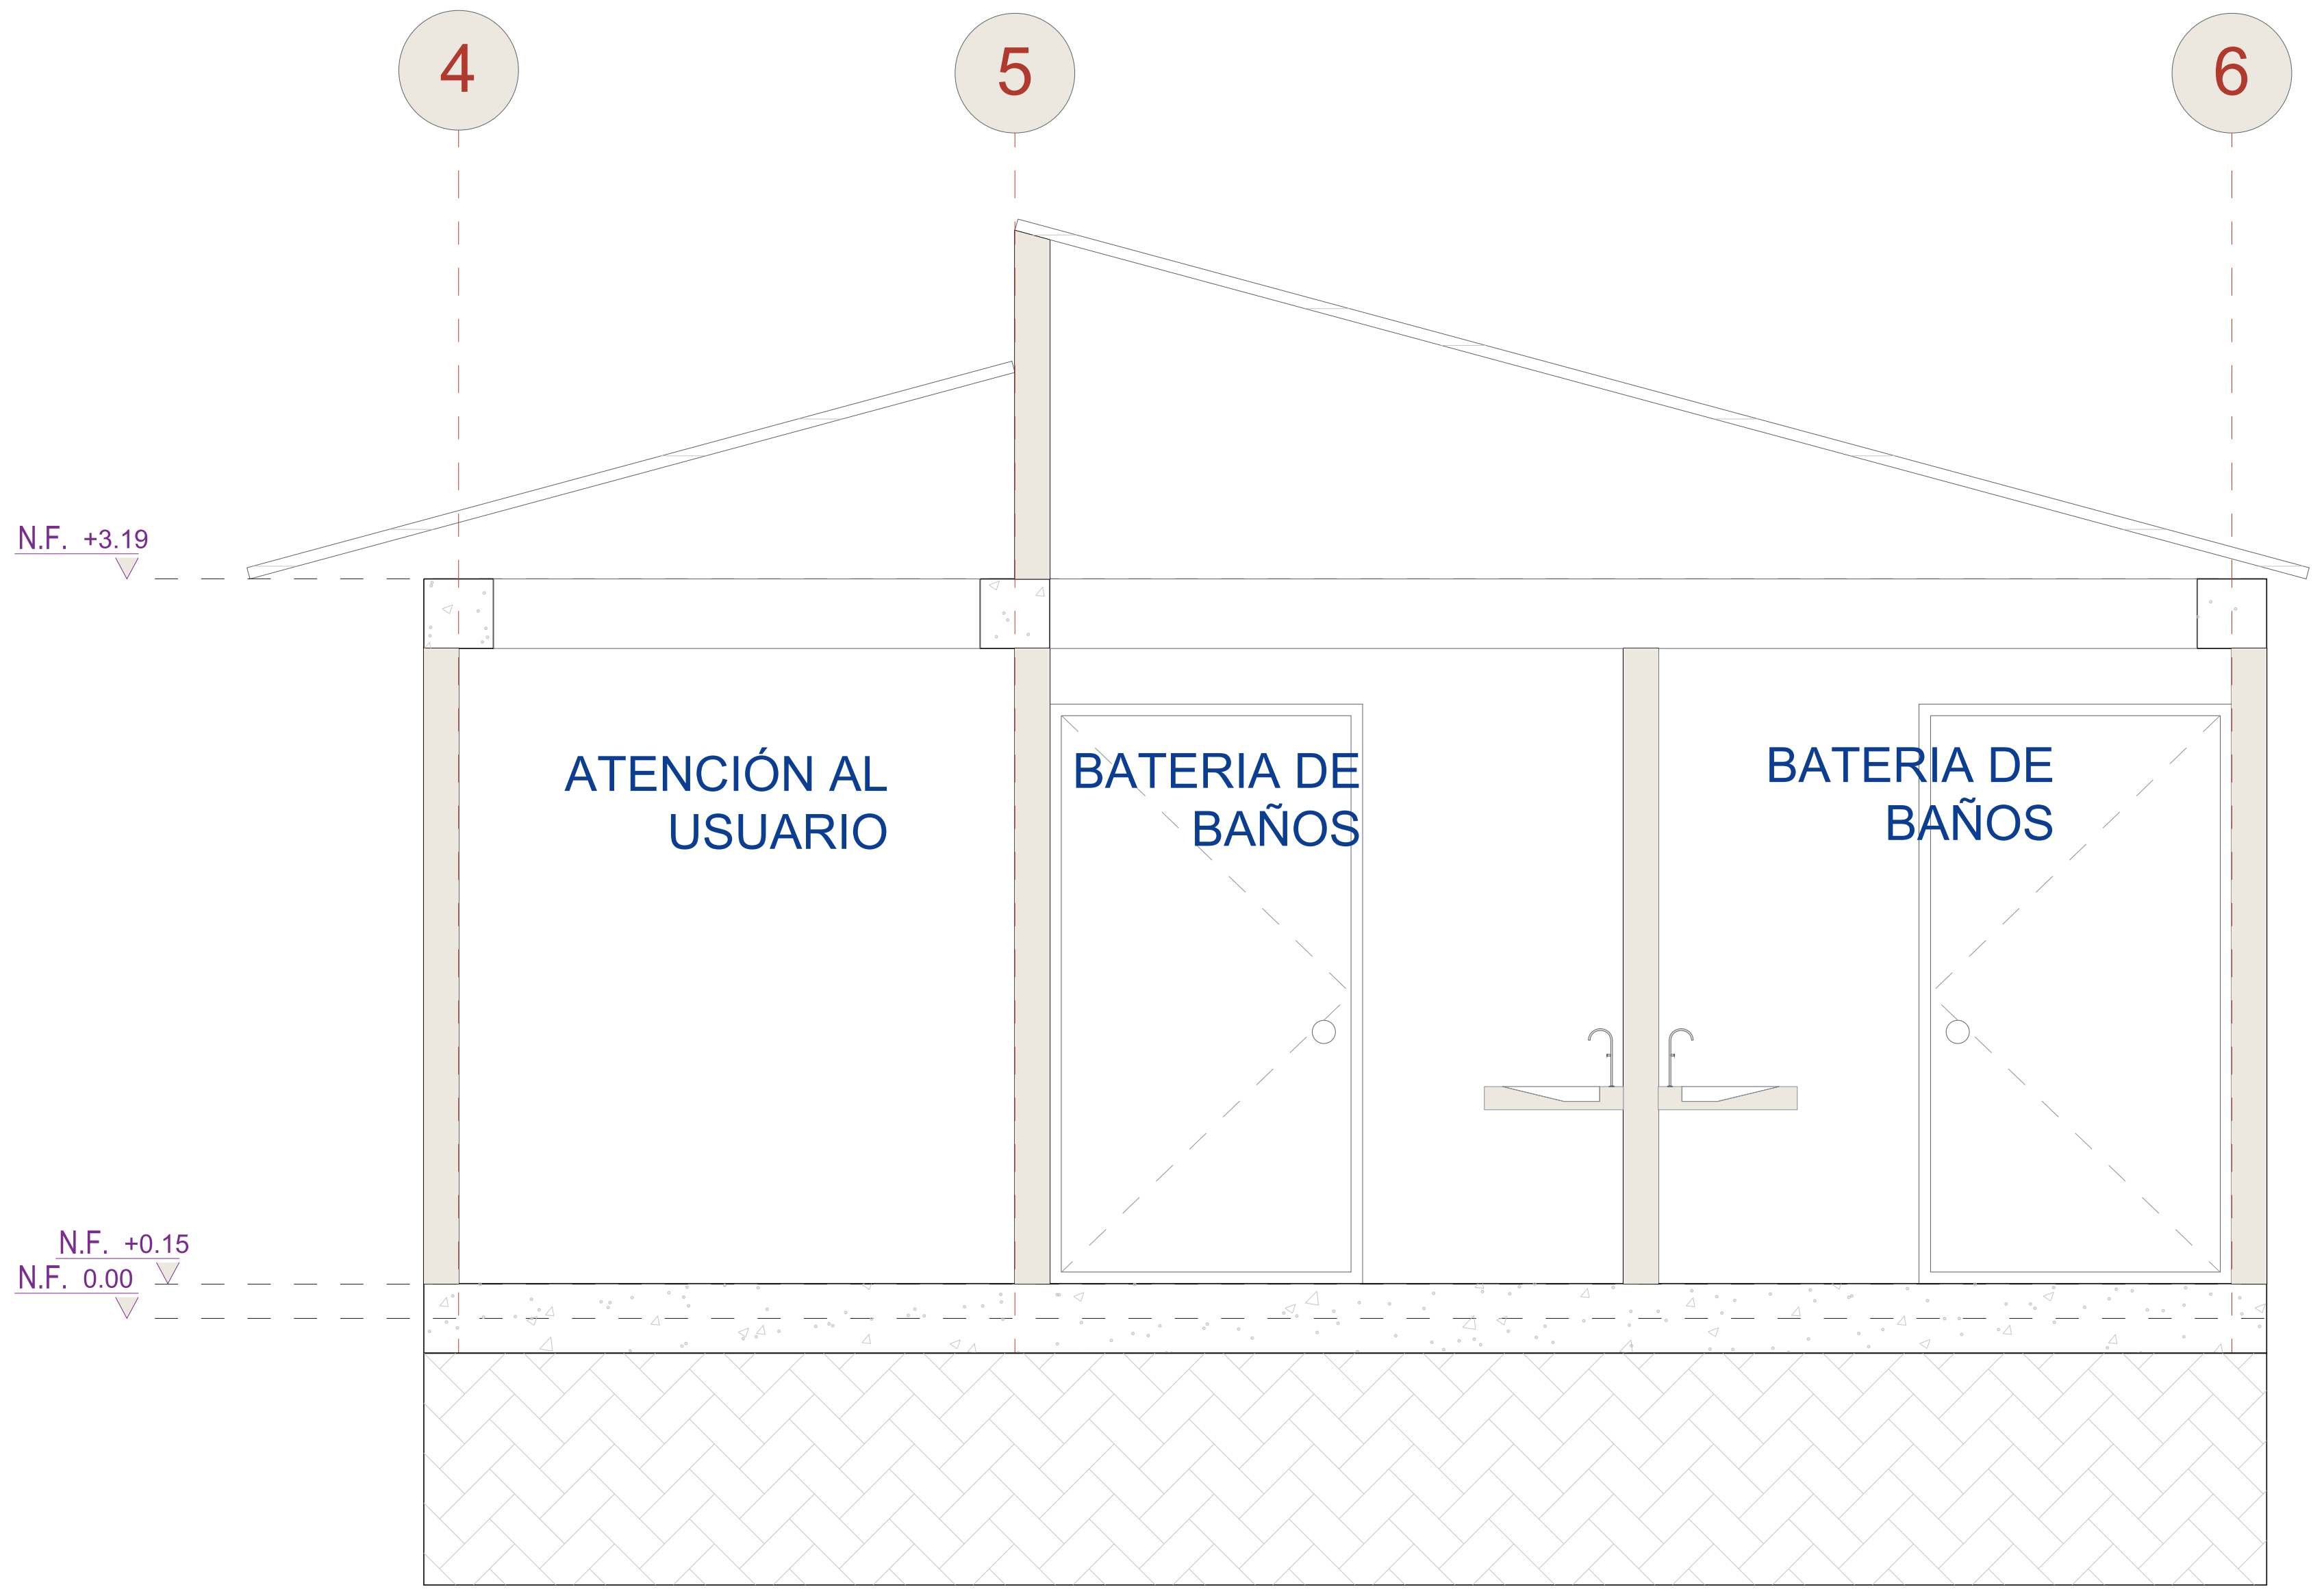
4
5
6
N.F. +3.19
ATENCIÓN AL
USUARIO
BATERIA DE
BAÑOS
BATERIA DE
BAÑOS
N.F. +0.15
N.F. 0.00

A1 CORTE B - B'
ESCALA 150

A-005
PLANO No:
PLANCHA No: 05
DE: 05

PROYECTO:

CONSTRUCCIÓN DE LA
INFRAESTRUCTURA DE LA PLANTA DE
TRANSFORMACIÓN DE LÁCTEOS
MUNICIPIO MARULANDA

MUNICIPIO DE MARULANDA - CALDAS
DIRECCIO: CARRERA 6 # 5 - 02

SUPERVISOR:

ING, MAYRA ALEJANDRA RAMIREZ RAMIREZ
SECRETARIA DE PLANEACIÓN

PROFESIONAL RESPONSABLE:

ARQ. DANIEL GONZALEZ AGUIRRE
M.P. A451492024-1000047231

DISEÑADOR DE ELEMENTOS NO ESTRUCTURALES

ING. CRISTIAN FERNEY HERRERA H
MAT. P. 17202-359548CLD

GRADO DE DESEMPEÑO DE ELEMENTOS NO ESTRUCTURALES (BAJO), GRUPO DE USO FABRIL E INDUSTRIAL (F), SUBGRUPO DE OCUPACION FABRIL E INDUSTRIAL DE RIESGO BAJO (F-2).

PROYECTO:

OBJETO: "CONSTRUCCIÓN DE LA
INFRAESTRUCTURA DE LA PLANTA DE
TRANSFORMACIÓN DE LÁCTEOS
MUNICIPIO MARULANDA**"**

OBRA NUEVA DE EDIFICACIÓN CON USO FABRIL E INDUSTRIAL 2 (F-2)

CONTENIDO
- Corte A-A
- Corte B-B
- Corte C-C
- Corte D-D

CONVENCIONES

P. PISOS
M. ACABADOS MUROS
T. ACABDO CIELO RASO
N. NIVEL FINO
G. GUARDAESCOBA
H. ALTURA LIBRE

MATERIALES

G. GRANITO
MR. MARMOL
V. VINILO
L. LADRILLO TOLETE
BL. BLOQUE N°5
C. CONCRETO ABUJARDADO
C. CONCRETO ESMALTADO

LOCALIZACION:

NOTA: ESCALA **GRAFICA**
FECHA **2026**

Todas las Medidas deberán ser Rectificadas en Obra,
Cuenta y Riesgo de Cada uno de los Contratistas.

PLANO No: **A-005**
PLANCHA No: 05
DE: 05