
PLANTA · SALA DE RECIBO Y PRODUCCIÓN

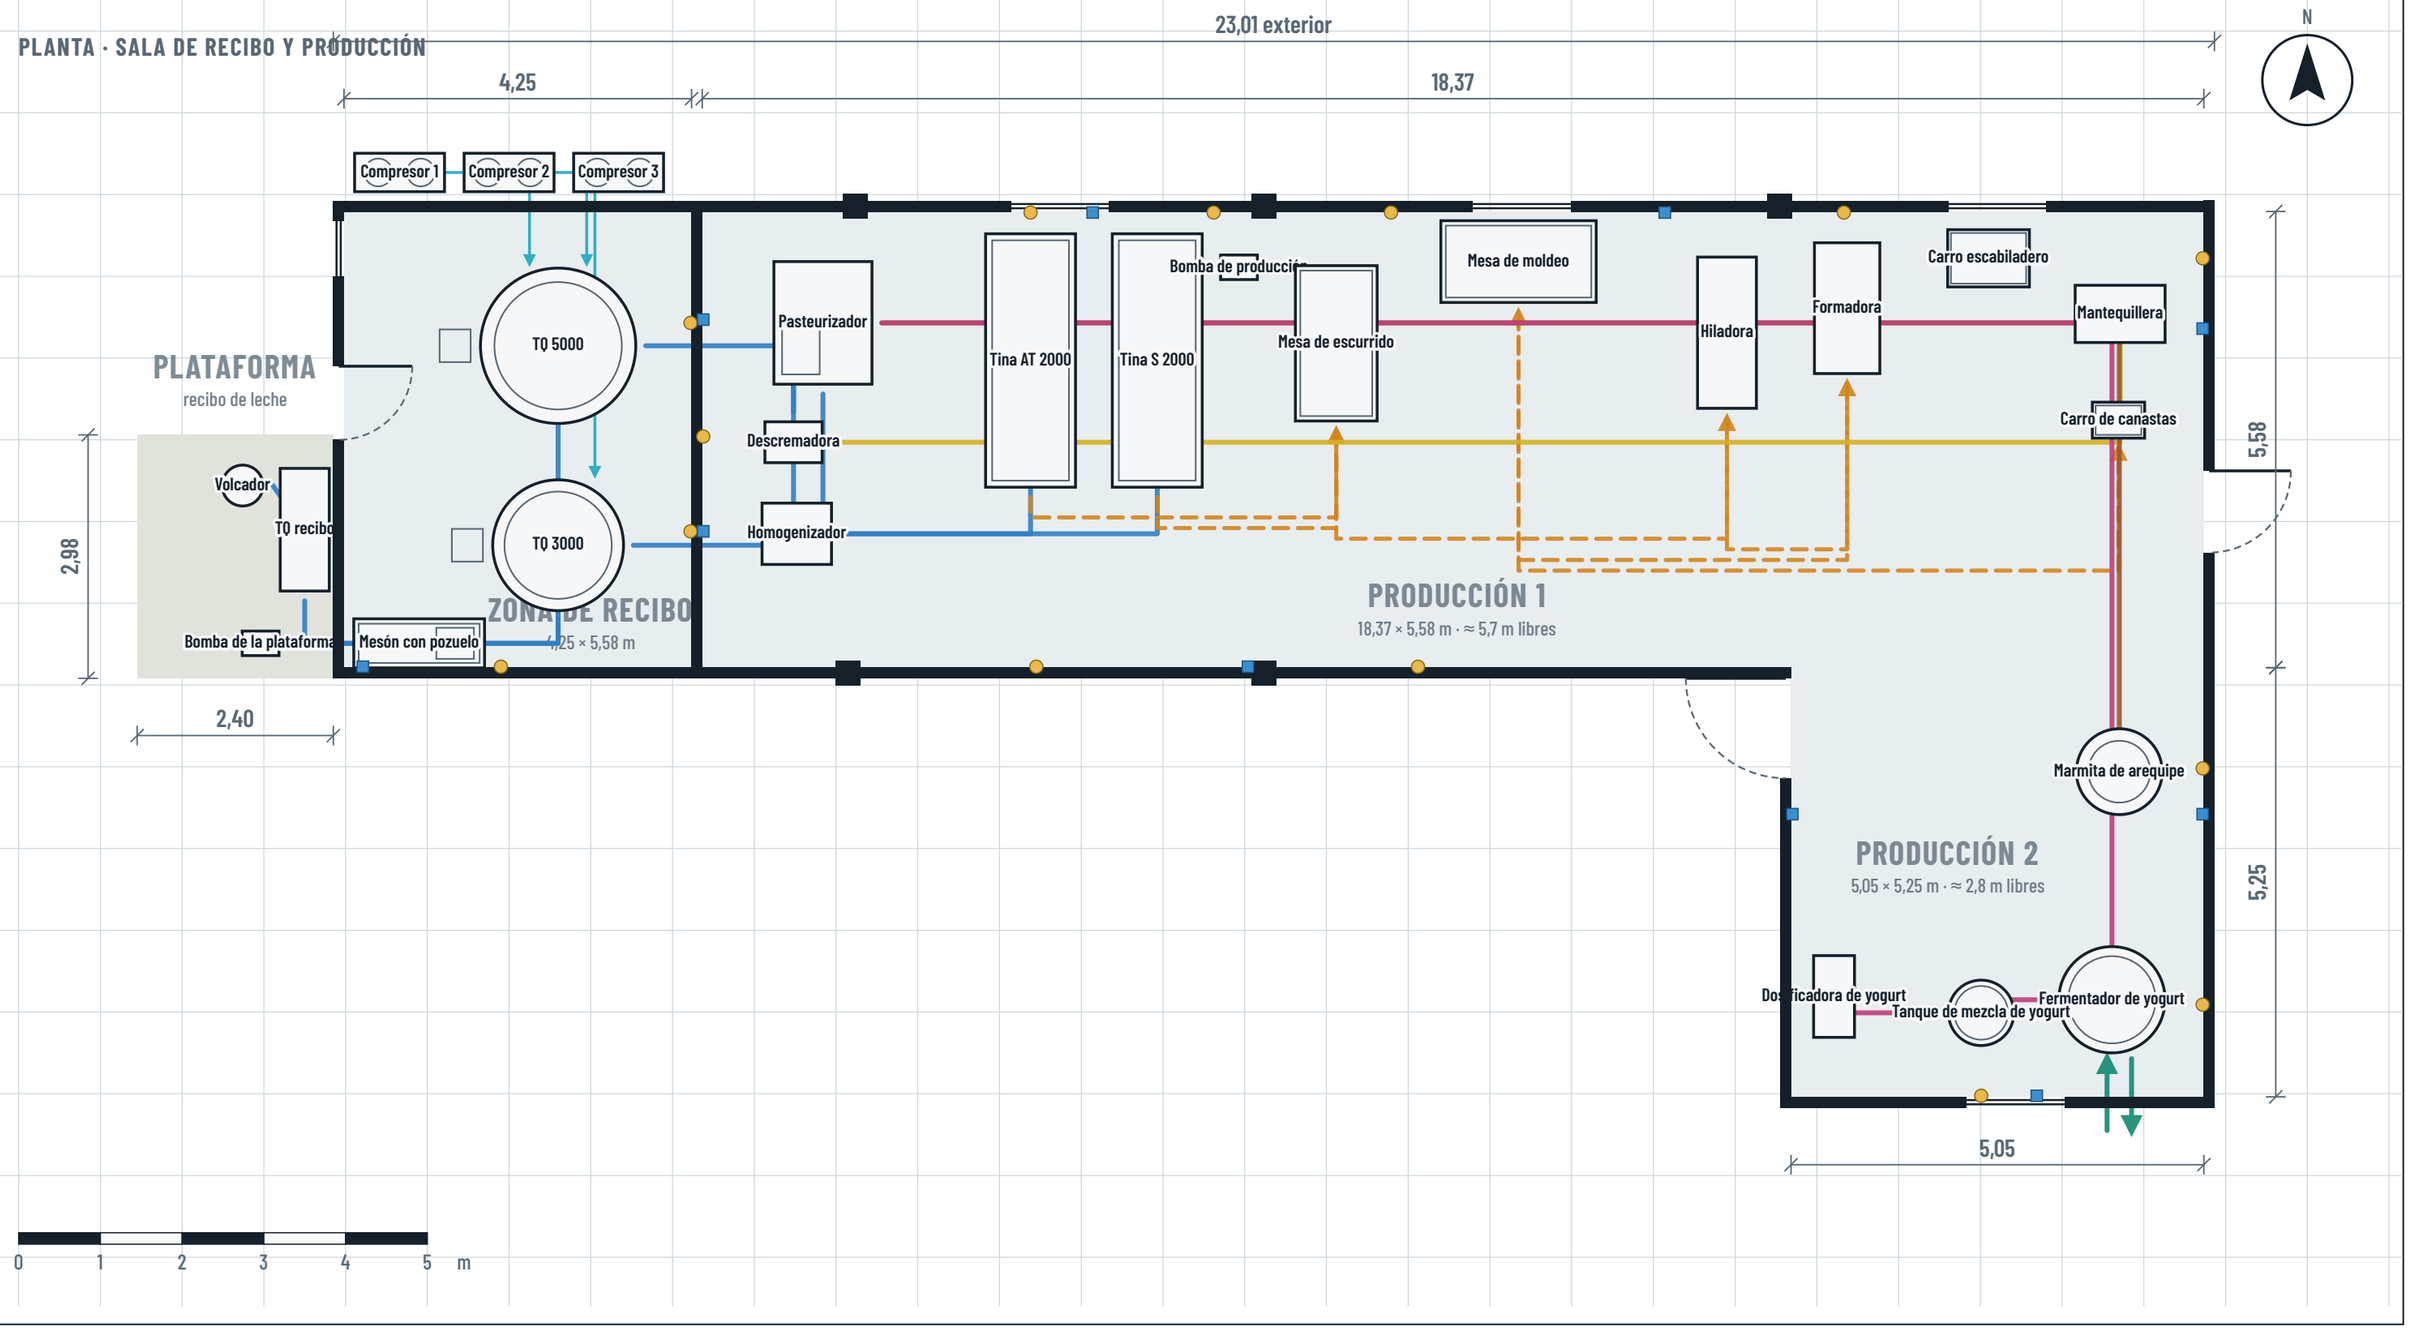

Industrias Equinox Colombia

PLANTA DE LÁCTEOS · MARULANDA, CALDAS

Sala de recibo y producción

Plano 2D de equipos y líneas de proceso · modelado preliminar

Escala	**1:75 en A3 · cotas interiores en metros**
Fecha	**10 de noviembre de 2026**
Visor	**planta-marulanda-3d.vercel.app**

LÍNEAS DE PROCESO Y TOMAS

- Leche
- Queso (traslado a mano)
- Crema
- Arequipe
- Yogurt
- Refrigeración de tanques
- Agua helada del chiller
- Toma eléctrica 220 V
- Toma de agua 1/2"

NOTAS

- Muros, puertas, ventanas y columnas: DWG arquitectónico, planta piso 1.
- Equipos: lista de dimensiones de la planta (10-nov-2026). Donde la lista no trae el alto se usó el del catálogo o uno estimado.
- Zona de recibo y plataforma: leídas a escala del plano de distribución de equipos.
- Tomas eléctricas y de agua: posición aproximada.

Diseño y modelado

Lukbyte

Soluciones digitales